

ÍNDICE DE PRANCHAS

01	Cozinha	4 pontos
02	Gourmet	1 pontos
03	Lavanderia	5 pontos
04	WC 01	7 pontos
05	WC 02	7 pontos
06	WC Suíte Master	7 pontos
07	WC Externo	7 pontos

REFERÊNCIA

Posição dos selos nesta planta é esquemática, apenas para localizar o ambiente. Eixos, alturas e cotas de execução estão nas pranchas 02 a 08 (uma por ambiente) e no Quadro de Pontos Hidráulicos, folha 09/09.

ESCALA

1/100

Imprimir em A3 sem ajuste de escala. Planta-base: PROJETO IVAN E ANA - R01, LayOut SketchUp (maio/2026).



Planta geral · pontos hidráulicos por ambiente

DUAS
design & arq

FOLHA
01/11

TIPO
Planta geral de pontos hidráulicos

OBRA
Design de interiores de casa unifamiliar térrea

CLIENTES
Ivan e Carol

ENDEREÇO
Nova Odessa, SP

ARO. RESPONSÁVEL
Arq. Lidiane Barbosa
CAU A290220-6

ARO. CORRESPONSÁVEL
Arq. Isadora Ferrari
CAU A269382-8

DATA
28/09/2026

REVISÃO N°
R01 ESCALA 1/100 aprox.

CONFERIR AS MEDIDAS NO LOCAL

LEGENDA

- A.F. Agua fria
- A.Q. Agua quente
- ESG Esgoto
- V.D. Valvula de descarga
- R.G. Registro geral
- ponto confirmado
- altura proposta (mercado) *
- eixo pendente de definição

REFERÊNCIA


Peça, altura, status e observações completas de cada ponto no Quadro de Pontos Hidráulicos, folha 09/09.

ESCALA

1/29



Imprimir em A3 sem ajuste de escala.

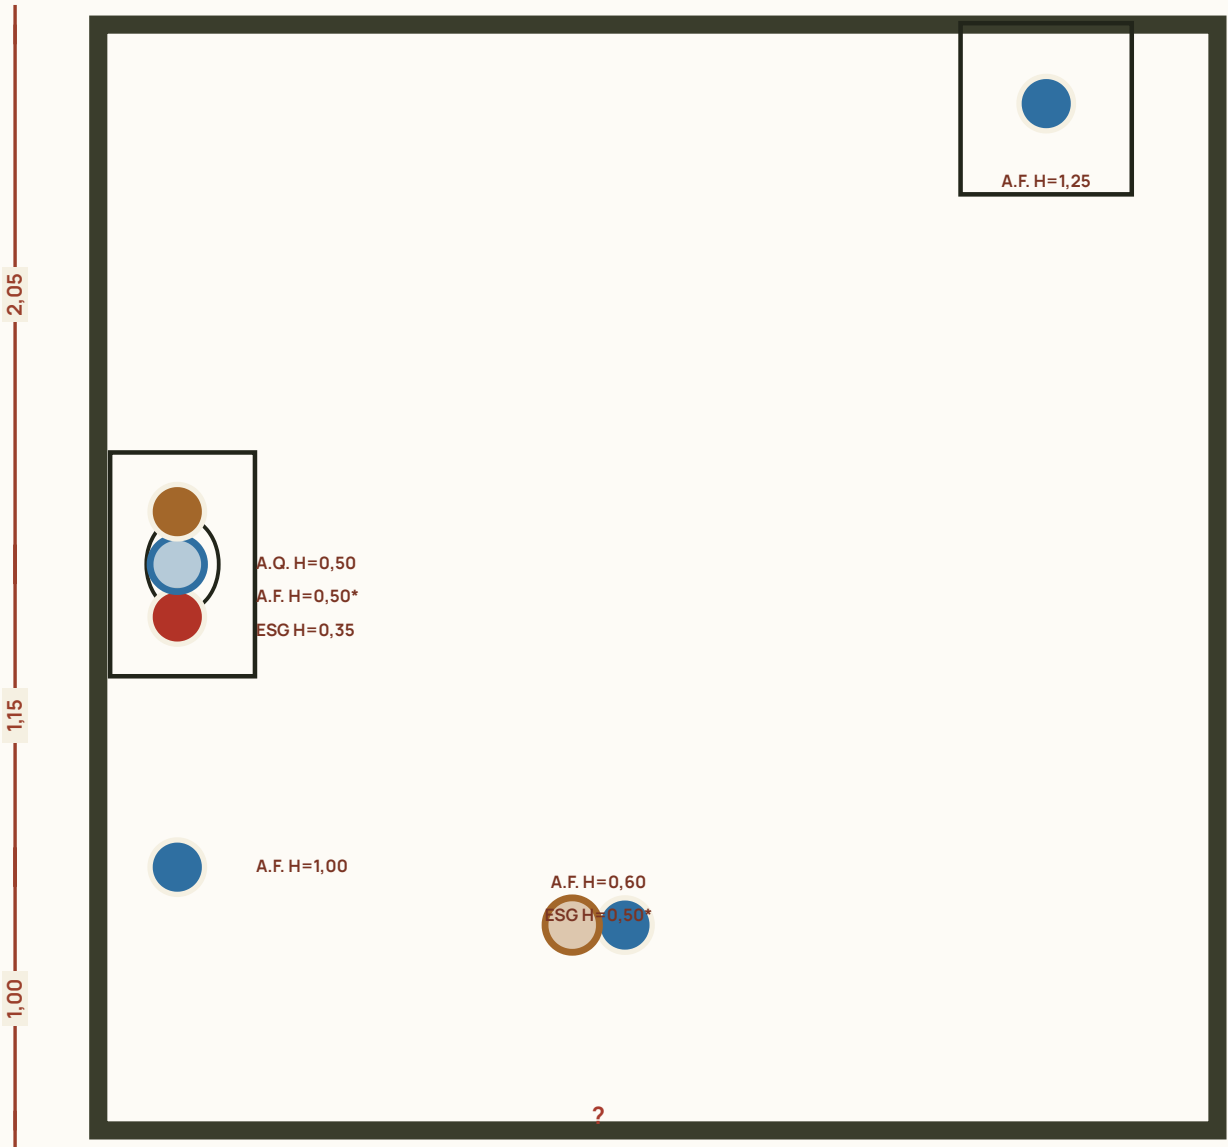

Cozinha · planta de pontos hidráulicos
ESCALA 1/29

DUAS
design & arq

FOLHA
02/11

TIPO
Planta de pontos hidráulicos · Cozinha

OBRA
Design de interiores de casa unifamiliar térrea

CLIENTES
Ivan e Carol

ENDEREÇO
Nova Odessa, SP


ARO. RESPONSÁVEL
Arq. Lidiane Barbosa
CAU A290220-6

ARO. CORRESPONSÁVEL
Arq. Isadora Ferrari
CAU A269382-8

DATA
28/09/2026

REVISÃO N°
R01 ESCALA 1/29

CONFERIR AS MEDIDAS NO LOCAL

 

Gourmet · planta de pontos hidráulicos

ESCALA 1/31

LEGENDA

- A.F. Agua fria
- A.Q. Agua quente
- ESG Esgoto
- V.D. Valvula de descarga
- R.G. Registro geral
- ponto confirmado
- altura proposta (mercado) *
- eixo pendente de definição

REFERÊNCIA

Peça, altura, status e observações completas de cada ponto no Quadro de Pontos Hidráulicos, folha 09/09.

ESCALA

1/31



Imprimir em A3 sem ajuste de escala.

DUAS
design & arq

FOLHA
03/11

TIPO
Planta de pontos hidráulicos · Gourmet

OBRA
Design de interiores de casa unifamiliar térrea

CLIENTES
Ivan e Carol

ENDEREÇO
Nova Odessa, SP


ARO. RESPONSÁVEL
Arq. Lidiane Barbosa
CAU A290220-6

ARO. CORRESPONSÁVEL
Arq. Isadora Ferrari
CAU A269382-8

DATA
28/09/2026

REVISÃO N°
R01 ESCALA 1/31

CONFERIR AS MEDIDAS NO LOCAL

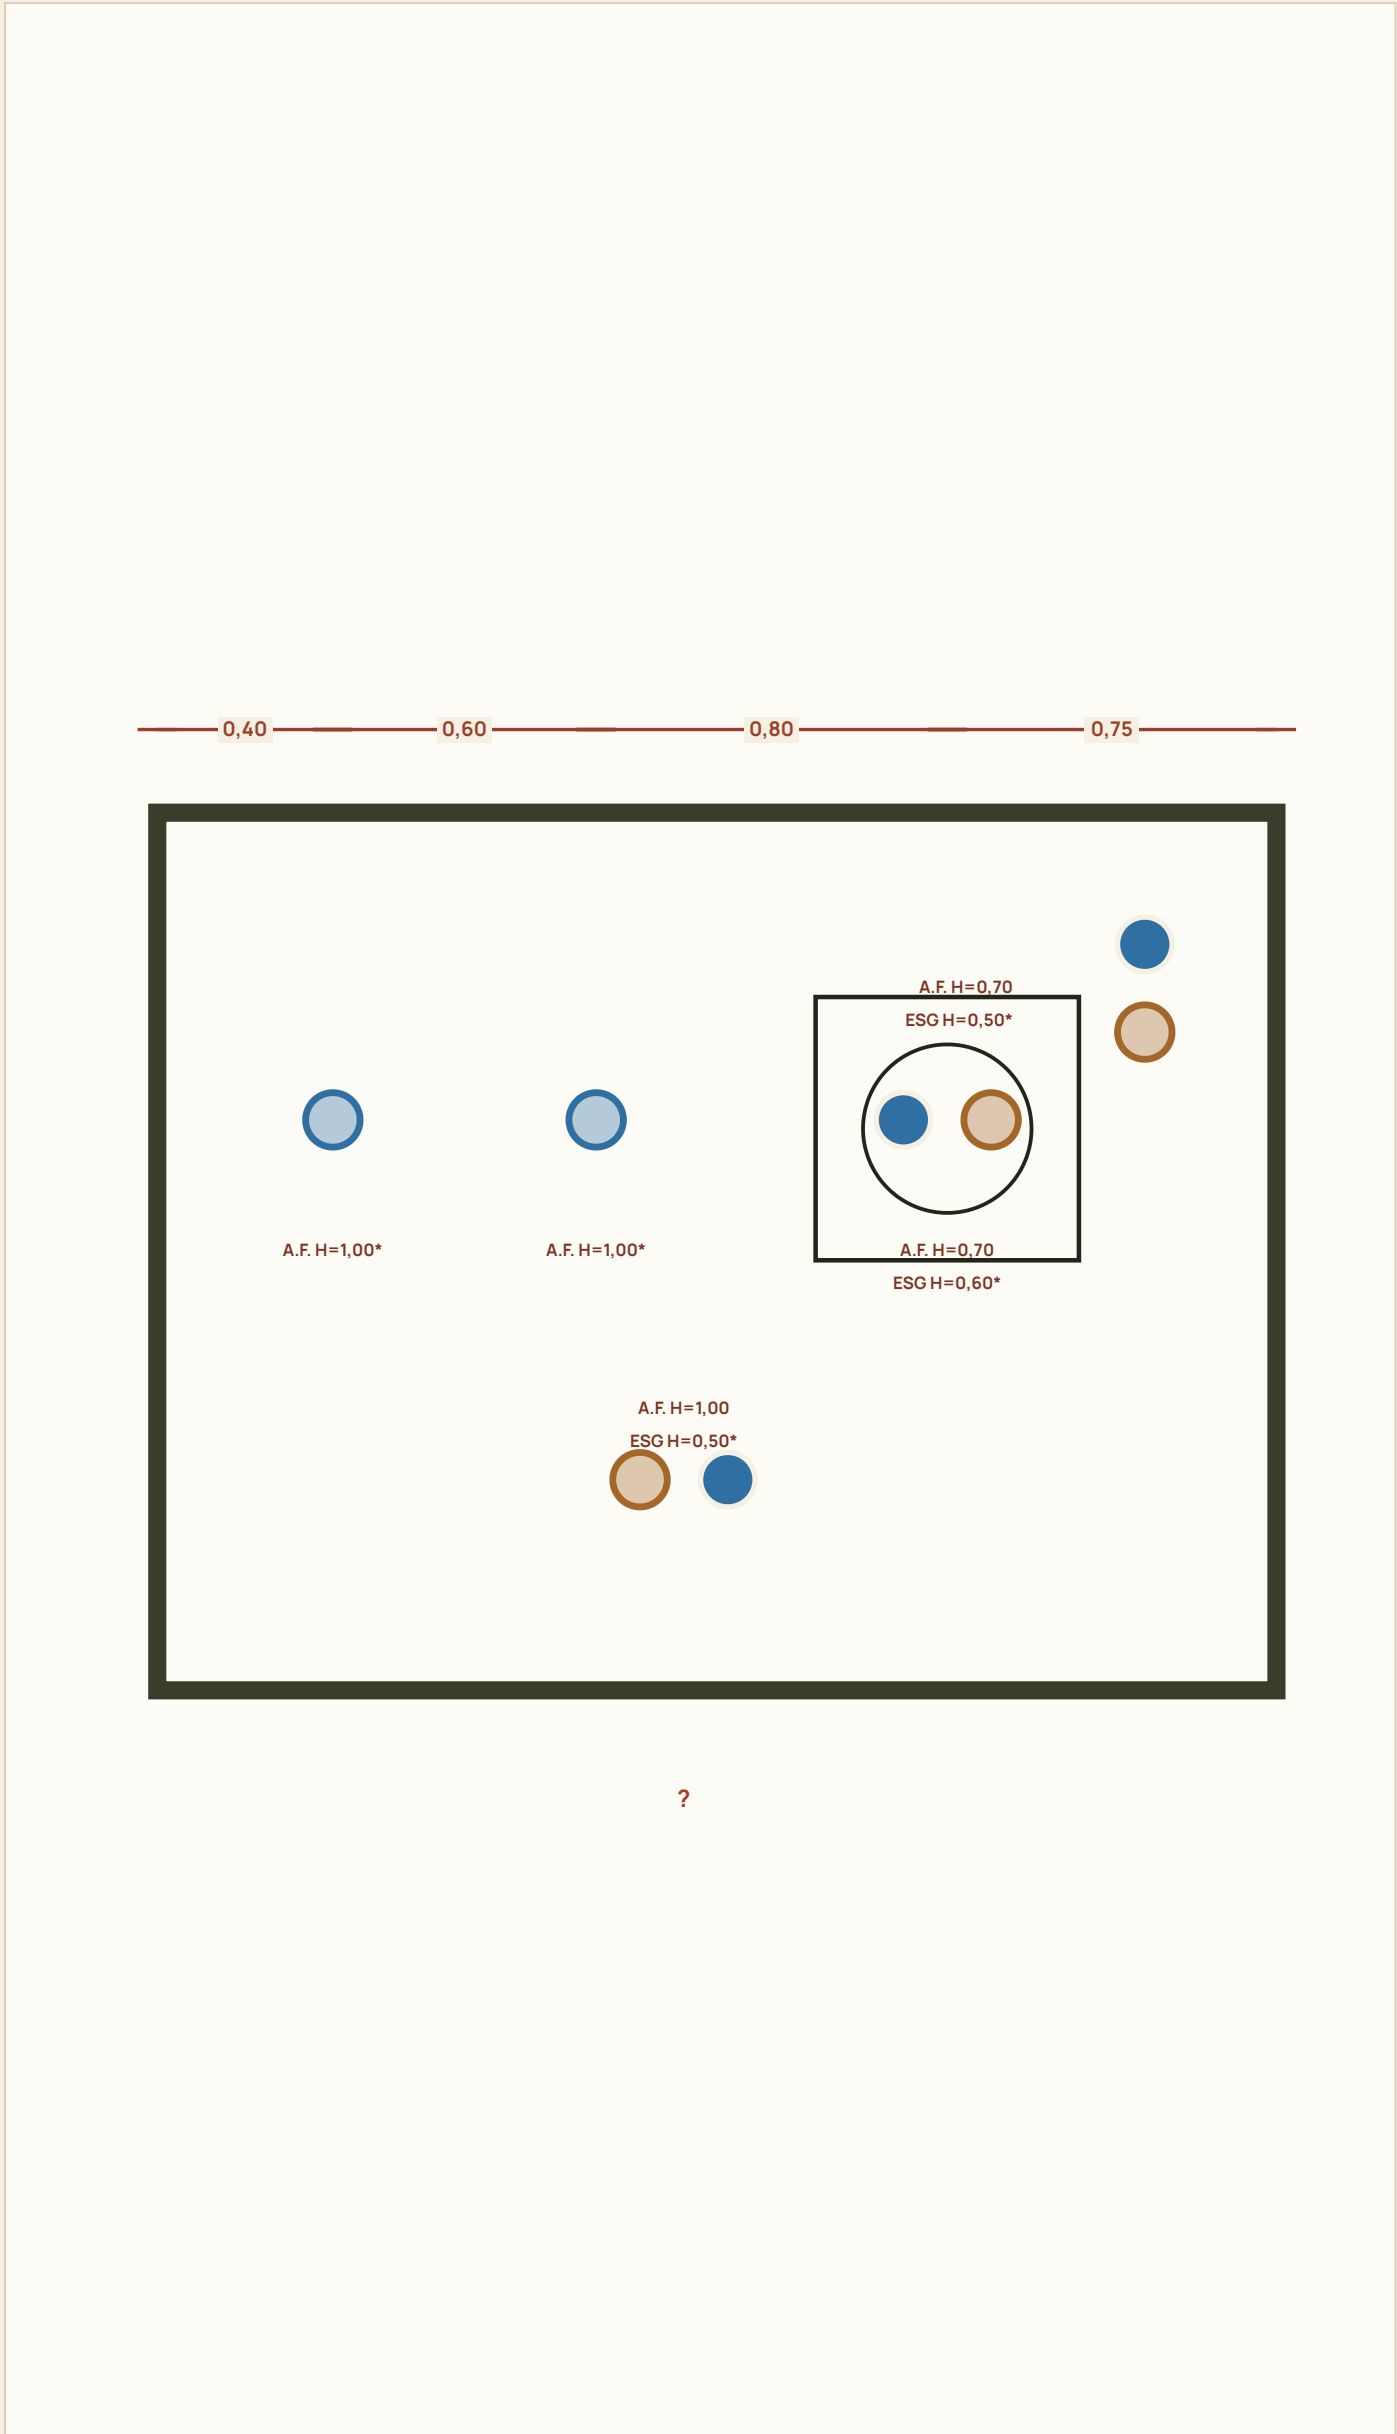

Lavanderia · planta de pontos hidráulicos
ESCALA 1/17

LEGENDA

- A.F. Agua fria
- A.Q. Agua quente
- ESG Esgoto
- V.D. Valvula de descarga
- R.G. Registro geral
- ponto confirmado
- altura proposta (mercado) *
- eixo pendente de definição

REFERÊNCIA

Peça, altura, status e observações completas de cada ponto no Quadro de Pontos Hidráulicos, folha 09/09.

ESCALA

1/17



Imprimir em A3 sem ajuste de escala.

DUAS
design & arq

FOLHA
04/11

TIPO
Planta de pontos hidráulicos · Lavanderia

OBRA
Design de interiores de casa unifamiliar térrea

CLIENTES
Ivan e Carol

ENDEREÇO
Nova Odessa, SP

ARO. RESPONSÁVEL
Arq. Lidiane Barbosa
CAU A290220-6

ARO. CORRESPONSÁVEL
Arq. Isadora Ferrari
CAU A269382-8

DATA
28/09/2026

REVISÃO N°
R01 ESCALA 1/17

CONFERIR AS MEDIDAS NO LOCAL

LEGENDA

- A.F. Agua fria
- A.Q. Agua quente
- ESG Esgoto
- V.D. Valvula de descarga
- R.G. Registro geral
- ponto confirmado
- altura proposta (mercado) *
- eixo pendente de definição

REFERÊNCIA


Peça, altura, status e observações completas de cada ponto no Quadro de Pontos Hidráulicos, folha 09/09.

ESCALA

1/20



Imprimir em A3 sem ajuste de escala.

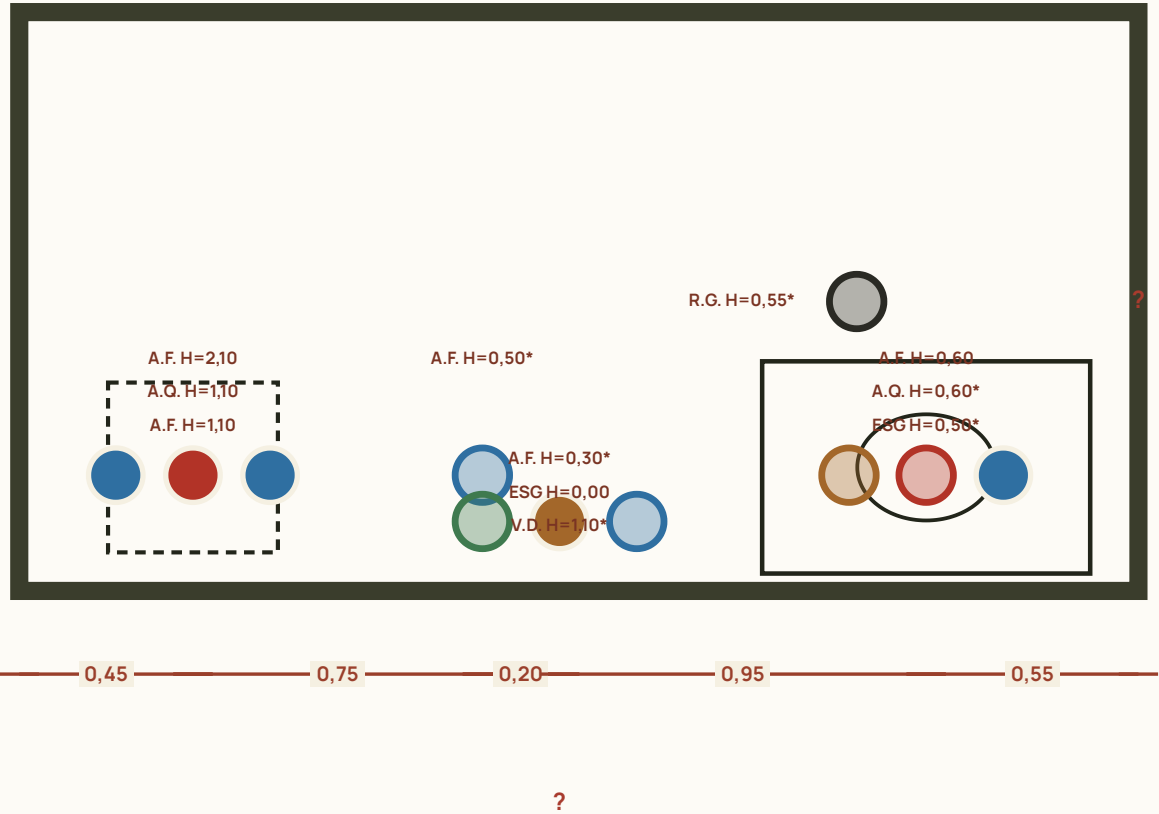

WC 01 · planta de pontos hidráulicos
ESCALA 1/20

DUAS
design & arq

FOLHA
05/11

TIPO
Planta de pontos hidráulicos · WC 01

OBRA
Design de interiores de casa unifamiliar térrea

CLIENTES
Ivan e Carol

ENDEREÇO
Nova Odessa, SP

ARO. RESPONSÁVEL
Arq. Lidiane Barbosa
CAU A290220-6

ARO. CORRESPONSÁVEL
Arq. Isadora Ferrari
CAU A269382-8

DATA
28/09/2026

REVISÃO N°
R01 ESCALA 1/20

CONFERIR AS MEDIDAS NO LOCAL

LEGENDA

- A.F. Agua fria
- A.Q. Agua quente
- ESG Esgoto
- V.D. Valvula de descarga
- R.G. Registro geral
- ponto confirmado
- altura proposta (mercado) *
- eixo pendente de definição

REFERÊNCIA


Peça, altura, status e observações completas de cada ponto no Quadro de Pontos Hidráulicos, folha 09/09.

ESCALA

1/20



Imprimir em A3 sem ajuste de escala.

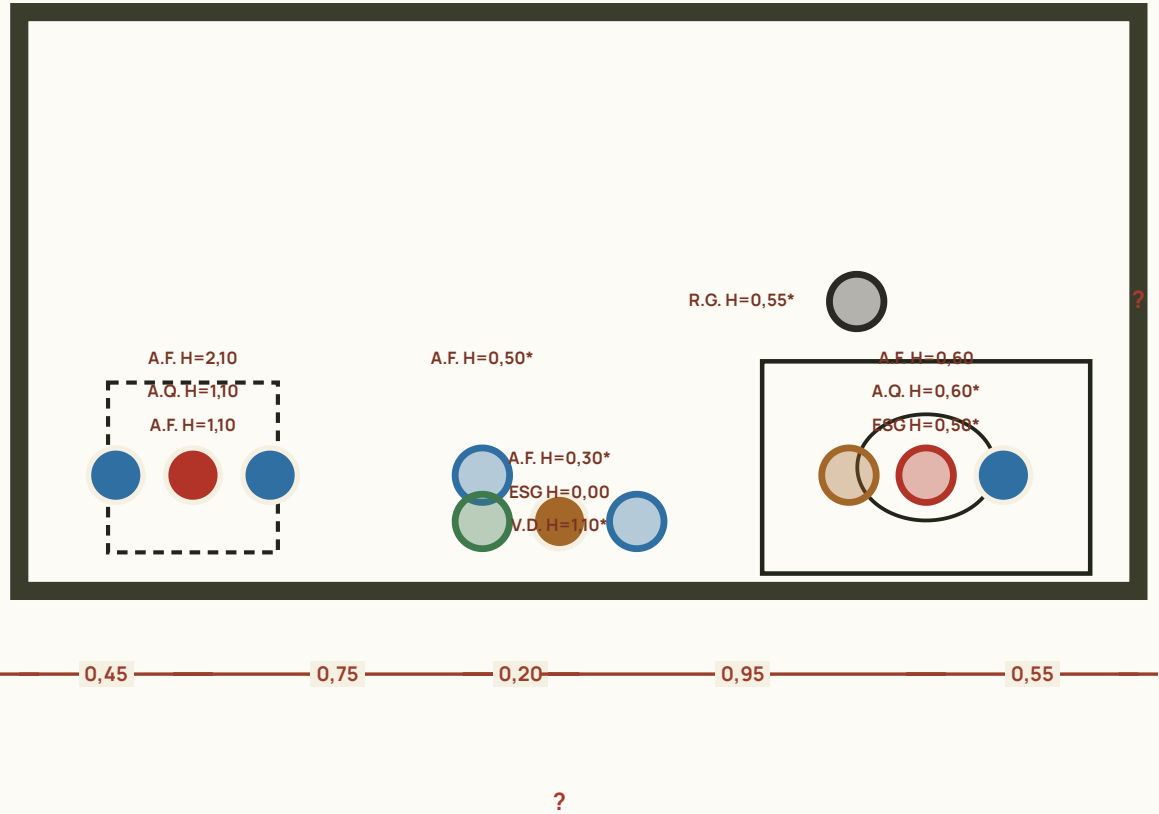

WC 02 · planta de pontos hidráulicos
ESCALA 1/20

DUAS
design & arq

FOLHA
06/11

TIPO
Planta de pontos hidráulicos · WC 02

OBRA
Design de interiores de casa unifamiliar térrea

CLIENTES
Ivan e Carol

ENDEREÇO
Nova Odessa, SP

ARO. RESPONSÁVEL
Arq. Lidiane Barbosa
CAU A290220-6

ARO. CORRESPONSÁVEL
Arq. Isadora Ferrari
CAU A269382-8

DATA
28/09/2026

REVISÃO N°
R01 ESCALA 1/20

CONFERIR AS MEDIDAS NO LOCAL

LEGENDA

- A.F. Agua fria
- A.Q. Agua quente
- ESG Esgoto
- V.D. Valvula de descarga
- R.G. Registro geral
- ponto confirmado
- altura proposta (mercado) *
- eixo pendente de definição

REFERÊNCIA


Peça, altura, status e observações completas de cada ponto no Quadro de Pontos Hidráulicos, folha 09/09.

ESCALA

1/13



Imprimir em A3 sem ajuste de escala.

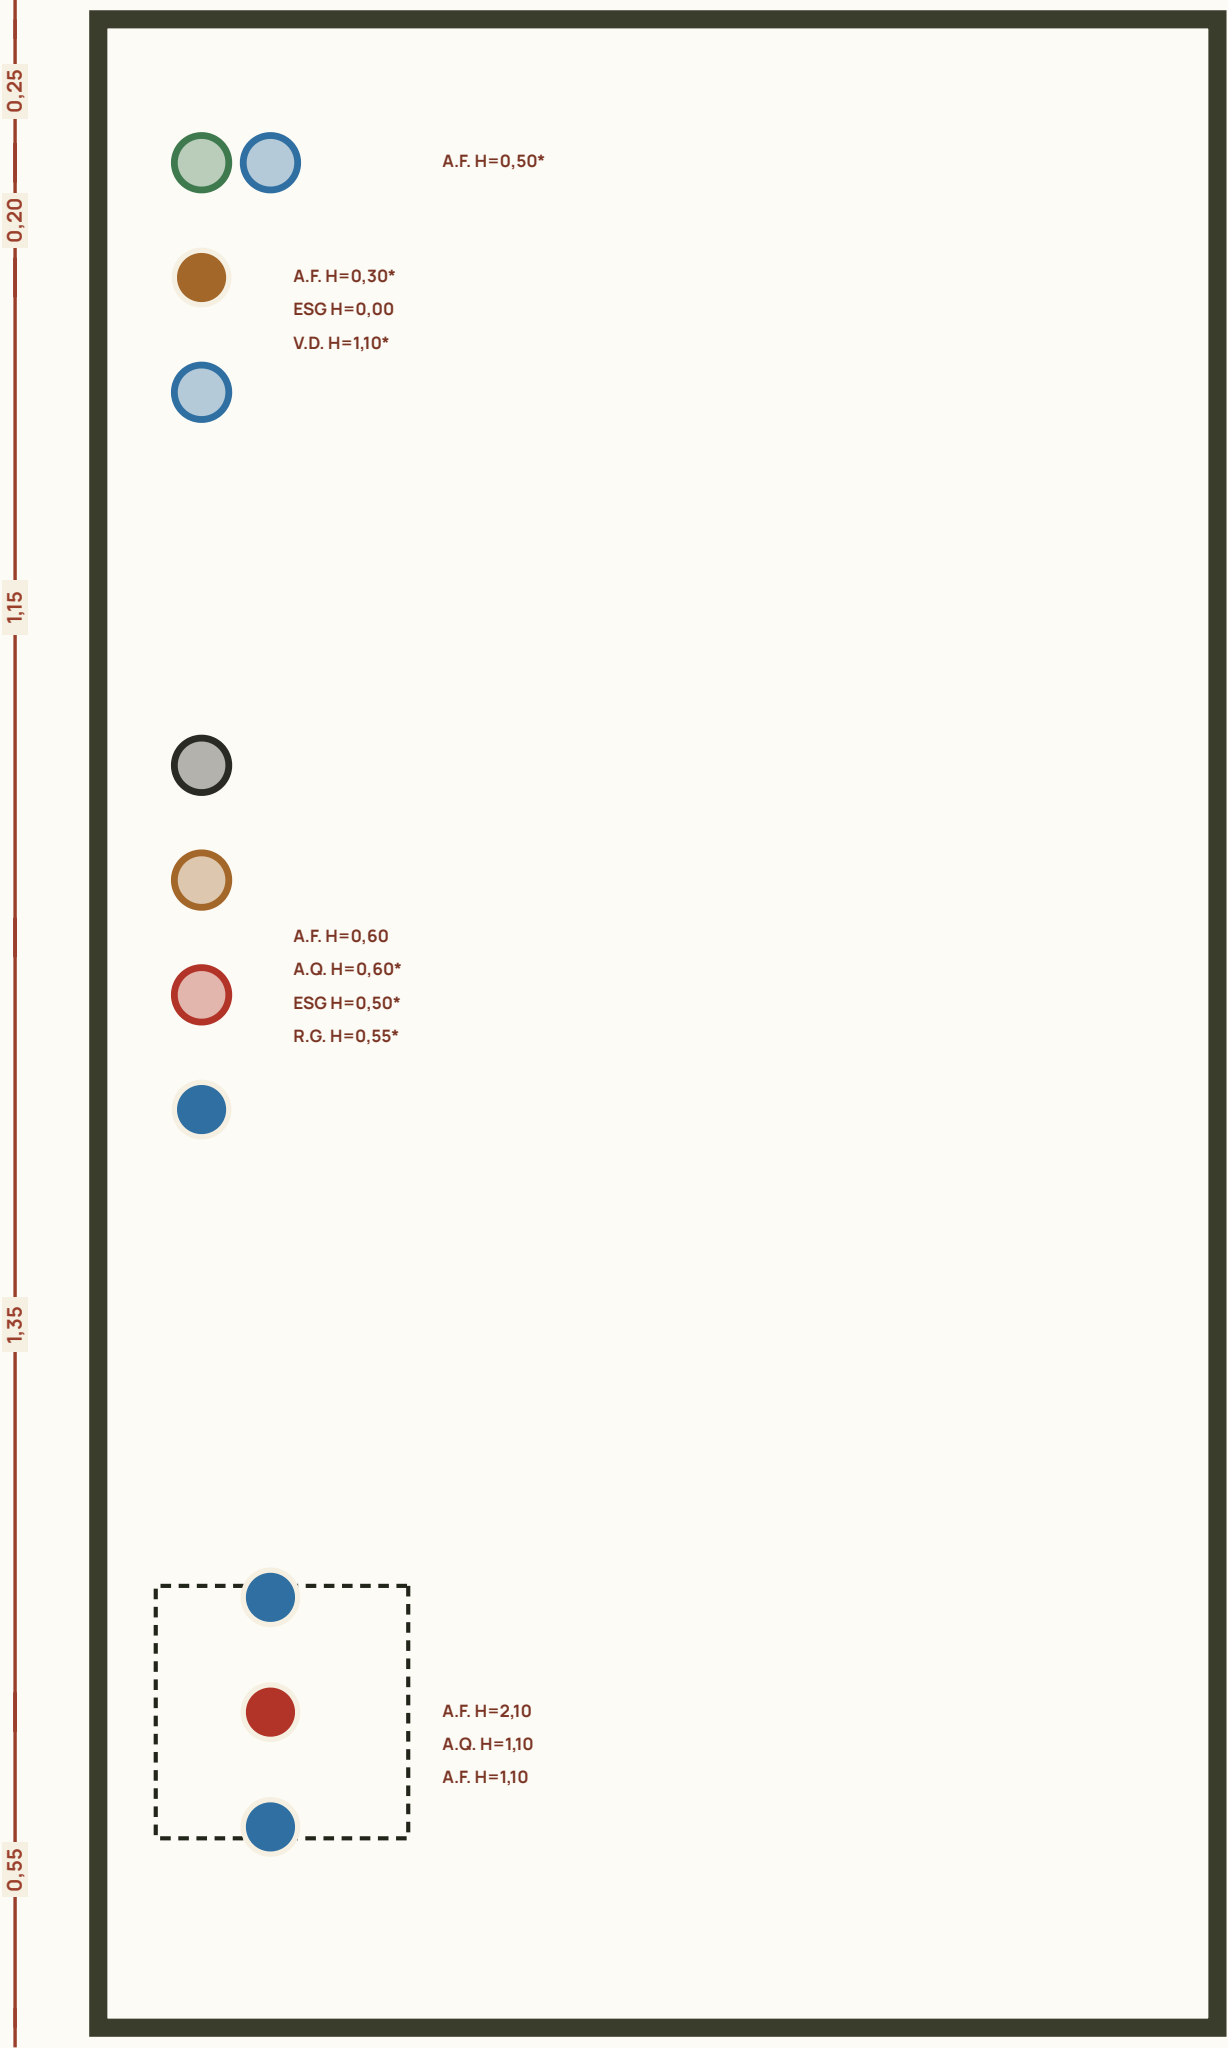

WC Suíte Master · planta de pontos hidráulicos
ESCALA 1/13

DUAS
design & arq

FOLHA
07/11

TIPO
Planta de pontos hidráulicos · WC Suíte Master

OBRA
Design de interiores de casa unifamiliar térrea

CLIENTES
Ivan e Carol

ENDEREÇO
Nova Odessa, SP

ARO. RESPONSÁVEL
Arq. Lidiane Barbosa
CAU A290220-6

ARO. CORRESPONSÁVEL
Arq. Isadora Ferrari
CAU A269382-8

DATA
28/09/2026

REVISÃO N°
R01 ESCALA 1/13

CONFERIR AS MEDIDAS NO LOCAL

LEGENDA

- A.F. Agua fria
- A.Q. Agua quente
- ESG Esgoto
- V.D. Valvula de descarga
- R.G. Registro geral
- ponto confirmado
- altura proposta (mercado) *
- eixo pendente de definição

REFERÊNCIA


Peça, altura, status e observações completas de cada ponto no Quadro de Pontos Hidráulicos, folha 09/09.

ESCALA

1/21



Imprimir em A3 sem ajuste de escala.

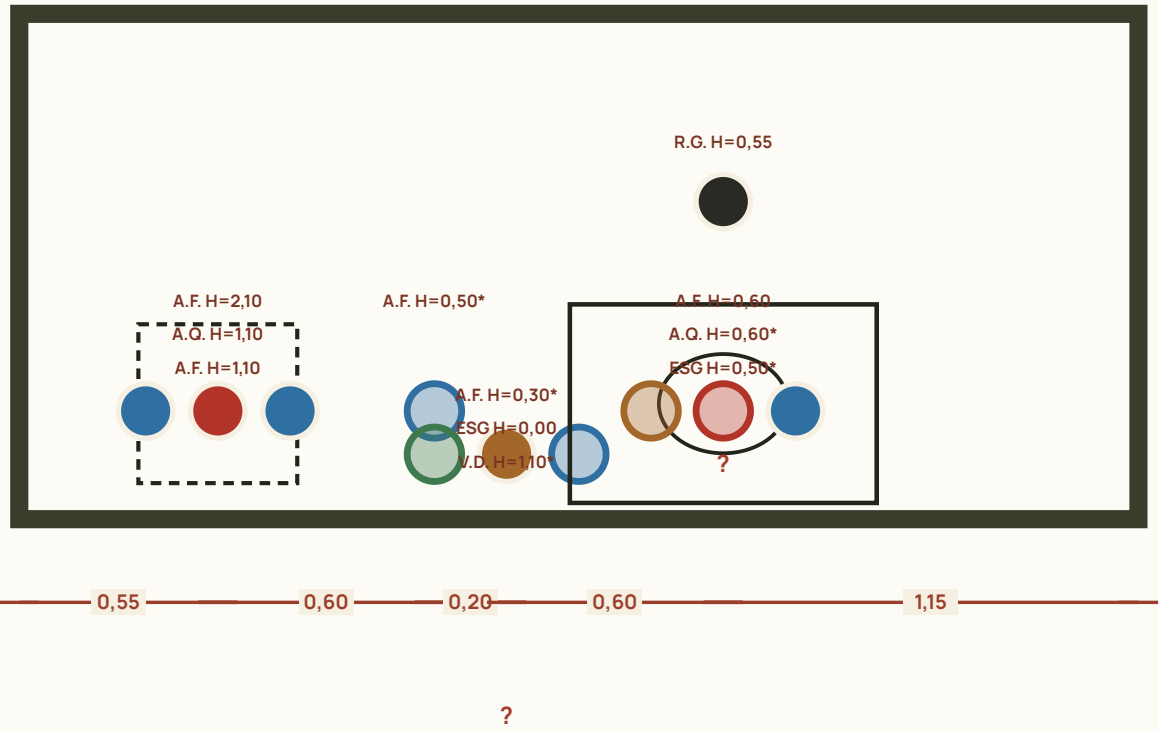

WC Externo · planta de pontos hidráulicos
ESCALA 1/21

DUAS
design & arq

FOLHA
08/11

TIPO
Planta de pontos hidráulicos · WC Externo

OBRA
Design de interiores de casa unifamiliar térrea

CLIENTES
Ivan e Carol

ENDEREÇO
Nova Odessa, SP

ARO. RESPONSÁVEL
Arq. Lidiane Barbosa
CAU A290220-6

ARO. CORRESPONSÁVEL
Arq. Isadora Ferrari
CAU A269382-8

DATA
28/09/2026

REVISÃO N°
R01 ESCALA 1/21

CONFERIR AS MEDIDAS NO LOCAL

Quadro de pontos hidráulicos (1/2)

Pt.	Peça	Tipo	Altura	Status altura	Status eixo	Observação
01 · COZINHA						
1	Filtro	A.F.	1,00 m	Confirmado	Confirmado	
2	Cuba pia · torneira de bancada	A.Q.	0,50 m	Confirmado	Confirmado	
		A.F.	0,50 m	Proposta *	Confirmado	mesma linha do A.Q. confirmado
		ESG	0,35 m	Confirmado	Confirmado	
3	Geladeira	A.F.	1,25 m	Confirmado	Confirmado	
4	Lava-louças (ilha)	A.F.	0,60 m	Confirmado	Pendente	
		ESG	0,50 m	Proposta *	Pendente	saida de sifao sob a cuba, pratica usual
02 · GOURMET						
1	Cuba · torneira de bancada	A.Q.	0,50 m	Confirmado	Pendente	
		A.F.	0,50 m	Proposta *	Pendente	mesma linha do A.Q. confirmado
		ESG	0,50 m	Proposta *	Pendente	saida de sifao sob a cuba, pratica usual
03 · LAVANDERIA						
1	Torneira de parede · tanque	A.F.	1,00 m	Proposta *	Confirmado	altura usual de torneira de parede alta para tanque
2	Torneira de parede · tanque	A.F.	1,00 m	Proposta *	Confirmado	altura usual de torneira de parede alta para tanque
3	Maquina de lavar roupas	A.F.	0,70 m	Confirmado	Confirmado	
		ESG	0,60 m	Proposta *	Confirmado	altura usual de saida da maquina de lavar
4	Tanquinho	A.F.	0,70 m	Confirmado	Confirmado	
		ESG	0,50 m	Proposta *	Confirmado	saida de sifao do tanquinho, pratica usual
5	A.F. + ESG da bancada do tanque	A.F.	1,00 m	Confirmado	Pendente	
		ESG	0,50 m	Proposta *	Pendente	saida de sifao, pratica usual
04 · WC 01						
1	Chuveiro (tipo ducha)	A.F.	2,10 m	Confirmado	Confirmado	
2	Registros do chuveiro	A.Q.	1,10 m	Confirmado	Confirmado	
		A.F.	1,10 m	Confirmado	Confirmado	
3	Ducha higienica	A.F.	0,50 m	Proposta *	Confirmado	altura usual de ducha higienica
4	Bacia sanitaria	A.F.	0,30 m	Proposta *	Confirmado	altura usual de alimentacao de caixa acoplada
		ESG	0,00 m	Confirmado	Confirmado	
5	Valvula de descarga	V.D.	1,10 m	Proposta *	Pendente	altura usual de acionamento de valvula de descarga
6	Cuba pia · torneira de bancada	A.F.	0,60 m	Confirmado	Confirmado	
		A.Q.	0,60 m	Proposta *	Confirmado	mesma linha do A.F. confirmado
		ESG	0,50 m	Proposta *	Confirmado	saida de sifao, pratica usual
7	Registro geral (dentro do armario)	R.G.	0,55 m	Proposta *	Pendente	valor confirmado no caderno original para o WC Externo (unico R.G. cotado na casa) — adotado aqui por analogia

DUAS

design & arq

FOLHA

09/11

TIPO

Quadro de pontos hidráulicos · tabela

OBRA

Design de interiores de casa unifamiliar térrea

CLIENTES

Ivan e Carol

ENDEREÇO

Nova Odessa, SP

ARO. RESPONSÁVEL

Arq. Lidiane Barbosa
CAU A290220-6

ARO. CORRESPONSÁVEL

Arq. Isadora Ferrari
CAU A269382-8

DATA

28/09/2026

REVISÃO N°

R01 ESCALA Sem escala

CONFERIR AS MEDIDAS NO LOCAL

Quadro de pontos hidráulicos (2/2)

Pt.	Peça	Tipo	Altura	Status altura	Status eixo	Observação
05 · WC 02						
1	Chuveiro (tipo ducha)	A.F.	2,10 m	Confirmado	Confirmado	
2	Registros do chuveiro	A.Q.	1,10 m	Confirmado	Confirmado	
		A.F.	1,10 m	Confirmado	Confirmado	
3	Ducha higienica	A.F.	0,50 m	Proposta *	Confirmado	altura usual de ducha higienica
4	Bacia sanitaria	A.F.	0,30 m	Proposta *	Confirmado	altura usual de alimentacao de caixa acoplada
		ESG	0,00 m	Confirmado	Confirmado	
5	Valvula de descarga	V.D.	1,10 m	Proposta *	Pendente	altura usual de acionamento de valvula de descarga
6	Cuba pia · torneira de bancada	A.F.	0,60 m	Confirmado	Confirmado	
		A.Q.	0,60 m	Proposta *	Confirmado	mesma linha do A.F. confirmado
		ESG	0,50 m	Proposta *	Confirmado	saida de sifao, pratica usual
7	Registro geral (dentro do armario)	R.G.	0,55 m	Proposta *	Pendente	valor confirmado no caderno original para o WC Externo (unico R.G. cotado na casa) — adotado aqui por analogia
06 · WC SUÍTE MASTER						
3	Ducha higienica	A.F.	0,50 m	Proposta *	Confirmado	altura usual de ducha higienica
4	Bacia sanitaria	A.F.	0,30 m	Proposta *	Confirmado	altura usual de alimentacao de caixa acoplada
		ESG	0,00 m	Confirmado	Confirmado	
5	Valvula de descarga	V.D.	1,10 m	Proposta *	Pendente	altura usual de acionamento de valvula de descarga
6	Cuba pia · torneira de bancada	A.F.	0,60 m	Confirmado	Confirmado	
		A.Q.	0,60 m	Proposta *	Confirmado	mesma linha do A.F. confirmado
		ESG	0,50 m	Proposta *	Confirmado	saida de sifao, pratica usual
1	Chuveiro (tipo ducha)	A.F.	2,10 m	Confirmado	Confirmado	
2	Registros do chuveiro	A.Q.	1,10 m	Confirmado	Confirmado	
		A.F.	1,10 m	Confirmado	Confirmado	
7	Registro geral (dentro do armario)	R.G.	0,55 m	Proposta *	Pendente	valor confirmado no caderno original para o WC Externo (unico R.G. cotado na casa) — adotado aqui por analogia
07 · WC EXTERNO						
1	Chuveiro (tipo ducha)	A.F.	2,10 m	Confirmado	Confirmado	
2	Registros do chuveiro	A.Q.	1,10 m	Confirmado	Confirmado	
		A.F.	1,10 m	Confirmado	Confirmado	
3	Ducha higienica	A.F.	0,50 m	Proposta *	Confirmado	altura usual de ducha higienica
4	Bacia sanitaria	A.F.	0,30 m	Proposta *	Confirmado	altura usual de alimentacao de caixa acoplada
		ESG	0,00 m	Confirmado	Confirmado	
5	Valvula de descarga	V.D.	1,10 m	Proposta *	Pendente	altura usual de acionamento de valvula de descarga
6	Cuba pia · torneira de bancada	A.F.	0,60 m	Confirmado	Confirmado	
		A.Q.	0,60 m	Proposta *	Confirmado	mesma linha do A.F.
		ESG	0,50 m	Proposta *	Confirmado	saida de sifao, pratica usual
7	Registro geral (dentro do armario)	R.G.	0,55 m	Confirmado	Pendente	

DUAS

design & arq

FOLHA

10/11

TIPO

Quadro de pontos hidráulicos · tabela

OBRA

Design de interiores de casa unifamiliar térrea

CLIENTES

Ivan e Carol

ENDEREÇO

Nova Odessa, SP

ARO. RESPONSÁVEL

Arq. Lidiane Barbosa
CAU A290220-6

ARO. CORRESPONSÁVEL

Arq. Isadora Ferrari
CAU A269382-8

DATA

28/09/2026

REVISÃO N°

R01 ESCALA Sem escala

CONFERIR AS MEDIDAS NO LOCAL

Status, pendências e normas

STATUS

Confirmado — dado do Caderno Detalhamento Hidráulico original (Revisão 02, 24/09/2026) ou decisão explícita do cliente em 28/09/2026. Pode ser executado.

Proposta * — valor usual de mercado, adotado na ausência de cota no caderno original, a pedido do cliente (28/09/2026). Precisa de validação do responsável pelo projeto hidrossanitário antes da execução.

Pendente — posição em planta sem cota no caderno original e sem base segura para propor. Afeta o eixo do ponto, não apenas a altura.

PENDÊNCIAS EM ABERTO

1. Posição da ilha da cozinha em relação à parede — necessária para converter o eixo do lava-louças. Falta medida direta ou modelo SketchUp detalhado da marcenaria.
2. Afastamento da parede esquerda da cuba/torneira de bancada do Gourmet — não consta no caderno original.
3. Prancha 01/02 do Caderno de Ar Condicionado — só foi recebida a 02/02; pode conter dreno de condensado que intercepte shafts hidráulicos.
4. Eixo dos registros gerais (dentro dos armários) em todos os banheiros — posição de projeto, não um dado padronizável.
5. WC Suíte Master: falta a cota de fechamento da cuba/torneira de bancada contra a parede lateral oposta.

NORMAS DE REFERÊNCIA

- NBR 5626** Instalações prediais de água fria.
- NBR 7198** Instalações prediais de água quente.
- NBR 8160** Sistemas prediais de esgoto sanitário.

DUAS
design & arq

FOLHA
11/11

TIPO
Quadro de pontos hidráulicos · status e pendências

OBRA
Design de interiores de casa unifamiliar térrea

CLIENTES
Ivan e Carol

ENDEREÇO
Nova Odessa, SP

ARO. RESPONSÁVEL
Arq. Lidiane Barbosa
CAU A290220-6

ARO. CORRESPONSÁVEL
Arq. Isadora Ferrari
CAU A269382-8

DATA
28/09/2026

REVISÃO N°
R01 ESCALA Sem escala

CONFERIR AS MEDIDAS NO LOCAL