


# Planta-chave e índice

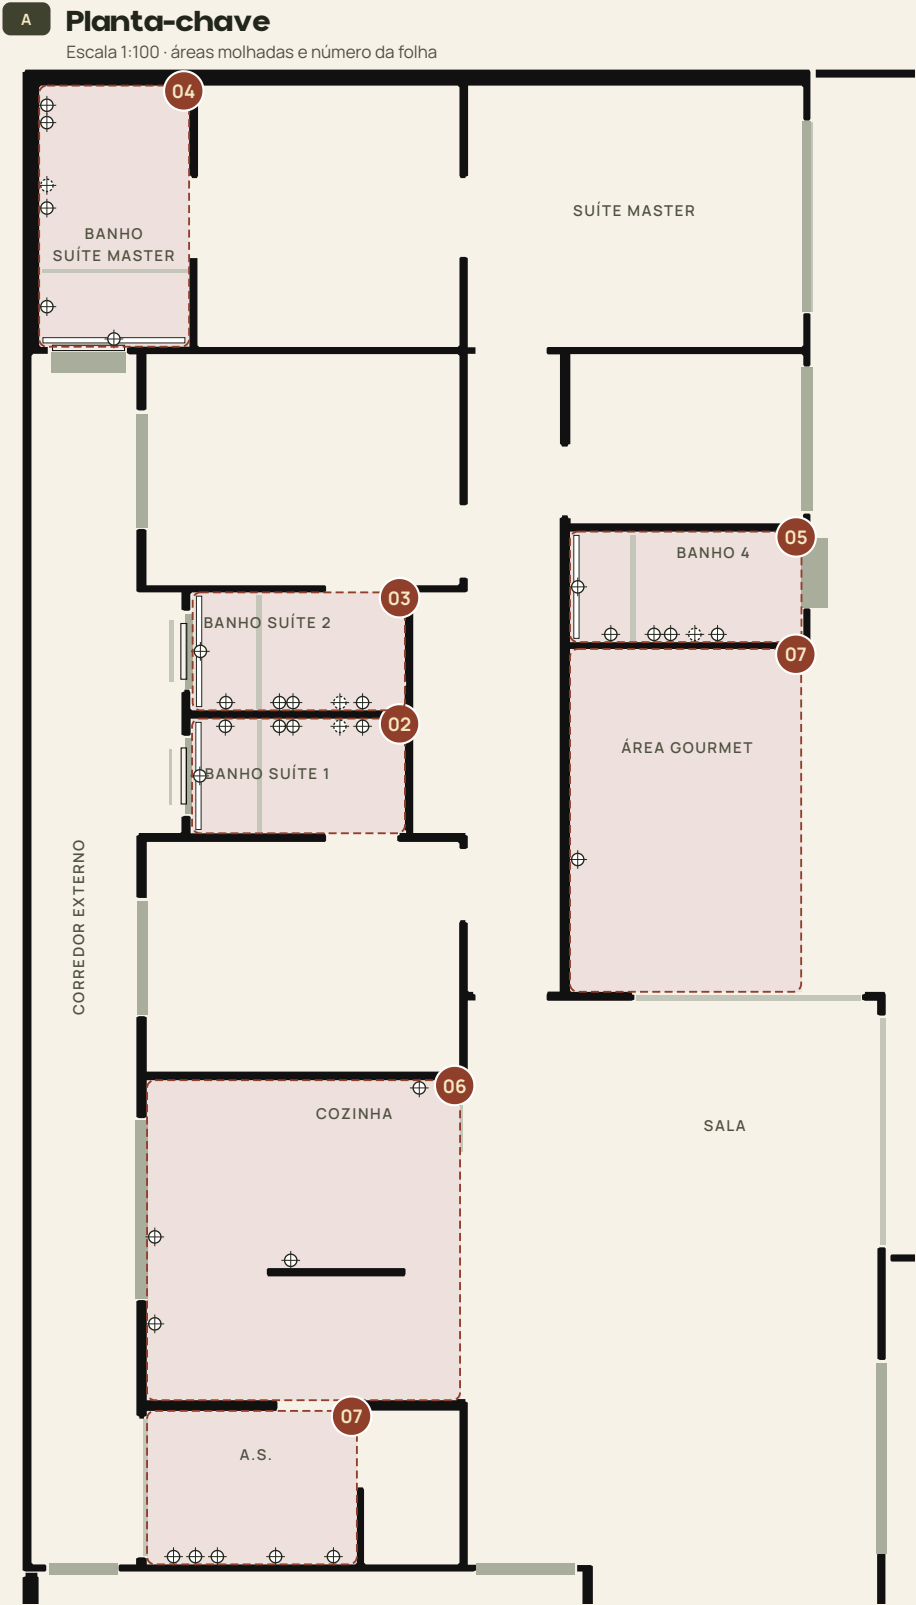

## Índice

|    |                                        |             |
|----|----------------------------------------|-------------|
| 01 | Planta-chave, índice e legenda         | 1/100       |
| 02 | Banho Suíte 1                          | 1/25        |
| 03 | Banho Suíte 2                          | 1/25        |
| 04 | Banho Suíte Master                     | 1/25        |
| 05 | Banho 4                                | 1/25        |
| 06 | Cozinha                                | 1/50 · 1/25 |
| 07 | Área Gourmet e A.S.                    | 1/50 · 1/25 |
| 08 | Detalhes: ralo, box, nicho, acessórios | indicadas   |
| 09 | Louças e metais                        | —           |

## Legenda

- Água fria
- Água quente
- Esgoto
- Registro geral
- Saída de chuveiro (misturada)
- Gás (GLP)
- Ponto com eixo sem cota
- Código do ponto (= pranchas R04)
- Ralo linear (indicativo)
- Vidro do box (de correr)
- Área detalhada · nº da folha

### REVESTIMENTOS DE PAREDE

- RP02 Porcelanato Santorini OFW NAT**  
Portinari
- RP03 Porcelanato Confete WH NAT**  
Ceusa · cód. 5041209A
- RP04 Porcelanato Confete PK NAT (Pink)**  
Ceusa · cód. 5041210A
- RP05 Revestimento Fatto Oliva AC**  
Decortiles · SC 8068139
- RP06 Travertino Rock Face**  
Pedreira (compra à parte)
- RP07 Cerâmica simples (fundo da marcenaria)**  
Eliane · SC 8039383

### STATUS DAS INFORMAÇÕES

- DOCUMENTADO** consta nos arquivos ou foi definido pelo cliente
- PROPOSTA** proposta do escritório: aprovar
- A DEFINIR** falta definição: não executar sem ela
- A CONFIRMAR** há divergência entre arquivos: conferir

## Observações gerais

- Escopo** Detalhamento arquitetônico das áreas molhadas: pontos, box, ralo, nicho, revestimentos e louças. Não é projeto hidrossanitário nem de impermeabilização.
- Base** Planta de 29/09 (Tomadas R05 / Pontos Hidráulicos). Pontos e alturas iguais às pranchas hidráulicas R04.
- Alturas** Do piso acabado. Forro +2,85 nos banhos, cozinha e A.S. (caderno de forro R01).
- Fontes** Revestimentos de parede e piso R00, forro R01, lista de louças e metais (25/09), decisões do cliente de 30/09 e 02/10.
- Nomes** Ambientes com os nomes da planta elétrica (decisão de 02/10).

### PENDÊNCIAS E DIVERGÊNCIAS

- Vãos** Os cadernos de revestimento R00 e o de forro usam a geometria do DWG R01 (boxes de 0,90; Banho 4 com 3,30). Este caderno segue a planta de 29/09: revisar quantitativos.  
**A CONFIRMAR**
- Forro R01** Diz "revestimento cerâmico total nos banhos"; a definição de 02/10 é revestir só o box.  
**A CONFIRMAR**
- CAU** Cadernos de piso e parede R00 trazem A269382-8; o correto é A263982-8.  
**A CONFIRMAR**
- Registros** Chuveiros: afastamento entre registros AF/AQ já executados a medir em obra.  
**A CONFIRMAR**

- Roca ONA** Altura do ponto AF (0,30) a conferir na ficha técnica.  
**A CONFIRMAR**
- Box** Lado da folha fixa e ferragem.  
**A DEFINIR**
- Ralo** Modelo, comprimento, caimento e desnível; impermeabilização pelo responsável técnico.  
**A DEFINIR**
- Gourmet** Posição da churrasqueira e altura da boca (caderno R00: a confirmar).  
**A CONFIRMAR**



- STATUS
- DOCUMENTADO
  - PROPOSTA
  - A DEFINIR
  - A CONFIRMAR



FOLHA

01/09

TIPO

## Planta-chave e índice

**OBRA**  
Residência Ivan e Ana Neris · casa unifamiliar térrea

**CLIENTES**  
Ivan e Ana Neris

**ARQ. RESPONSÁVEL**  
Lidiane Barbosa  
CAU A290220-6

**DATA**  
02/10/2026

**ENDEREÇO**  
Nova Odessa, SP

**ARQ. CORRESPONSÁVEL**  
Isadora Ferrari  
CAU A263982-8

**REVISÃO**  
Nº 00


**ESCALA**  
1/100

CONFERIR AS MEDIDAS NO LOCAL

# Banho Suíte 1

## A Planta · pontos e box

Escala 1:25 · cotas em metros a partir da face da parede indicada

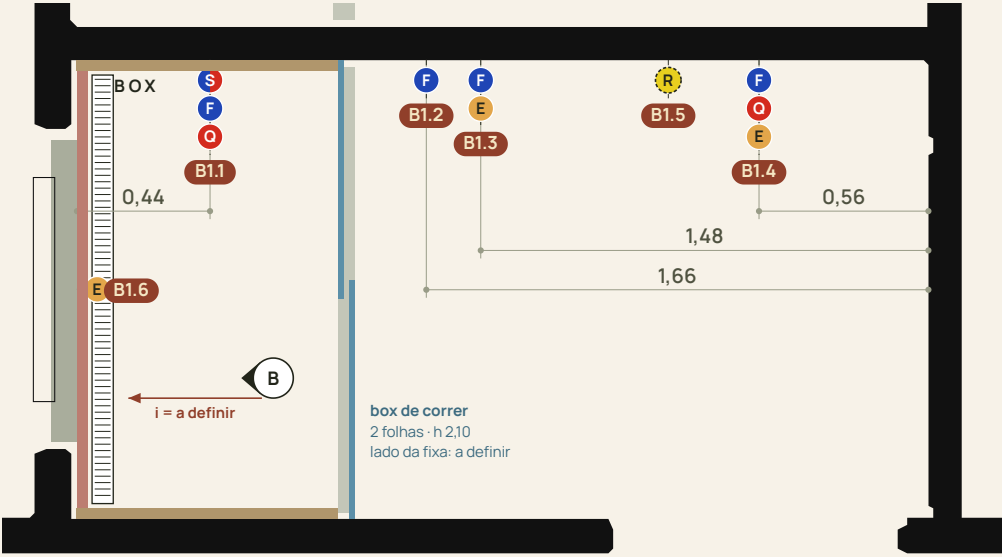

## Pontos e alturas

ALTURA (M) · FONTE

- B1.1

Chuveiro

0,44 da parede esquerda

S

2,10<sup>C</sup>

F

1,10<sup>C</sup>

Q

1,10<sup>C</sup>
- B1.2

Ducha higiênica

1,66 da parede direita

F

0,50<sup>P</sup>
- B1.3

Bacia sanitária

1,48 da parede direita

F

0,30<sup>P</sup>

E

piso<sup>C</sup>
- B1.4

Cuba · misturador de mesa

0,56 da parede direita

F

0,60<sup>C</sup>

Q

0,60<sup>D</sup>

E

0,50<sup>P</sup>
- B1.5

Registro geral

sem cota · dentro do armário

R

0,55<sup>P</sup>
- B1.6

Ralo linear do box

junto à parede do fundo do box · comprimento a definir

E

piso<sup>D</sup>

Fontes: C caderno Hidráulica Rev. 02 · D definição do cliente · P padrão do escritório.

## Elementos

- Box

Vidro de correr, 2 folhas (1 fixa + 1 de correr), h 2,10 do piso acabado; não vai até o forro.

DOCUMENTADO
- Folha fixa

Lado da folha fixa, ferragem e perfis (lista de louças: previsão cromada).

A DEFINIR
- Vão do box

Fundo 1,52 × lateral 0,86 (planta 29/09). Caderno de revestimentos R00: 1,50 × 0,90.

A CONFIRMAR
- Ralo

Linear, junto à parede do fundo do box; não há ralo fora do box. Modelo, comprimento e caimento a definir.

DOCUMENTADO
- Revestimento

Box: laterais RP02 e fundo RP04 até o forro (2,85). Demais paredes em pintura: ducha higiênica, bacia e cuba na pintura.

DOCUMENTADO
- Nicho

0,30 × 0,10, base a 1,00, em toda a largura do fundo (caderno R00). Parede de ≈0,15 na planta: conferir a profundidade.

A CONFIRMAR
- Janela J04

1,00 × 0,60, peitoril 1,50 (02/10), no fundo do box.

DOCUMENTADO
- Piso

P01 Santorini OFW NAT 90 × 90 (caderno de pisos R00), inclusive no box.

DOCUMENTADO
- Bancada

Bancada da cuba: prancha de marmoraria (a desenvolver).


A DEFINIR
- Acessórios

Alturas propostas na folha 08.

PROPOSTA

## B Box e parede das peças · planificados

Escala 1:25 · vistos de dentro, da esquerda para a direita · alturas do piso acabado

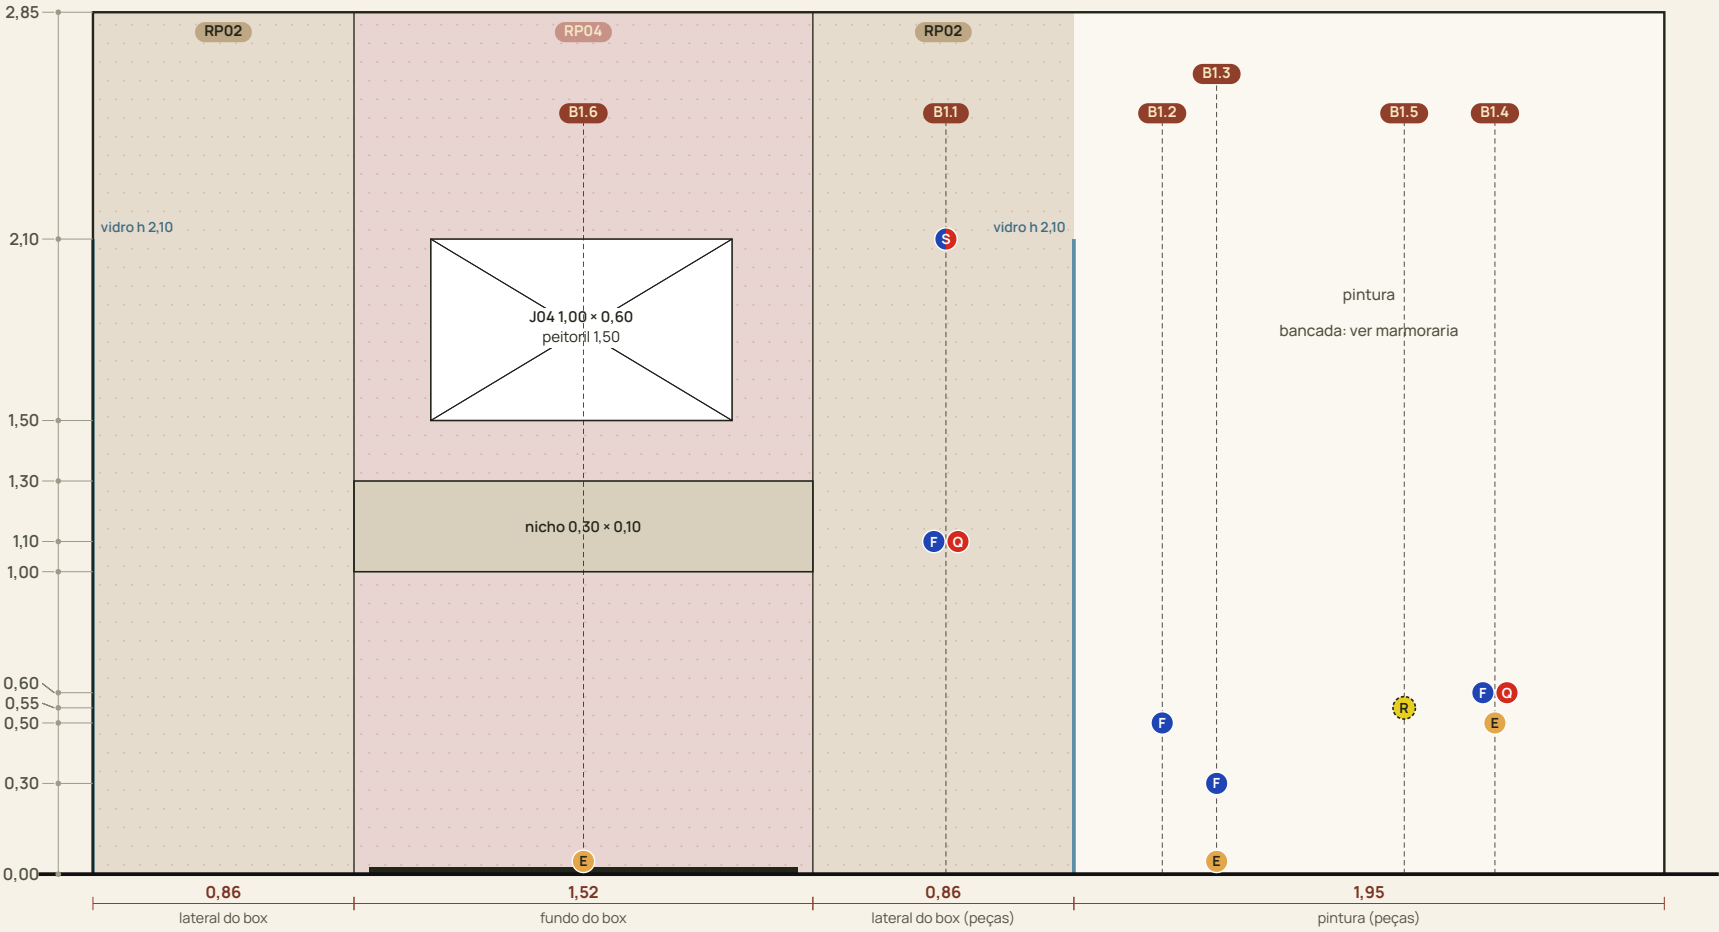

### NOTAS

- Chuveiro

Kit Deca Acqua Plus + misturador de duas alavancas (Level 4900). Registros AF/AQ já executados: afastamento entre eles a medir em obra.

A CONFIRMAR
- Bacia

Roca ONA com caixa acoplada, sem válvula de descarga. AF a 0,30 até conferir na ficha da Roca.

A CONFIRMAR
- RG

Registro geral dentro do armário da bancada, eixo sem cota (marcador tracejado): definir com a marcenaria.

A DEFINIR
- Pontos

Posições e alturas iguais às pranchas de pontos hidráulicos R04 (cotas da planta de 29/09).

DOCUMENTADO

- Vão


Vão do box medido na planta de 29/09 (base das pranchas). O caderno de revestimentos R00 usa a geometria do DWG R01: quantitativos de RP02/RP04 a revisar.

A CONFIRMAR
- Ralo

Desenho indicativo: comprimento, grelha, caimento e desnível do box conforme fabricante e projeto hidrossanitário (folha 08).

A DEFINIR

ESCALA 1 / 25

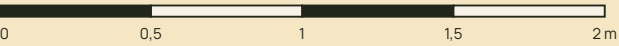

### STATUS

- DOCUMENTADO
- PROPOSTA
- A DEFINIR
- A CONFIRMAR



FOLHA

02/09

TIPO

## Banho Suíte 1

OBRA  
Residência Ivan e Ana Neris · casa unifamiliar térrea

CLIENTES  
Ivan e Ana Neris

ARQ. RESPONSÁVEL  
Lidiane Barbosa  
CAU A290220-6

DATA  
02/10/2026

ENDEREÇO  
Nova Odessa, SP


ARQ. CORRESPONSÁVEL  
Isadora Ferrari  
CAU A263982-8

REVISÃO  
Nº 00

ESCALA  
1/25

CONFERIR AS MEDIDAS NO LOCAL

Escala 1:25 · cotas em metros a partir da face da parede indicada

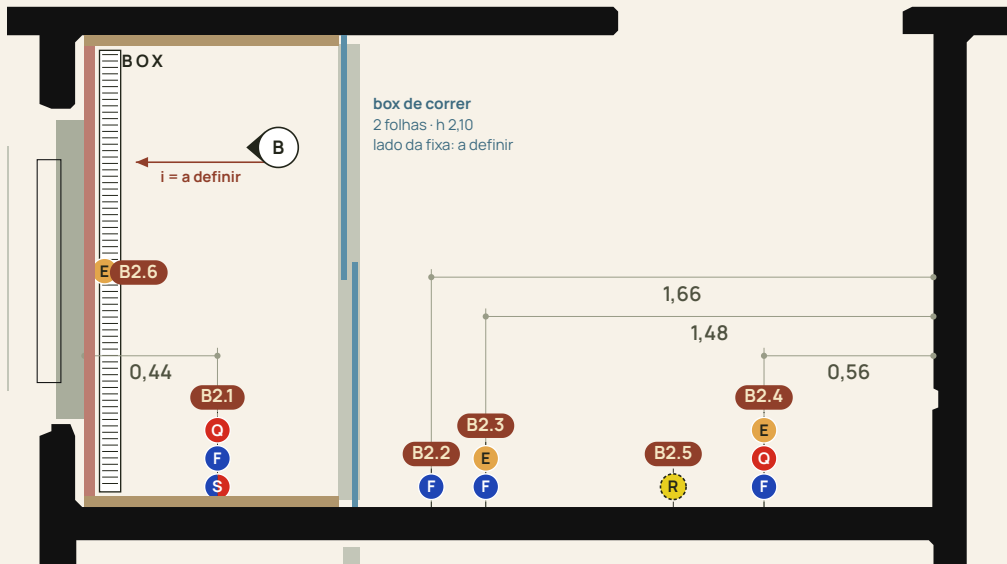

## ALTURA (M) · FONTE

**B2.1 Chuveiro**  
0,44 da parede esquerda  
 2,10 <sup>°</sup>  1,10 <sup>°</sup>  1,10 <sup>°</sup>

**B2.2 Ducha higiênica**  
1,66 da parede direita  
 0,50 <sup>P</sup>

**B2.3 Bacia sanitária**  
1,48 da parede direita  
 0,30 <sup>P</sup>  piso <sup>°</sup>

**B2.4 Cuba - misturador de mesa**  
0,56 da parede direita  
 0,60 <sup>°</sup>  0,60 <sup>D</sup>  0,50 <sup>P</sup>

**B2.5 Registro geral**  
sem cota - dentro do armário  
 0,55 <sup>P</sup>

**B2.6 Ralo linear do box**  
junto à parede do fundo do box - comprimento a definir  
 piso <sup>D</sup>

Fontes: C caderno Hidráulica Rev. 02 · D definição do cliente · P padrão do escritório

|                     |   |
|---------------------|---|
| <b>Box</b>          | Vidro de correr, 2 folhas (1 fixa + 1 de correr), h 2,10 do piso acabado; não vai até o forro.                           |
| <b>Folha fixa</b>   | Lado da folha fixa, ferragem e perfis (lista de louças: previsão cromada).                                               |
| <b>Vão do box</b>   | Fundo 1,56 x lateral 0,84 (planta 29/09). Caderno de revestimentos R00: 1,50 x 0,90.                                     |
| <b>Ralo</b>         | Linear, junto à parede do fundo do box; não há ralo fora do box. Modelo, comprimento e caimento a definir.               |
| <b>Revestimento</b> | Box: laterais RP02 e fundo RP04 até o forro (2,85). Demais paredes em pintura: ducha higiênica, bacia e cuba na pintura. |
| <b>Nicho</b>        | 0,30 x 0,10, base a 1,00, em toda a largura do fundo (caderno R00). Parede de ≈0,15 na planta: conferir a profundidade.  |
| <b>Janela J04</b>   | 1,00 x 0,60, peitoril 1,50 (02/10), no fundo do box.                                                                     |
| <b>Piso</b>         | P01 Santorini OFW NAT 90 x 90 (caderno de pisos R00), inclusive no box.                                                  |
| <b>Bancada</b>      | Bancada da cuba: prancha de marmoraria (a desenvolver).                                                                  |
| <b>Acessórios</b>   | Alturas propostas na folha 08.                                                                                           |

DOCUMENTADO

**A DEFINIR**

A CONFIRMAR

DOCUMENTADO

DOCUMENTADO

CONFIRMAR


DOCUMENTADO

DOCUMENTADO

**A DEFINIR**

## PROPOSTA

Escala 1:25 · vistos de dentro, da esquerda para a direita · alturas do piso acabado

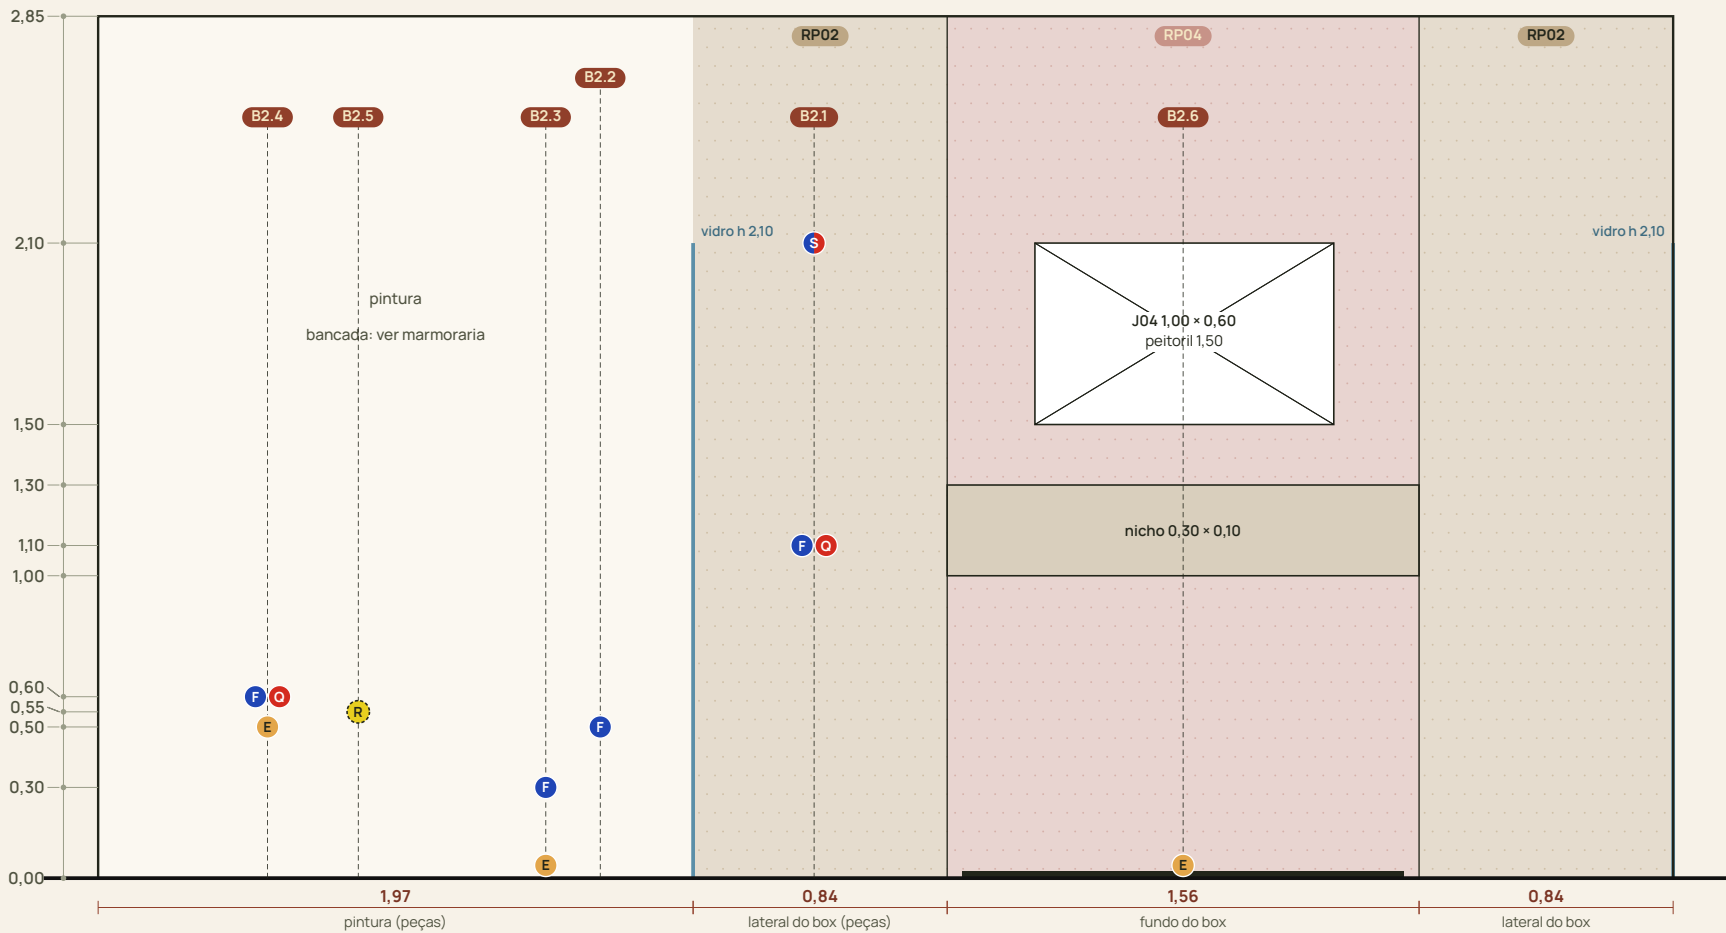

|                 |   |
|-----------------|---|
| <b>Espelho</b>  | Espelhado em relação ao Banho Suíte 1.                                                                                                  |
| <b>Chuveiro</b> | Kit Deca Acqua Plus + misturador de duas alavancas (Level 4900). Registros AF/AQ já executados: afastamento entre eles a medir em obra. |

**Bacia** Roca ONA com caixa acoplada, sem válvula de  
**A CONFIRMAR** descarga. AF a 0,30 até conferir na ficha da Roca.


**RG** Registro geral dentro do armário da bancada, eixo sem cota (marcador tracejado): definir com a marcenaria.

**Pontos** Posições e alturas iguais às pranchas de pontos  
**DOCUMENTADO** hidráulicos R04 (cotas da planta de 29/09).

**Vão** Vão do box medido na planta de 29/09 (base das pranchas). O caderno de revestimentos R00 usa a geometria do DWG R01: quantitativos de RP02/RP04 a revisar.

**Ralo** Desenho indicativo: comprimento, grelha, caimento e desnível do box conforme fabricante e projeto hidrossanitário (folha 08).

ESCALA 1/25

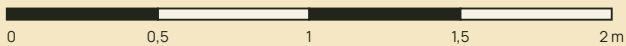

## STATUS

DOCUMENTADO PROPOSTA A DEFINIR A CONFIRMAR



duas  
design  
& arq

duas  
design  
& arq

FOLHA

03/09

## TIPO

## Banho Suíte 2

OBRA  
Residência Ivan e Ana Neris · casa unifamiliar térrea

CLIENTES  
Ivan e Ana Neris

ARQ. RESPONSÁVEL  
Lidiane Barbosa  
CAU A290220-6

DATA  
02/10/2026

ENDEREÇO  
Nova Odessa, SP

ARQ. CORRESPONSÁVEL  
Isadora Ferrari  
CAU A263982-8

REVISÃO      ESCALA  
Nº 00      1/25

**CONFERIR AS MEDIDAS NO LOCAL**

# Banho Suíte Master


## A Planta · pontos e box

Escala 1:25 · cotas em metros a partir da face da parede indicada



## B Box e parede das peças · planificados

Escala 1:25 · vistos de dentro, da esquerda para a direita · alturas do piso acabado

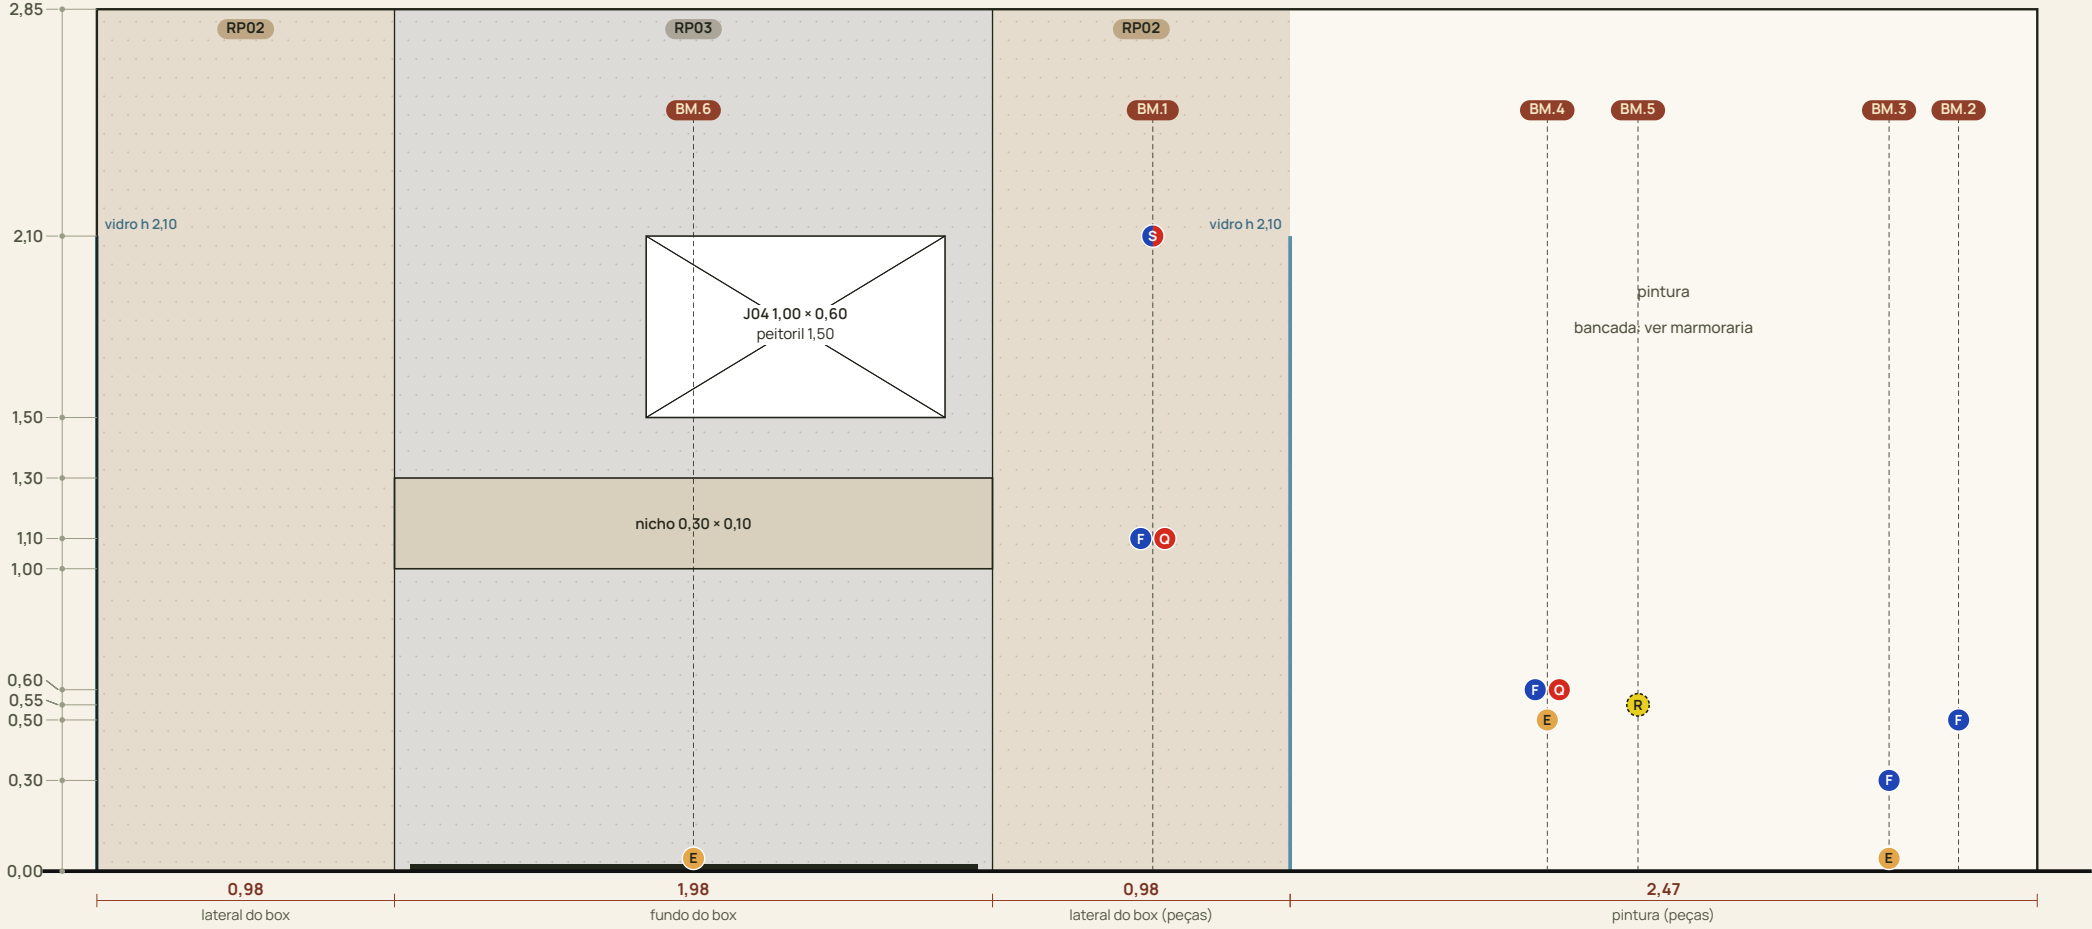

## Pontos e alturas

ALTURA (M) · FONTE

- BM.1

Chuveiro

0,53 da parede inferior

S 2,10<sup>C</sup>

F 1,10<sup>C</sup>

Q 1,10<sup>C</sup>
- BM.2

Ducha higiênica

0,26 da parede superior

F 0,50<sup>P</sup>
- BM.3

Bacia sanitária

0,49 da parede superior

F 0,30<sup>P</sup>

E piso<sup>C</sup>
- BM.4

Cuba · misturador de mesa

1,62 da parede superior

F 0,60<sup>C</sup>

Q 0,60<sup>D</sup>

E 0,50<sup>P</sup>
- BM.5

Registro geral

sem cota · dentro do armário

R 0,55<sup>P</sup>
- BM.6

Ralo linear do box

junto à parede do fundo do box · comprimento a definir

E piso<sup>D</sup>

Fontes: C caderno Hidráulica Rev. 02 · D definição do cliente · P padrão do escritório.

## Elementos

- Box

Vidro de correr, 2 folhas (1 fixa + 1 de correr), h 2,10 do piso acabado; não vai até o forro.

DOCUMENTADO
- Folha fixa

Lado da folha fixa, ferragem e perfis (lista de louças: previsão cromada).

A DEFINIR
- Vão do box

Fundo 1,98 × lateral 0,98 (planta 29/09). Caderno de revestimentos R00: 1,95 × 0,90.

A CONFIRMAR
- Ralo

Linear, junto à parede do fundo do box; não há ralo fora do box. Modelo, comprimento e caimento a definir.

DOCUMENTADO
- Revestimento

Box: laterais RP02 e fundo RP03 até o forro (2,85). Demais paredes em pintura: ducha higiênica, bacia e cuba na pintura.

DOCUMENTADO
- Nicho

0,30 × 0,10, base a 1,00, em toda a largura do fundo (caderno R00). Parede de ≈0,15 na planta: conferir a profundidade.

A CONFIRMAR
- Janela J04

1,00 × 0,60, peitoril 1,50 (02/10), no fundo do box.

DOCUMENTADO
- Piso

P01 Santorini OFW NAT 90 × 90 (caderno de pisos R00), inclusive no box.

DOCUMENTADO
- Bancada

Bancada da cuba: prancha de marmoraria (a desenvolver).

A DEFINIR
- Acessórios

Alturas propostas na folha 08.

PROPOSTA

## NOTAS

- Chuveiro

Kit Deca Acqua Plus + misturador de duas alavancas (Level 4900). Registros AF/AQ já executados: afastamento entre eles a medir em obra.

A CONFIRMAR
- Bacia

Roca ONA com caixa acoplada, sem válvula de descarga. AF a 0,30 até conferir na ficha da Roca.

A CONFIRMAR
- RG

Registro geral dentro do armário da bancada, eixo sem cota (marcador tracejado): definir com a marcenaria.

A DEFINIR
- Pontos

Posições e alturas iguais às pranchas de pontos hidráulicos R04 (cotas da planta de 29/09).

DOCUMENTADO

- Vão

Vão do box medido na planta de 29/09 (base das pranchas). O caderno de revestimentos R00 usa a geometria do DWG R01: quantitativos de RP02/RP03 a revisar.

A CONFIRMAR
- Ralo

Desenho indicativo: comprimento, grelha, caimento e desnível do box conforme fabricante e projeto hidrossanitário (folha 08).

A DEFINIR

ESCALA 1 / 25



## STATUS

- DOCUMENTADO
- PROPOSTA
- A DEFINIR
- A CONFIRMAR



FOLHA

04/09

TIPO

## Banho Suíte Master

OBRA  
Residência Ivan e Ana Neris · casa unifamiliar térrea

CLIENTES  
Ivan e Ana Neris

ARQ. RESPONSÁVEL  
Lidiane Barbosa  
CAU A290220-6

ENDEREÇO  
Nova Odessa, SP

ARQ. CORRESPONSÁVEL  
Isadora Ferrari  
CAU A263982-8

DATA  
02/10/2026

REVISÃO  
Nº 00


ESCALA  
1/25

CONFERIR AS MEDIDAS NO LOCAL

# Banho 4

## A Planta · pontos e box

Escala 1:25 · cotas em metros a partir da face da parede indicada

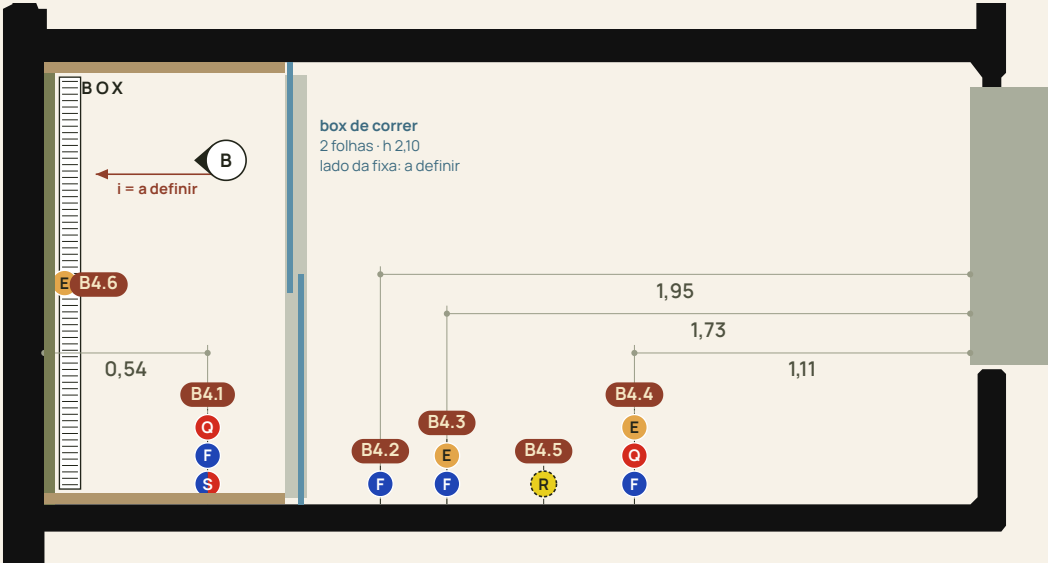

## Pontos e alturas

ALTURA (M) · FONTE

- B4.1** Chuveiro  
0,54 da parede esquerda  
S 2,10<sup>C</sup> F 1,10<sup>C</sup> Q 1,10<sup>C</sup>
- B4.2** Ducha higiênica  
1,95 da parede direita  
F 0,50<sup>P</sup>
- B4.3** Bacia sanitária  
1,73 da parede direita  
F 0,30<sup>P</sup> E piso<sup>C</sup>
- B4.4** Cuba de sobrepor · misturador bica alta  
1,11 da parede direita  
F 0,60<sup>D</sup> Q 0,60<sup>D</sup> E 0,50<sup>P</sup>
- B4.5** Registro geral  
sem cota · dentro do armário  
R 0,55<sup>C</sup>
- B4.6** Ralo linear do box  
junto à parede do fundo do box · comprimento a definir  
E piso<sup>D</sup>


Fontes: C caderno Hidráulica Rev. 02 · D definição do cliente · P padrão do escritório.

## Elementos

|              |   |             |
|--------------|---|-------------|
| Box          | Vidro de correr, 2 folhas (1 fixa + 1 de correr), h 2,10 do piso acabado; não vai até o forro.                           | DOCUMENTADO |
| Folha fixa   | Lado da folha fixa, ferragem e perfis (lista de louças: previsão cromada).                                               | A DEFINIR   |
| Vão do box   | Fundo 1,46 × lateral 0,80 (planta 29/09). Caderno de revestimentos R00: 1,40 × 0,90.                                     | A CONFIRMAR |
| Ralo         | Linear, junto à parede do fundo do box; não há ralo fora do box. Modelo, comprimento e caimento a definir.               | DOCUMENTADO |
| Revestimento | Box: laterais RP02 e fundo RP05 até o forro (2,85). Demais paredes em pintura: ducha higiênica, bacia e cuba na pintura. | DOCUMENTADO |
| Nicho        | 0,30 × 0,10, base a 1,00, em toda a largura do fundo (caderno R00). Parede de ≈0,15 na planta: conferir a profundidade.  | A CONFIRMAR |
| Piso         | P01 Santorini OFW NAT 90 × 90 (caderno de pisos R00), inclusive no box.                                                  | DOCUMENTADO |
| Bancada      | Bancada da cuba: prancha de marmoraria (a desenvolver).                                                                  | A DEFINIR   |
| Acessórios   | Alturas propostas na folha 08.                                                                                           | PROPOSTA    |

## B Box e parede das peças · planejados

Escala 1:25 · vistos de dentro, da esquerda para a direita · alturas do piso acabado

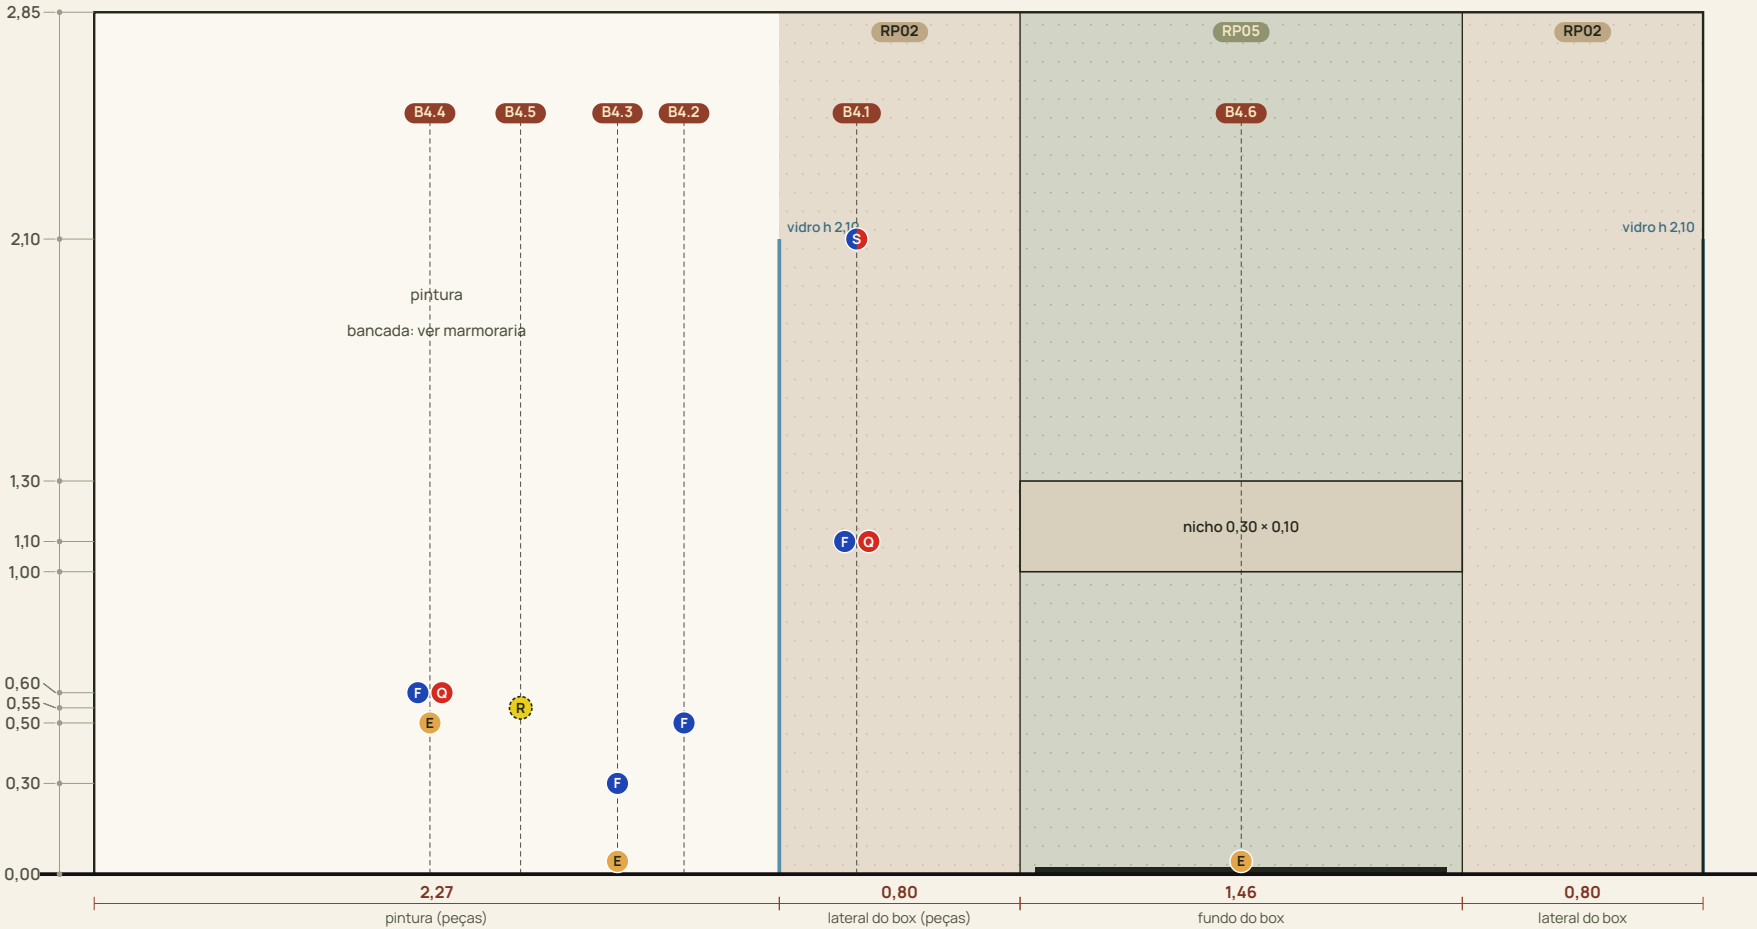

### NOTAS

**Chuveiro** Kit Deca Acqua Plus + misturador de duas alavancas (Level 4900). Registros AF/AQ já executados: afastamento entre eles a medir em obra.

**Bacia** Roca ONA com caixa acoplada, sem válvula de descarga. AF a 0,30 até conferir na ficha da Roca.


**RG** Registro geral dentro do armário da bancada, eixo sem cota (marcador tracejado): definir com a marcenaria.

**Pontos** Posições e alturas iguais às pranchas de pontos hidráulicos R04 (cotas da planta de 29/09).

**Vão** Vão do box medido na planta de 29/09 (base das pranchas). O caderno de revestimentos R00 usa a geometria do DWG R01: quantitativos de RP02/RP05 a revisar.

**Ralo** Desenho indicativo: comprimento, grelha, caimento e desnível do box conforme fabricante e projeto hidrossanitário (folha 08).

ESCALA 1/25

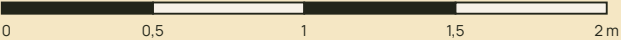

### STATUS

DOCUMENTADO PROPOSTA A DEFINIR A CONFIRMAR

DUAS duas design & arq

FOLHA

05/09

TIPO

## Banho 4

**OBRA** Residência Ivan e Ana Neris · casa unifamiliar térrea

**CLIENTES** Ivan e Ana Neris  
**ARQ. RESPONSÁVEL** Lidiane Barbosa  
CAU A290220-6

**DATA** 02/10/2026

**ENDEREÇO** Nova Odessa, SP

**ARQ. CORRESPONSÁVEL** Isadora Ferrari  
CAU A263982-8

**REVISÃO** N° 00


**ESCALA** 1/25

CONFERIR AS MEDIDAS NO LOCAL

# Cozinha

## A Planta · pontos

Escala 1:50 · cotas em metros a partir da face da parede indicada

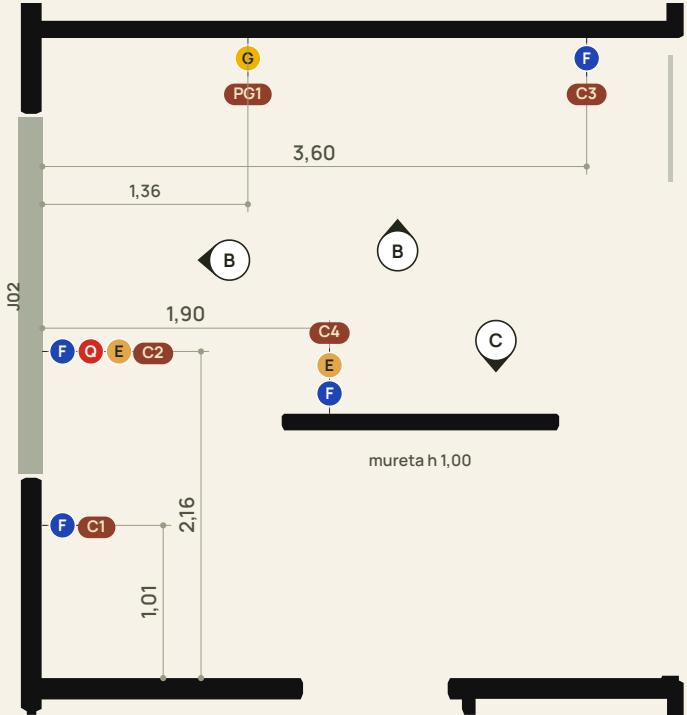

## Pontos e alturas

ALTURA (M) · FONTE

- C1** Filtro  
1,01 da parede inferior  
F 1,00<sup>C</sup>
- C2** Cuba da pia · misturador monocomando  
2,16 da parede inferior  
F 0,50<sup>D</sup> D 0,50<sup>C</sup> E 0,35<sup>C</sup>
- C3** Geladeira  
3,60 da parede da janela (esquerda)  
F 1,25<sup>C</sup>
- C4** Lava-louças · face da mureta  
1,90 da parede da janela · na face norte da mureta do balcão (≈0,32 da ponta)  
F 0,60<sup>C</sup> E 0,50<sup>P</sup>
- PG1** Fogão de piso 5 bocas  
1,36 da parede da janela · parede superior da cozinha  
G 0,60<sup>D</sup>

Fontes: C caderno Hidráulica Rev. 02 · D definição do cliente · P padrão do escritório.

## Elementos

- Revestimento** RP07 cerâmica simples (fundo da marcenaria) na parede da janela e na parede superior, até o forro 2,85 (caderno R00).
- J02** 2,35 × 0,45, peitoril 1,10 (caderno de revestimentos R00) : conferir no quadro de esquadrias.
- Mureta** Planta 29/09: 1,83 × 0,11, h 1,00. Caderno R00: 1,90 × 0,15. RP02 nas faces norte e sul.
- Parede sup.** Planta 29/09: 4,14 até o vidro; caderno R00: 4,25.
- Lava-louças** Água e esgoto pela face norte da mureta; ponto de água sem torneira própria (02/10).
- Gás** PG1 fogão: ver prancha de pontos de gás R02.
- Piso** P01 Santorini OFW NAT 90 × 90 (caderno de pisos R00).
- Bancada** Bancadas e marcenaria: projeto de marcenaria e marmoraria.

DOCUMENTADO

A CONFIRMAR

A CONFIRMAR

A CONFIRMAR

DOCUMENTADO


DOCUMENTADO

DOCUMENTADO

A DEFINIR


## B Parede da janela e parede superior · planificadas

Escala 1:50 · vistas de dentro · alturas do piso acabado

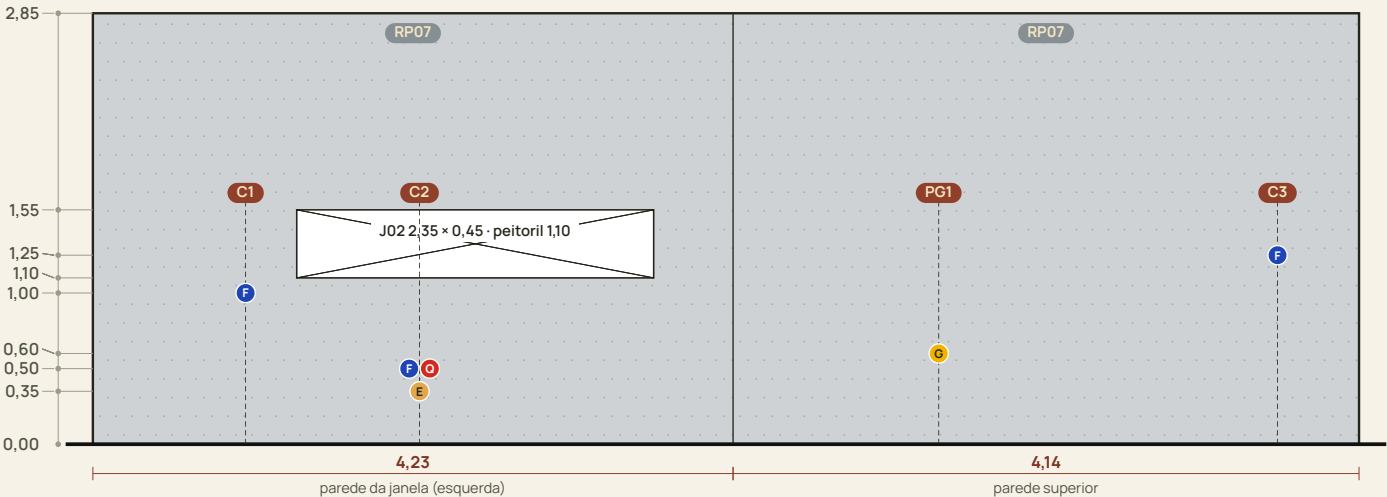

## C Mureta do balcão · face voltada para o fogão

Escala 1:25 · vista do lado do fogão e da geladeira (face norte da planta)

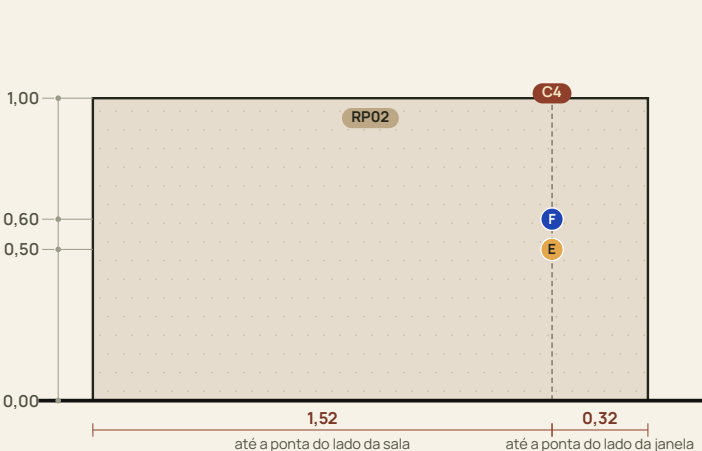

C4 cotado na planta a 1,90 da parede da janela (eixo) ; fica a 0,32 da ponta da mureta do lado da janela. Tomada da face do balcão afastada no mínimo 0,30 m dos pontos (Tomadas R05, item 13.5).

Topo e cabeceiras da mureta: acabamento a definir com a marmoraria.

### NOTAS

**C2** Cuba Deca Suprema 75 × 40 inox com misturador monocomando 2275.INX (AF/AQ). Registro 4900.INX105.PQ sob a bancada.

**C1** Filtro Purific Camadas 10 (torneira própria do fabricante), ponto a 1,00.


**C4** Lava-louças: ESG a 0,50 (padrão do escritório) e AF a 0,60 (caderno), na face da mureta.

**Elevação** Planificada: parede da janela vista de dentro (esquerda = parede inferior) e, em seguida, parede superior.

**Geometria** Mureta e paredes medidas na planta de 29/09; o caderno de revestimentos R00 usa a geometria do DWG R01.

A CONFIRMAR

ESCALA 1 / 50

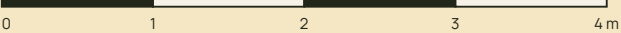

### STATUS

DOCUMENTADO

PROPOSTA

A DEFINIR

A CONFIRMAR

duas design & arq

FOLHA

06/09

TIPO

Cozinha

**OBRA**  
Residência Ivan e Ana Neris · casa unifamiliar térrea

**CLIENTES**  
Ivan e Ana Neris

**ARQ. RESPONSÁVEL**  
Lidiane Barbosa  
CAU A290220-6

**DATA**  
02/10/2026

**ENDEREÇO**  
Nova Odessa, SP



**ARQ. CORRESPONSÁVEL**  
Isadora Ferrari  
CAU A263982-8

**REVISÃO**  
Nº 00

**ESCALA**  
1/50 e 1/25

CONFERIR AS MEDIDAS NO LOCAL

# Gourmet e A.S.

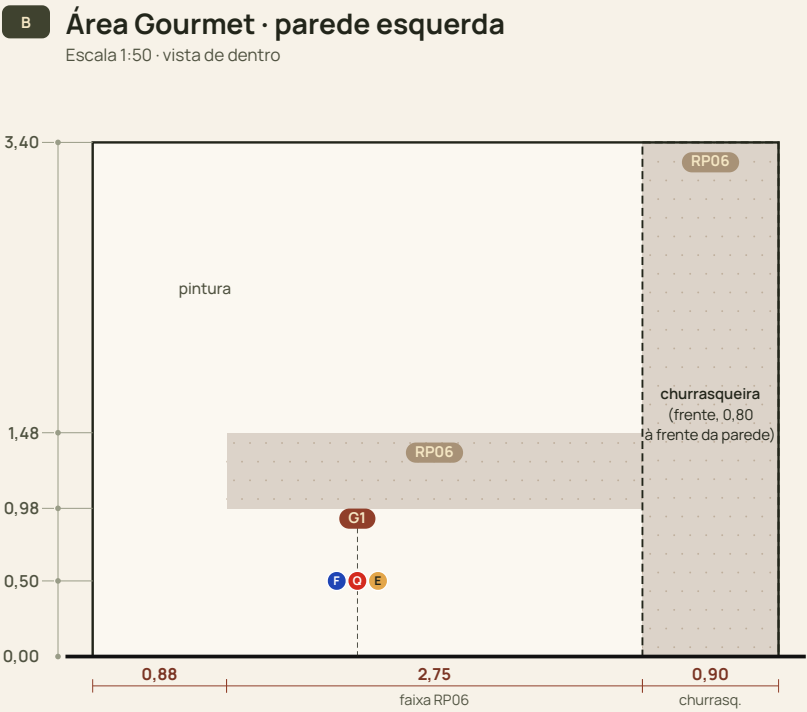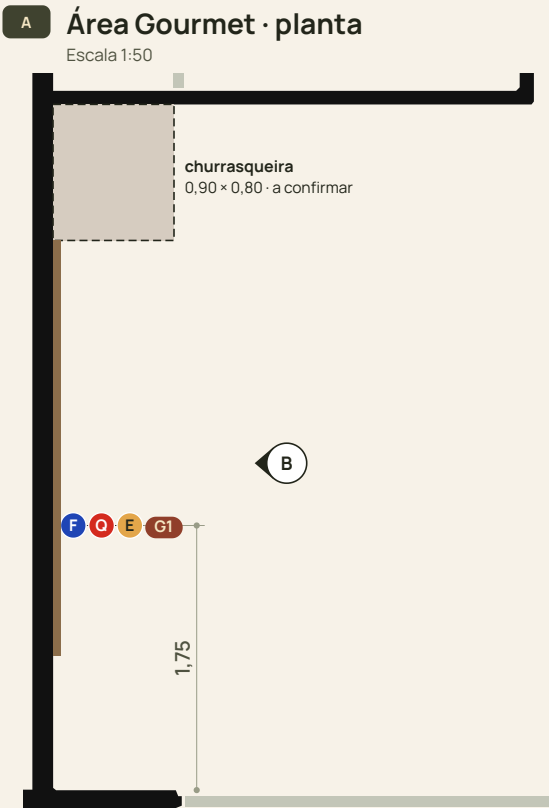

Pontos e alturas

ALTURA (M) · FONTE

G1

Cuba · misturador de mesa

1,75 da parede inferior (2,80 até a superior, conforme caderno)

F

0,50<sup>D</sup>

Q

0,50<sup>C</sup>

E

0,50<sup>D</sup>

Fontes: C caderno Hidráulica Rev. 02 · D definição do cliente · P padrão do escritório.

Elementos

Faixa RP06

Travertino Rock Face 0,98–1,48, 2,75 junto à churrasqueira.

DOCUMENTADO

Churrasq.

Frente 0,90 e lateral 0,80, RP06 (caderno R00). Posição a confirmar.

A CONFIRMAR

Boca

0,80 × 0,80: altura a confirmar.

A CONFIRMAR

Pé-direito

3,40 (caderno R00): sem forro de gesso.

DOCUMENTADO

Piso



P02 Santorini SGR HARD.

DOCUMENTADO

Bancada

Marmoraria.

A DEFINIR

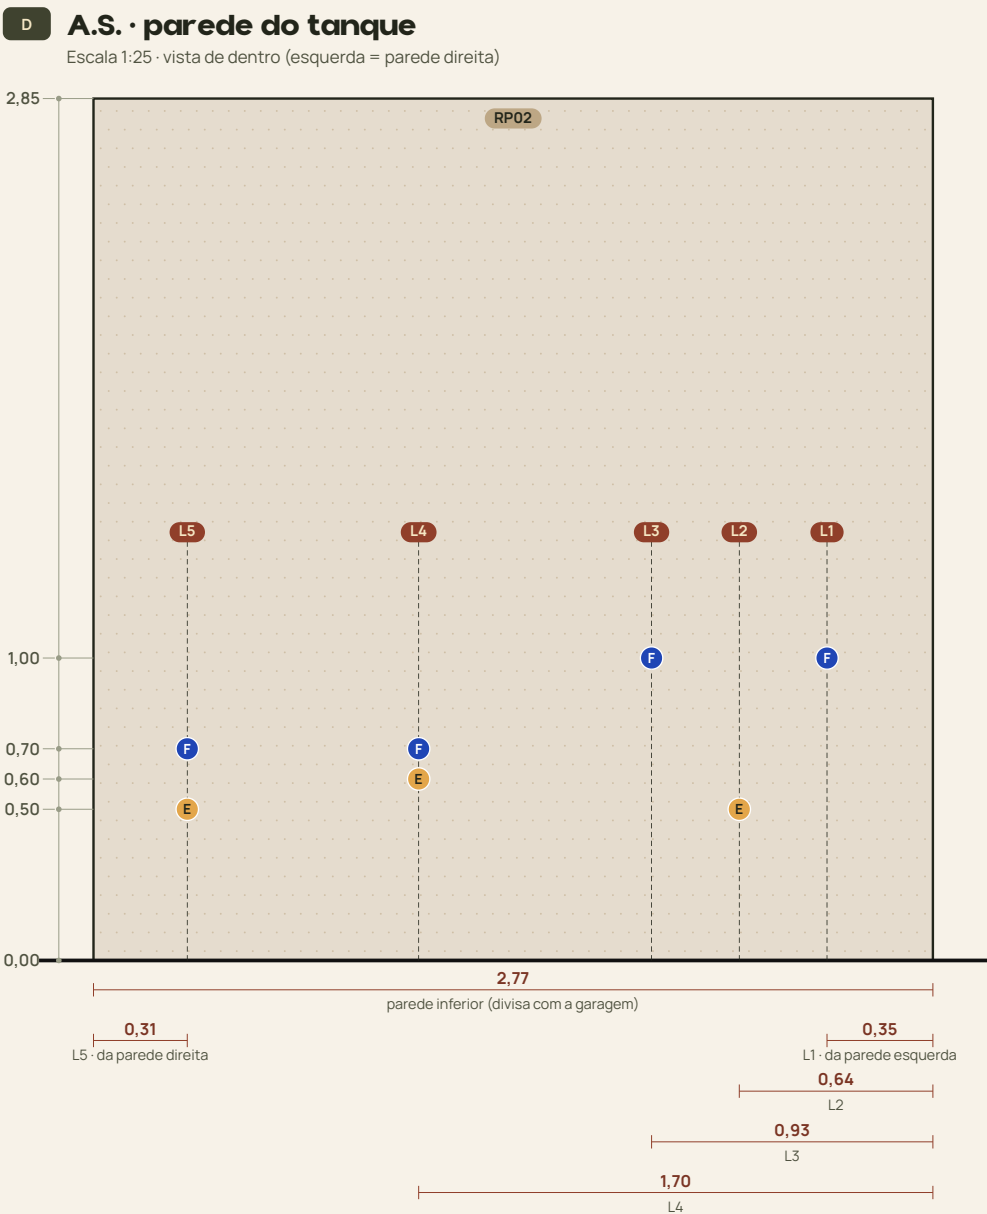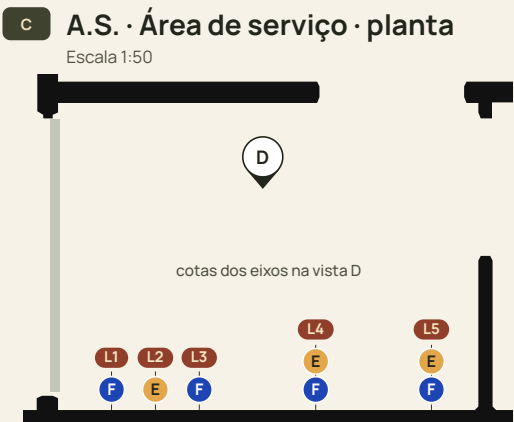

Pontos e alturas

ALTURA (M) · FONTE

L1

Torneira de parede · tanque

0,35 da parede esquerda

F

1,00<sup>P</sup>

L2

Esgoto do tanque

0,64 da parede esquerda (centro do tanque, meio das torneiras)

E

0,50<sup>P</sup>

L3

Torneira de parede · tanque

0,93 da parede esquerda

F

1,00<sup>P</sup>

L4

Máquina de lavar roupas

1,70 da parede esquerda

F

0,70<sup>C</sup>

E

0,60<sup>P</sup>

L5

Tanquinho

0,31 da parede direita

F

0,70<sup>C</sup>

E

0,50<sup>P</sup>

Fontes: C caderno Hidráulica Rev. 02 · D definição do cliente · P padrão do escritório.

NOTAS

Gourmet

Cuba Deca Suprema 50 × 40 inox; misturador de mesa AF/AQ (proposta Deca Flex Plus 2250.C, folha 09).

PROPOSTA

Churrasq.

Posição lida no caderno de revestimentos R00 (E11/E12): no canto junto ao Banho 4. Não consta na planta de 29/09.

A CONFIRMAR

A.S.

Tanque I.Corso 60 × 57; L1 e L3 ficam, uma será vedada depois. L2 só com o esgoto do tanque (R04).

DOCUMENTADO

A.S.

RP02 em toda a parede inferior até o forro 2,85 (caderno R00). Piso P01.

DOCUMENTADO

Ralos

Ralo de piso na A.S. e na Área Gourmet: não indicado nos arquivos nem solicitado (02/10).

Varal

Varal de parede Varal Mágico 120 cm: posição a definir (parede com estrutura para o peso).

A DEFINIR

ESCALA 1/25 (1/50: × 2)

00,511,52m

STATUS

DOCUMENTADO

PROPOSTA

A DEFINIR

A CONFIRMAR

DUAS

duas design & arq

FOLHA

07/09

TIPO

Gourmet e A.S.

OBRA

Residência Ivan e Ana Neris · casa unifamiliar térrea

CLIENTES

Ivan e Ana Neris

ENDEREÇO

Nova Odessa, SP

ARQ. RESPONSÁVEL

Lidiane Barbosa  
CAU A290220-6

ARQ. CORRESPONSÁVEL

Isadora Ferrari  
CAU A263982-8

DATA

02/10/2026

REVISÃO

Nº 00

ESCALA


1/50 e 1/25

CONFERIR AS MEDIDAS NO LOCAL

# Detalhes


## A Ralo linear · planta esquemática

Sem escala · vale para os 4 boxes

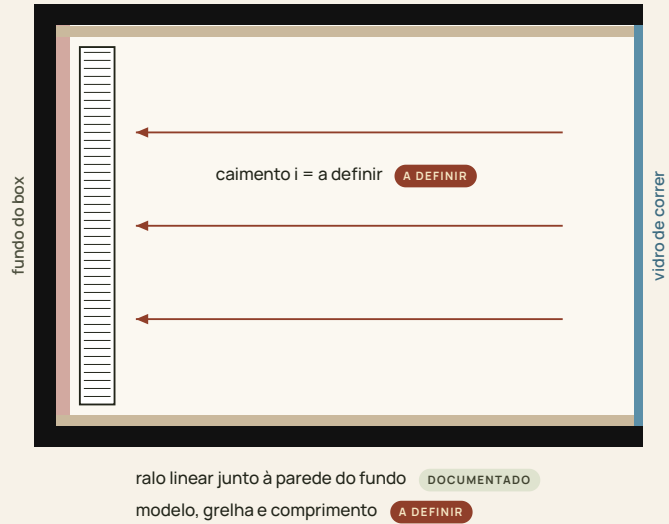


## B Ralo linear · corte esquemático

Sem escala · sem dimensionamento

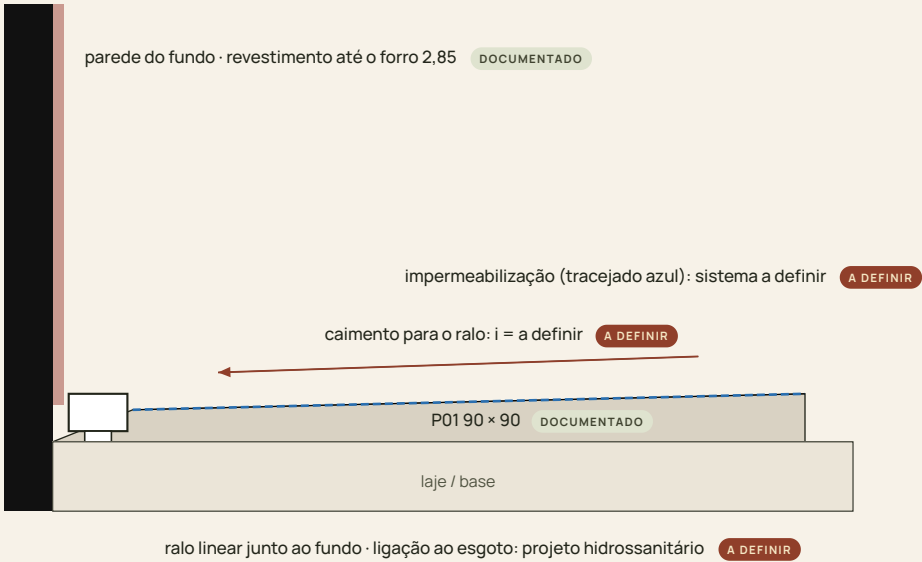

## C Box de correr · planta e vista esquemáticas

Sem escala · vão de cada banho na tabela

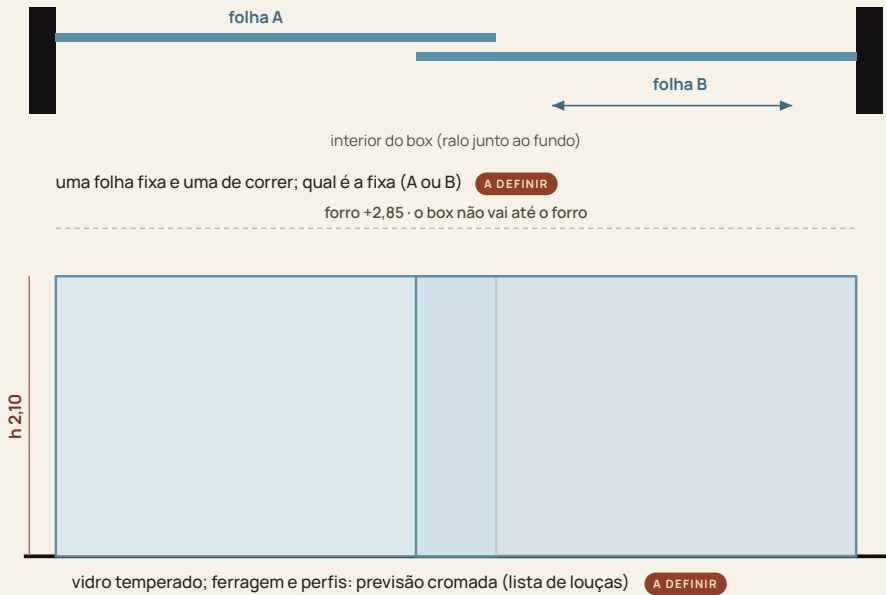


### Vãos dos boxes

| BANHO              | VÃO (FUNDO) | LATERAL | CADERNO R00 |
|--------------------|-------------|---------|-------------|
| Banho Suite 1      | 1,52        | 0,86    | 1,50 × 0,90 |
| Banho Suite 2      | 1,56        | 0,84    | 1,50 × 0,90 |
| Banho Suite Master | 1,98        | 0,98    | 1,95 × 0,90 |
| Banho 4            | 1,46        | 0,80    | 1,40 × 0,90 |

Planta de 29/09 (base das pranchas), medido entre as faces das paredes. Medir o vão executado antes de encomendar o vidro.


## D Nicho · corte

Escala 1:10 · caderno de revestimentos R00

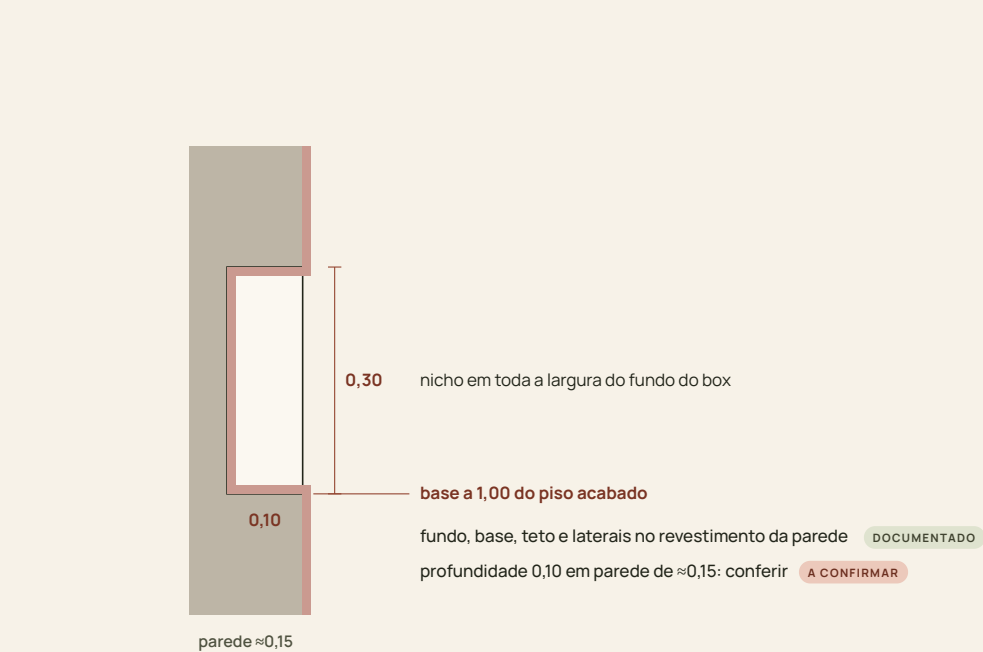

## E Acessórios · alturas propostas

Eixo da peça a partir do piso acabado · linha Deca You

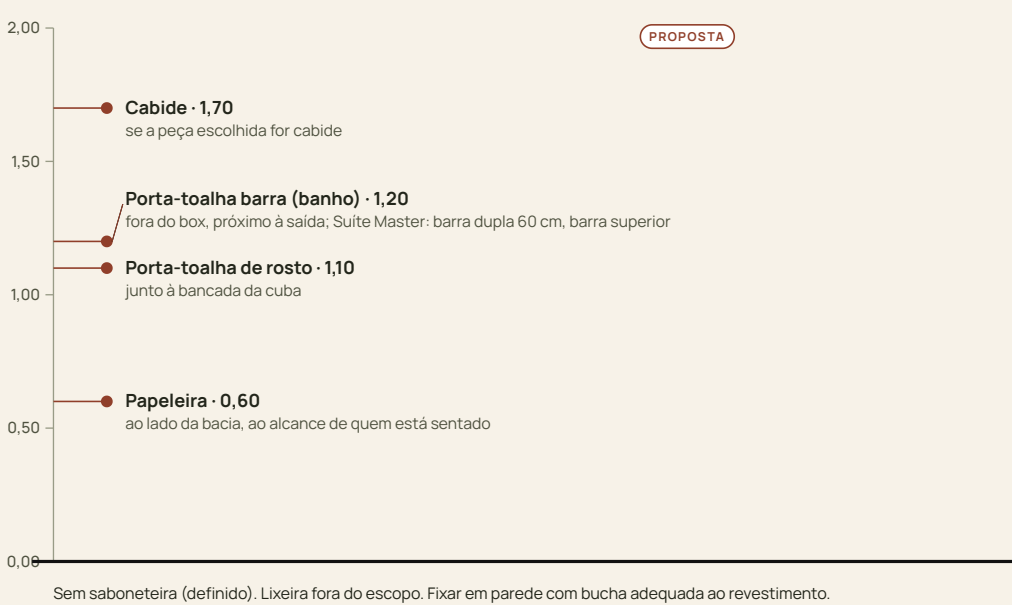

Sem saboneteira (definido). Lixeira fora do escopo. Fixar em parede com bucha adequada ao revestimento.

### NOTAS

**Impermeab.** Sistema, extensão e altura de subida nas paredes do box e no piso dos banhos e da A.S.: a definir pelo responsável técnico (NBR 9575 e NBR 9574).

**Desnível** Desnível entre o piso do box e o do banho e soleira do box: a definir com o ralo escolhido.

**Ralo** Linear, junto ao fundo do box, nos 4 banhos (02/10). Não há ralo fora do box.

**Box** Correr, 2 folhas (1 fixa + 1 de correr), h 2,10, não vai até o forro (02/10).

**Acessórios** Alturas propostas pelo escritório (liberado pelo cliente em 02/10): confirmar com as peças Deca You.

### Escopo

Desenhos esquemáticos de localização: não substituem o projeto hidrossanitário nem o de impermeabilização.

### STATUS

DOCUMENTADO

PROPOSTA

A DEFINIR

A CONFIRMAR

duas design & arq

FOLHA

08/09

TIPO

## Detalhes

**OBRA**  
Residência Ivan e Ana Neris · casa unifamiliar térrea

**CLIENTES**  
Ivan e Ana Neris

**ARQ. RESPONSÁVEL**  
Lidiane Barbosa  
CAU A290220-6

**DATA**  
02/10/2026

**ENDEREÇO**  
Nova Odessa, SP

**ARQ. CORRESPONSÁVEL**  
Isadora Ferrari  
CAU A263982-8

**REVISÃO**  
Nº 00

**ESCALA**  
indicadas

CONFERIR AS MEDIDAS NO LOCAL

# Louças e metais

Lista técnica de compras de 25/09/2026 atualizada com as decisões de 02/10/2026. O código vale pela referência de cada linha; confirmar disponibilidade e acabamento na loja.

| PONTO                                     | ITEM                                                                      | MARCA · LINHA        | REFERÊNCIA                  | ACABAMENTO         | QTD.    | STATUS      |
|-------------------------------------------|---------------------------------------------------------------------------|----------------------|-----------------------------|--------------------|---------|-------------|
| Banhos Suíte 1 e Suíte 2 · por banho (×2) |                                                                           |                      |                             |                    |         |             |
| B1.1/B2.1                                 | Kit chuveiro de parede com desviador e ducha manual                       | Deca · Acqua Plus    | —                           | Cromado            | 1       | DOCUMENTADO |
| B1.1/B2.1                                 | Acabamento de registro · misturador de duas alavancas                     | Deca · Level         | 4900.C26.GD                 | Cromado            | 1 conj. | DOCUMENTADO |
| B1.2/B2.2                                 | Ducha higiênica com registro e derivação                                  | Deca · Level         | 1984.C26.ACT                | Cromado            | 1       | DOCUMENTADO |
| B1.3/B2.3                                 | Bacia com caixa acoplada + assento original                               | Roca · ONA           | —                           | Padrão             | 1       | DOCUMENTADO |
| B1.4/B2.4                                 | Cuba de embutir retangular 50 × 40                                        | Deca                 | —                           | Branca             | 1       | DOCUMENTADO |
| B1.4/B2.4                                 | Misturador de mesa bica baixa (AF/AQ) · substitui torneira 1193.C26       | Deca · Level         | 2875.C26                    | Cromado            | 1       | PROPOSTA    |
| B1.4/B2.4                                 | Válvula de escoamento click · engates flexíveis (2 por misturador)        | Deca                 | 1601.C.CLI · 4607.C.030/040 | Cromado            | 1 + 2   | PROPOSTA    |
| —                                         | Porta-toalha barra simples · porta-toalha de rosto/cabide · papeleira     | Deca · You           | —                           | Cromado            | 1 cada  | DOCUMENTADO |
| Banho Suíte Master                        |                                                                           |                      |                             |                    |         |             |
| BM.1                                      | Kit chuveiro Acqua Plus + acabamento misturador duas alavancas            | Deca                 | 4900.C26.GD                 | Cromado            | 1       | DOCUMENTADO |
| BM.2                                      | Ducha higiênica com registro e derivação                                  | Deca · Level         | 1984.C26.ACT                | Cromado            | 1       | DOCUMENTADO |
| BM.3                                      | Bacia com caixa acoplada + assento original                               | Roca · ONA           | —                           | Padrão             | 1       | DOCUMENTADO |
| BM.4                                      | Cuba de embutir 50 × 40 (1 cuba, 02/10)                                   | Deca                 | —                           | Branca             | 1       | DOCUMENTADO |
| BM.4                                      | Misturador de mesa bica baixa (AF/AQ) · substitui 1193.C26                | Deca · Level         | 2875.C26                    | Cromado            | 1       | PROPOSTA    |
| BM.4                                      | Válvula click · engates flexíveis                                         | Deca                 | 1601.C.CLI · 4607.C.030/040 | Cromado            | 1 + 2   | PROPOSTA    |
| —                                         | Porta-toalha barra dupla 60 cm                                            | Deca · You           | 2042.C104.060               | Cromado            | 1       | DOCUMENTADO |
| —                                         | Porta-toalha de rosto/cabide · papeleira                                  | Deca · You           | —                           | Cromado            | 1 cada  | DOCUMENTADO |
| Banho 4                                   |                                                                           |                      |                             |                    |         |             |
| B4.1                                      | Kit chuveiro Acqua Plus + acabamento misturador duas alavancas            | Deca                 | 4900.C26.GD                 | Cromado            | 1       | DOCUMENTADO |
| B4.2                                      | Ducha higiênica com registro e derivação                                  | Deca · Level         | 1984.C26.ACT                | Cromado            | 1       | DOCUMENTADO |
| B4.3                                      | Bacia com caixa acoplada + assento original                               | Roca · ONA           | —                           | Padrão             | 1       | DOCUMENTADO |
| B4.4                                      | Cuba de apoio/sobrepôr retangular (cor verde fosco a confirmar na loja)   | Deca · Slim          | —                           | Verde fosco        | 1       | A CONFIRMAR |
| B4.4                                      | Misturador de mesa bica alta (AF/AQ) · substitui Tube 1198.GF.TUB.MT      | Deca · Unic          | 2885.GF90.MT                | Dark Antracite     | 1       | PROPOSTA    |
| B4.4                                      | Válvula click (cromada, decisão do cliente) · engates flexíveis           | Deca                 | 1601.C.CLI · 4607.C.030/040 | Cromado            | 1 + 2   | PROPOSTA    |
| —                                         | Porta-toalha barra simples · rosto/cabide · papeleira                     | Deca · You           | —                           | Cromado            | 1 cada  | DOCUMENTADO |
| Cozinha                                   |                                                                           |                      |                             |                    |         |             |
| C2                                        | Cuba de embutir 75 × 40 inox                                              | Deca · Suprema       | CC67075INX                  | Inox               | 1       | DOCUMENTADO |
| C2                                        | Misturador monocomando de mesa                                            | Deca                 | 2275.INX                    | Inox               | 1       | DOCUMENTADO |
| C2                                        | Registro de gaveta, acabamento quadrado (sob a bancada)                   | Deca                 | 4900.INX105.PQ              | Inox               | 1       | DOCUMENTADO |
| C2                                        | Sifão articulado 1½" + engates (referência de mercado)                    | Deca                 | 1682.C.112                  | Cromado/inox       | 1 kit   | A CONFIRMAR |
| C1                                        | Filtro/purificador com torneira própria                                   | Purific · Camadas 10 | —                           | a escolher         | 1       | DOCUMENTADO |
| C4                                        | Lava-louças: só ponto de água e esgoto (sem torneira independente)        | —                    | —                           | —                  | —       | DOCUMENTADO |
| Área Gourmet                              |                                                                           |                      |                             |                    |         |             |
| G1                                        | Cuba de embutir 50 × 40 inox                                              | Deca · Suprema       | CC66050INX                  | Inox               | 1       | DOCUMENTADO |
| G1                                        | Misturador de mesa bica móvel (AF/AQ) · substitui torneira 1167.C21       | Deca · Flex Plus     | 2250.C                      | Cromado            | 1       | PROPOSTA    |
| G1                                        | Registro de gaveta, acabamento                                            | Deca · Level         | 4900.C26.GD                 | Cromado            | 1       | DOCUMENTADO |
| G1                                        | Sifão articulado 1½" + engates (referência de mercado)                    | Deca                 | 1682.C.112                  | Cromado/inox       | 1 kit   | A CONFIRMAR |
| A.S. · Área de serviço                    |                                                                           |                      |                             |                    |         |             |
| L2                                        | Tanque moldado 60 × 57, 39 L                                              | I.Corso · Premium    | —                           | Branco             | 1       | DOCUMENTADO |
| L1-L3                                     | Torneira de parede bica longa (uma das duas será vedada)                  | Deca · Link          | 1178.C.LNK                  | Cromado            | 1       | DOCUMENTADO |
| L4                                        | Registro/torneira da máquina de lavar                                     | —                    | —                           | Cromado            | 1       | A DEFINIR   |
| —                                         | Varal de parede sanfonado 7 varetas, 120 cm                               | Varal Mágico         | —                           | Alumínio branco    | 1       | DOCUMENTADO |
| Áreas externas e boxes                    |                                                                           |                      |                             |                    |         |             |
| X1-X2                                     | Kit chuveirão de parede, só água fria, com acabamento de registro         | Deca + kit           | a fechar                    | Cromado            | 1       | A CONFIRMAR |
| X3-X4                                     | Torneira de jardim com adaptador para mangueira (lista: qtd 1; pontos: 2) | Deca · Izy           | 1153.C37                    | Cromado            | 2       | A CONFIRMAR |
| Boxes                                     | Vidro temperado de correr e ferragem dos 4 boxes (folha 08)               | —                    | —                           | Cromado (previsão) | 4       | A DEFINIR   |

## NOTAS

- Misturadores**

PROPOSTA

Lavatórios e Área Gourmet passam a ter AF e AQ (02/10): as torneiras só de água fria da lista foram trocadas por misturadores da mesma família (proposta do escritório). Confirmar preço e prazo.
- Engates**

PROPOSTA

Cada misturador de mesa usa 2 engates flexíveis (AF e AQ): quantidade dobrada em relação à lista.
- Banho 4**

PROPOSTA

Unic 2885.GF90.MT em Dark Antracite (alternativa: Duna Clássica 1877.GF64.MT). Válvula click cromada.
- Bacias**

A CONFIRMAR

Roca ONA com caixa acoplada: dispensa válvula de descarga. Ponto AF a 0,30 a conferir na ficha técnica.

- Pendentes**

A DEFINIR

Sifões compatíveis com as cubas Suprema, kit da ducha externa e registro da máquina: lista de controle de 25/09.
- Quantidade**

A CONFIRMAR

Torneira de jardim: a lista prevê 1, mas há 2 pontos (X3 e X4, mantidos em 02/10).

## STATUS

- DOCUMENTADO
- PROPOSTA
- A DEFINIR
- A CONFIRMAR



FOLHA

09/09

TIPO

## Louças e metais

OBRA  
Residência Ivan e Ana Neris · casa unifamiliar térrea

CLIENTES  
Ivan e Ana Neris

ARQ. RESPONSÁVEL  
Lidiane Barbosa  
CAU A290220-6

ENDEREÇO  
Nova Odessa, SP

ARQ. CORRESPONSÁVEL  
Isadora Ferrari  
CAU A263982-8

DATA  
02/10/2026

REVISÃO  
Nº 00

ESCALA  
sem escala

CONFERIR AS MEDIDAS NO LOCAL