



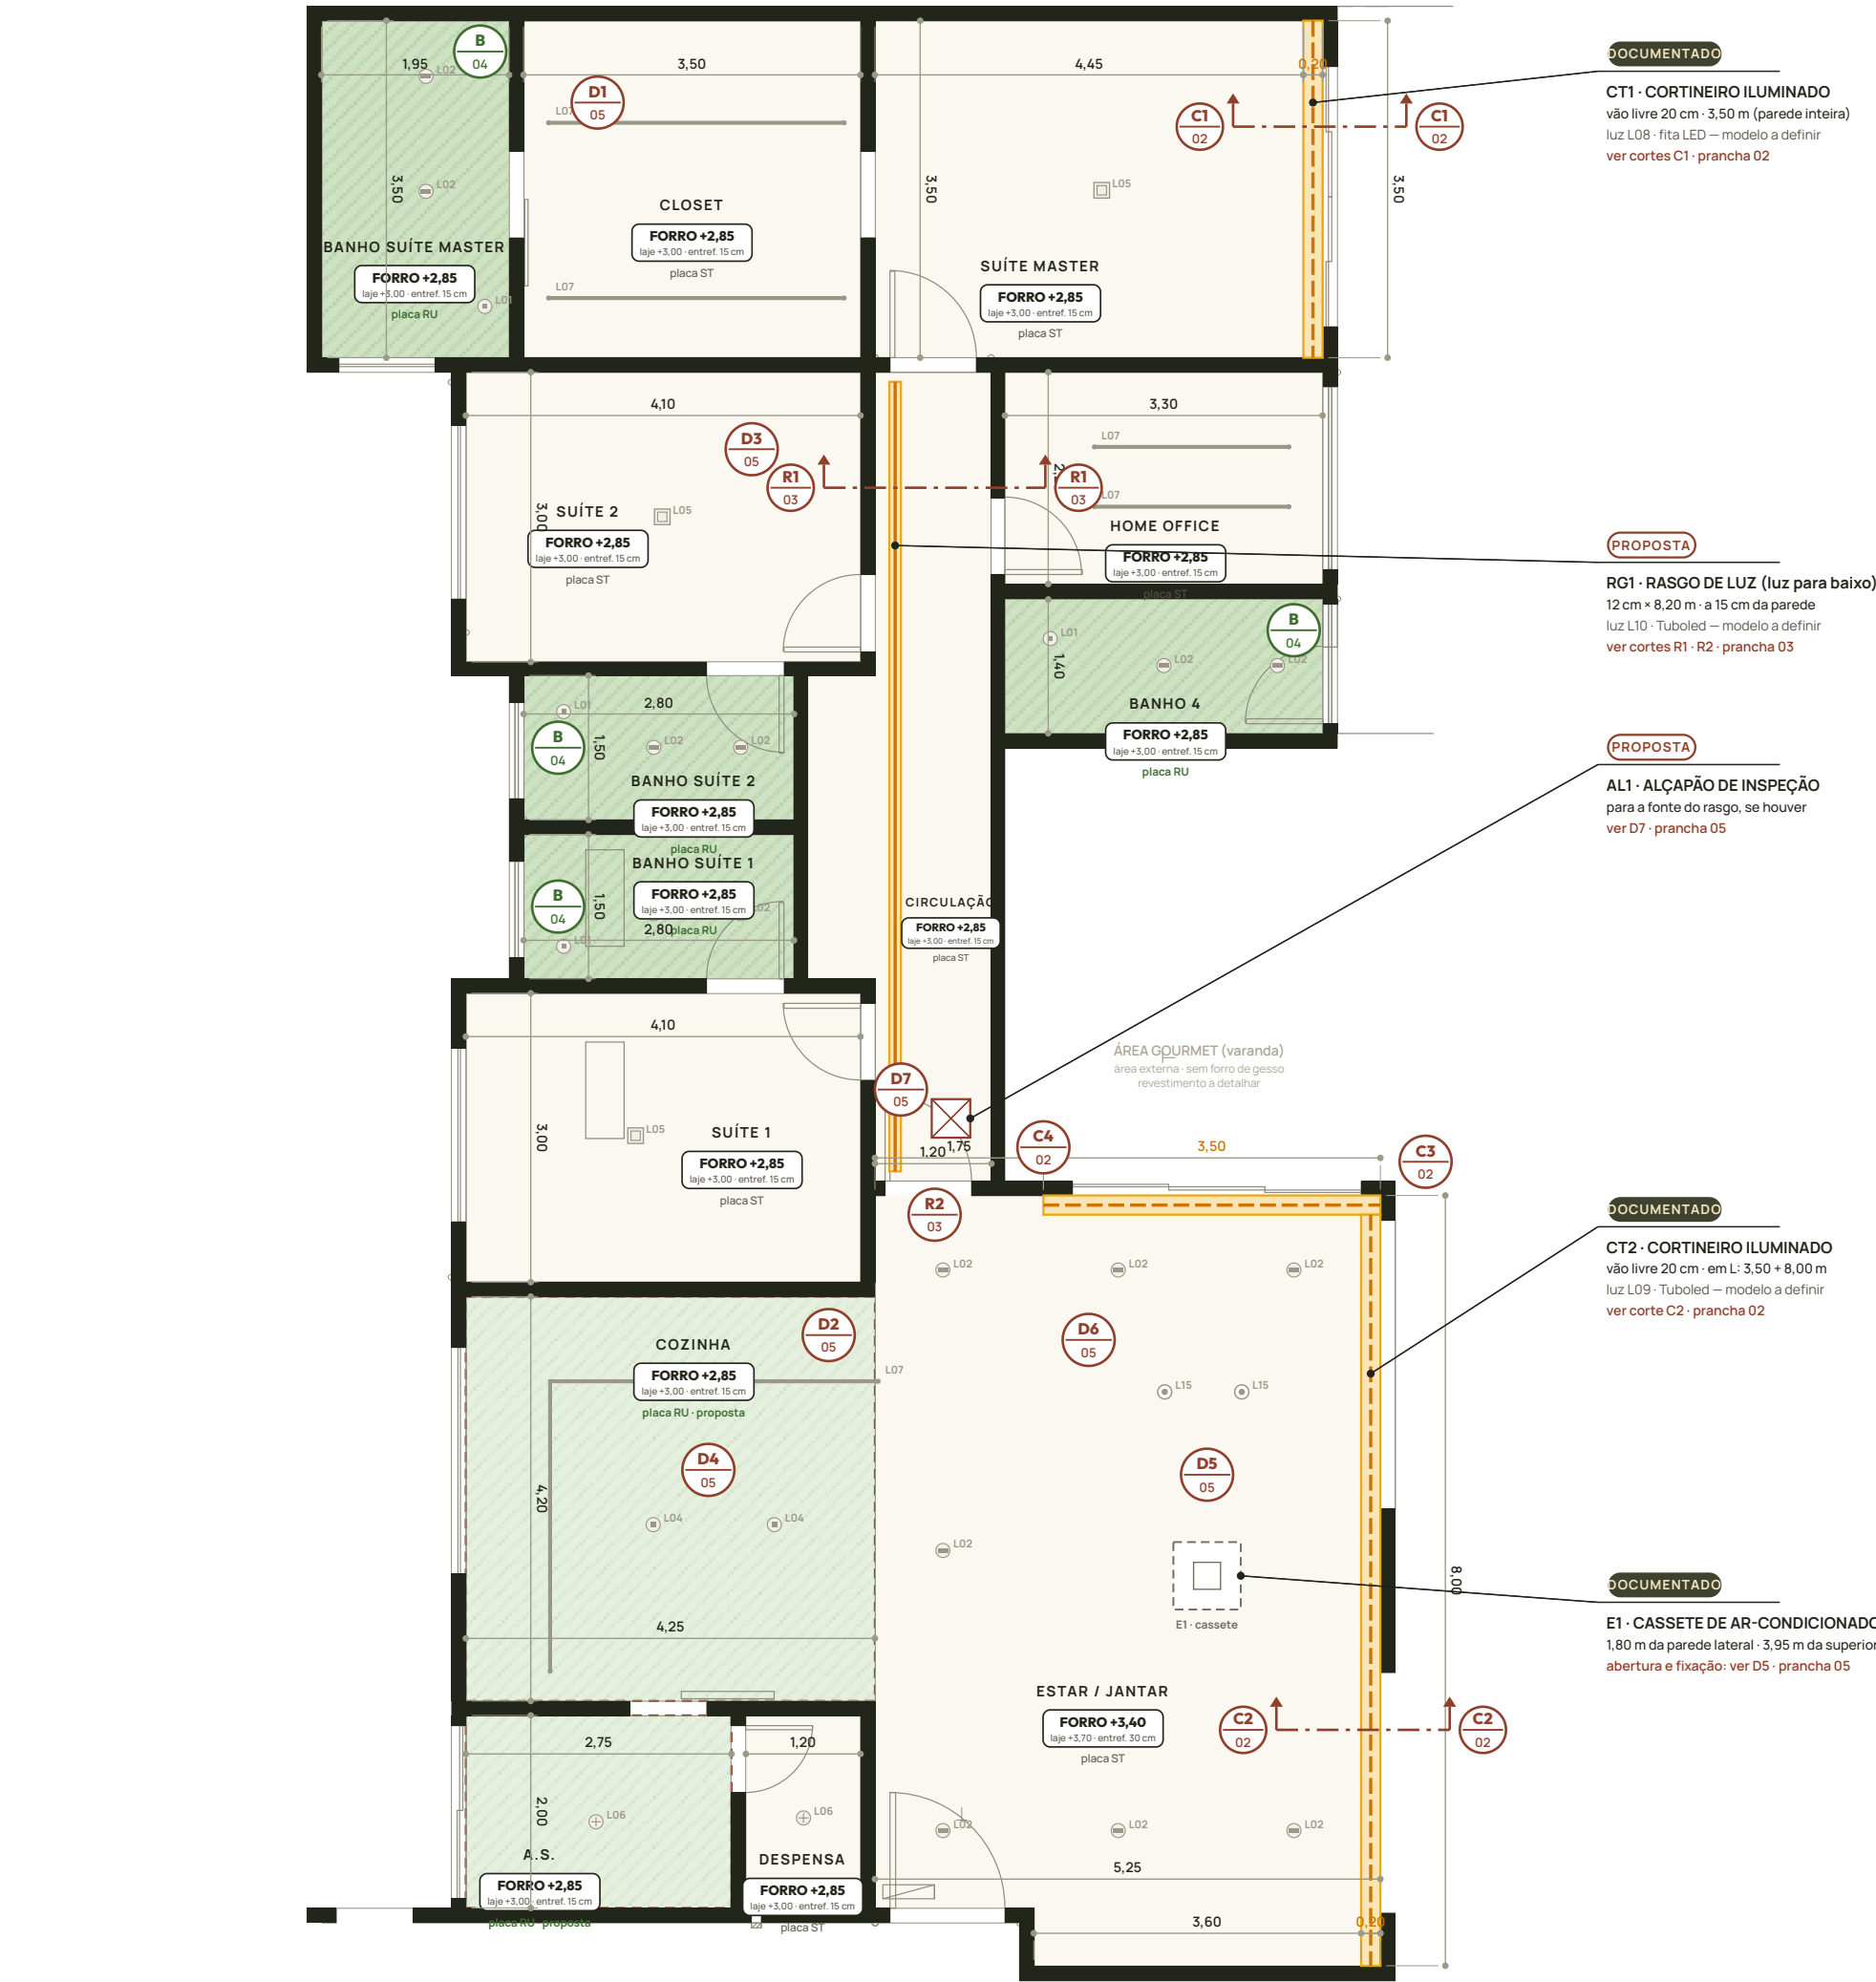

ESQUEMA DE NÍVEIS
corte esquemático - alturas do piso acabado ao forro e ao fundo da laje (DWG) - vertical 1:60, horizontal sem escala

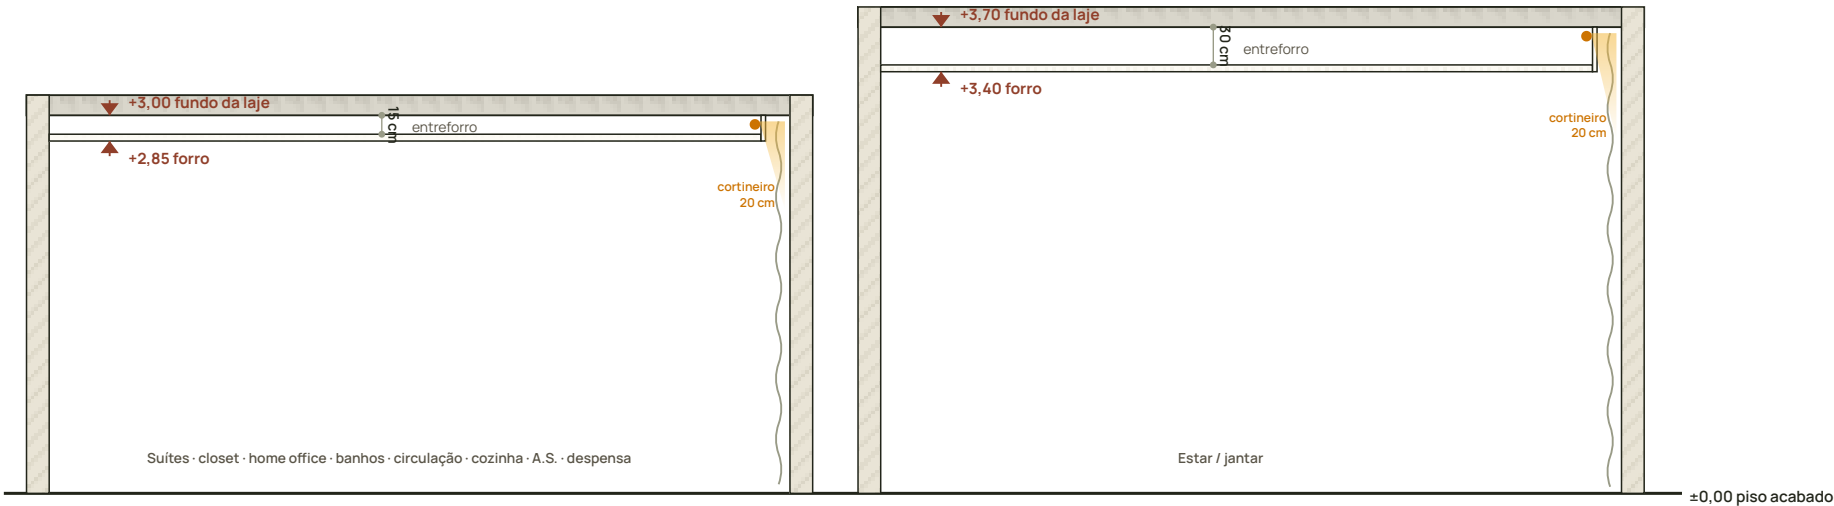

01 Planta de forro

Escala 1:75 · plotagem em A2 · cotas em metros · faces internas acabadas · conferir as medidas no local



Ambientes e níveis

QUADRO 1					
AMBIENTE	PLACA	FORRO	LAJE	ENTREF.	ÁREA m²
Banho Suite Master	RU	2,85	3,00	15 cm	6,83
Closet	ST	2,85	3,00	15 cm	12,25
Suite Master	ST	2,85	3,00	15 cm	15,75
Suite 2	ST	2,85	3,00	15 cm	12,30
Banho Suite 2	RU	2,85	3,00	15 cm	4,20
Banho Suite 1	RU	2,85	3,00	15 cm	4,20
Suite 1	ST	2,85	3,00	15 cm	12,30
Circulação	ST	2,85	3,00	15 cm	12,85
Home Office	ST	2,85	3,00	15 cm	7,26
Banho 4	RU	2,85	3,00	15 cm	4,62
Cozinha	RU PROPOSTA	2,85	3,00	15 cm	17,85
A.S.	RU PROPOSTA	2,85	3,00	15 cm	5,50
Despensa	ST	2,85	3,00	15 cm	2,40
Estar / Jantar	ST	3,40	3,70	30 cm	41,00

Alturas em metros a partir do piso acabado. Forro e área: planta de forro de gesso do DWG. Laje: cortes AA e BB do DWG. Placa RU nos banhos: DWG. RU na cozinha e na A.S.: proposta desta revisão. ST nos demais: placa padrão para ambientes secos, proposta.

ELEMENTO	VÃO	COMPR.	STATUS
CT1 cortineiro · suite master L08 fita LED · modelo a definir	20 cm	3,50 m	DOC
CT2 cortineiro · estar/jantar L09 Tuboled · modelo a definir	20 cm	3,50 + 8,00 m	DOC
RG1 rasgo · circulação L10 Tuboled · modelo a definir	12 cm	8,20 m	PROPOSTA

Legenda

- Forro de gesso · placa ST
ambientes secos
- Forro de gesso · placa RU (verde)
banhos · documentado
- Placa RU proposta
cozinha e A.S. · aguarda aprovação
- Cortineiro iluminado · vão 20 cm
faixa = vão no forro · traço = fonte de luz
- Rasgo de luz · luz para baixo
faixa = rasgo · linha = fonte de luz
- Luminárias · posição indicativa
códigos do caderno de iluminação · sem locação
- Cassete de ar-condicionado E1
posição do caderno de tomadas R05
- Alçapão de inspeção
proposta
- Chamada de detalhe
código / prancha
- Cota em metros
faces internas acabadas

DOCUMENTADO dado dos arquivos PROPOSTA aguarda aprovação

QUADRO 2

Observações

QUADRO 3

- Base**
Planta de forro de gesso e cortes AA/BB do DWG "Projeto Ivan e Ana R01", caderno de iluminação 02/04 R01; tomadas 01/04 R05; esquadrias R01.
- Área do forro**
Somente ambientes internos. Garagem, varanda gourmet e beirais recebem outro revestimento, a detalhar em caderno próprio.
- Cortineiros (CT1, CT2)**
Vão livre de 20 cm (decisão de 30/09/2026), medido da parede acabada à face interna da testeira. Comprimentos gerais do DWG. Tipo de cortina, trilho e fonte de luz a definir com os fornecedores.
- Rasgo (RG1)**
Luz voltada para baixo, reforçando a iluminação geral da circulação. Posição, largura e extremidades são proposta; ajustar ao Tuboled escolhido.
- Luminárias**
Símbolos só indicam tipo e quantidade de recortes. Locação conforme caderno de iluminação e marcação em obra.
- Banhos**
Placa RU (verde) resiste à umidade, mas não é impermeável. Ver prancha 04.
- Entreforro de 15 cm**
Nas alas íntima e de serviço há só 15 cm entre forro e laje. Conferir a altura de embutimento de L05, L07 e das fontes antes de comprar.
- Compatibilizar**
Cassete E1 (entreforro 30 cm × manual Gree); hi-walls E2 a E6 acima das portas; duto da coifa; linhas frigorígenas e dreno. Executar o forro após testes das instalações do entreforro.
- Especificação do sistema**
Espessura das placas, perfis, pendurais, fixações e espaçamentos conforme manual do fabricante escolhido e ABNT NBR 15758-2. Ver prancha 06.
- Pendências**
Fabricante de referência; modelos da fita LED e do Tuboled; tipo de cortina e trilho; box dos banhos (até o teto?); aprovação das propostas marcadas.



CARIMBO

PROJETO
Residência Ivan e Ana Neris
Nova Odessa - SP

RESPONSÁVEIS TÉCNICAS
Lidiane Barbosa · CAU A290220-6
Isadora Ferrari · CAU A263982-8

PLANTA
Forro de gesso


DATA
30/09/2026

ESCALA
1:75 · folha A2


PRANCHA
01/06

REVISÃO
R01


Imprimir em A2 sem ajuste de escala

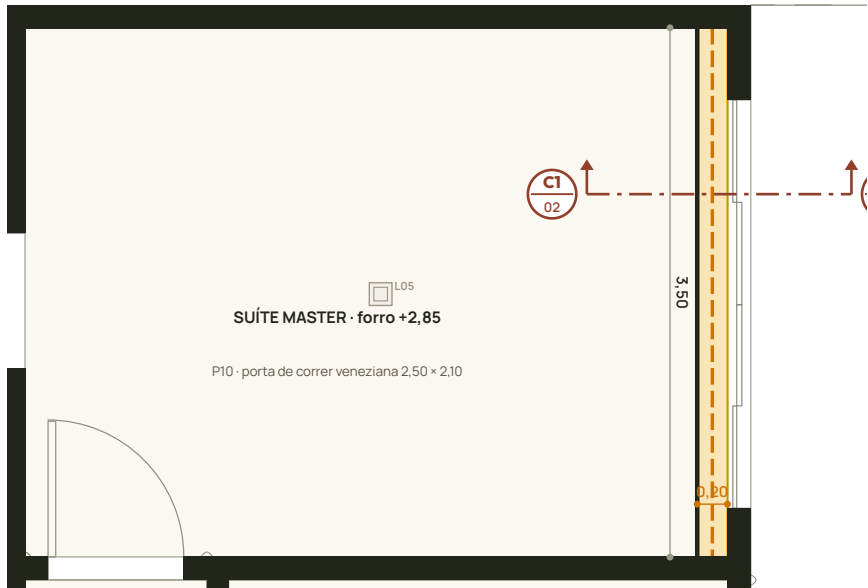


CT1 Cortineiro • suite master
planta 1:50 · L08 fita LED

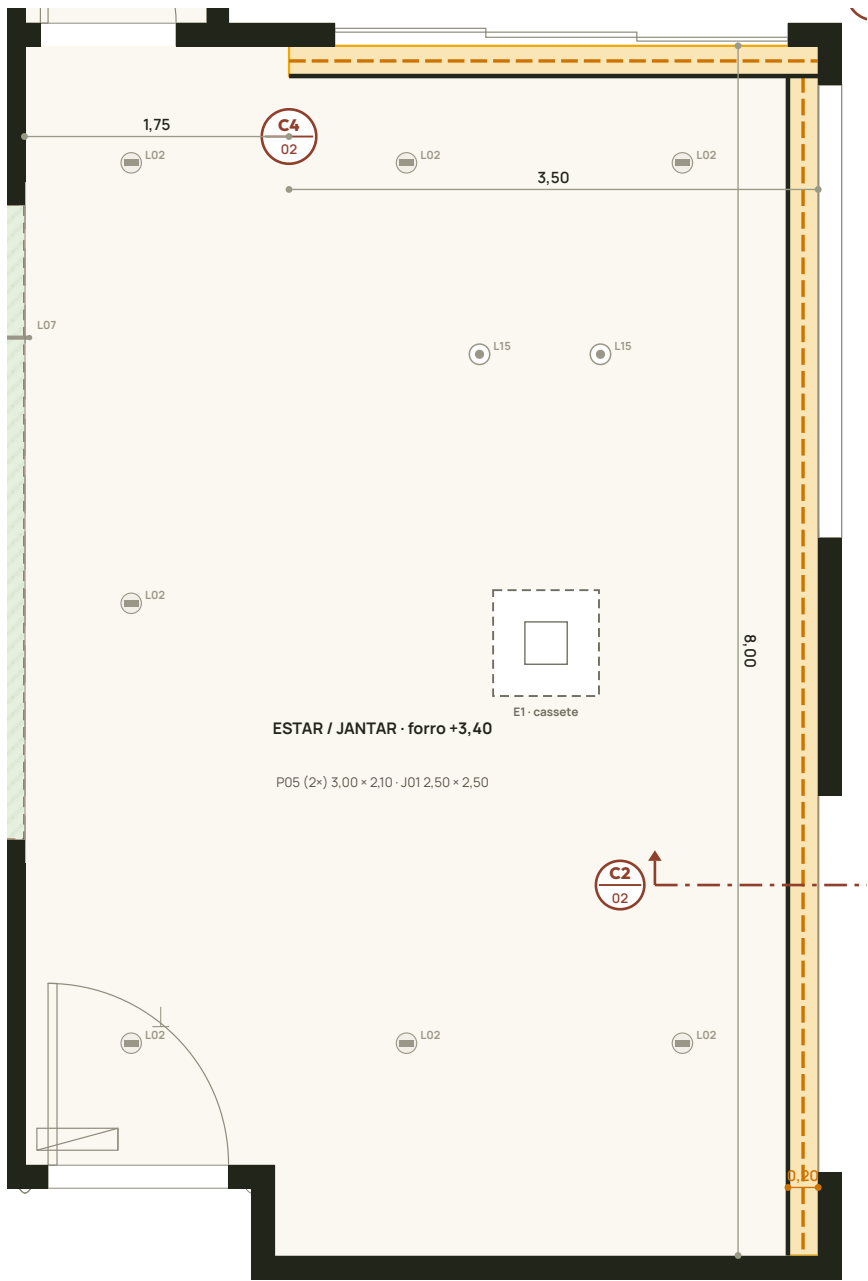

CT2 Cortineiro • estar / jantar
planta 1:50 · L09 TuboLED

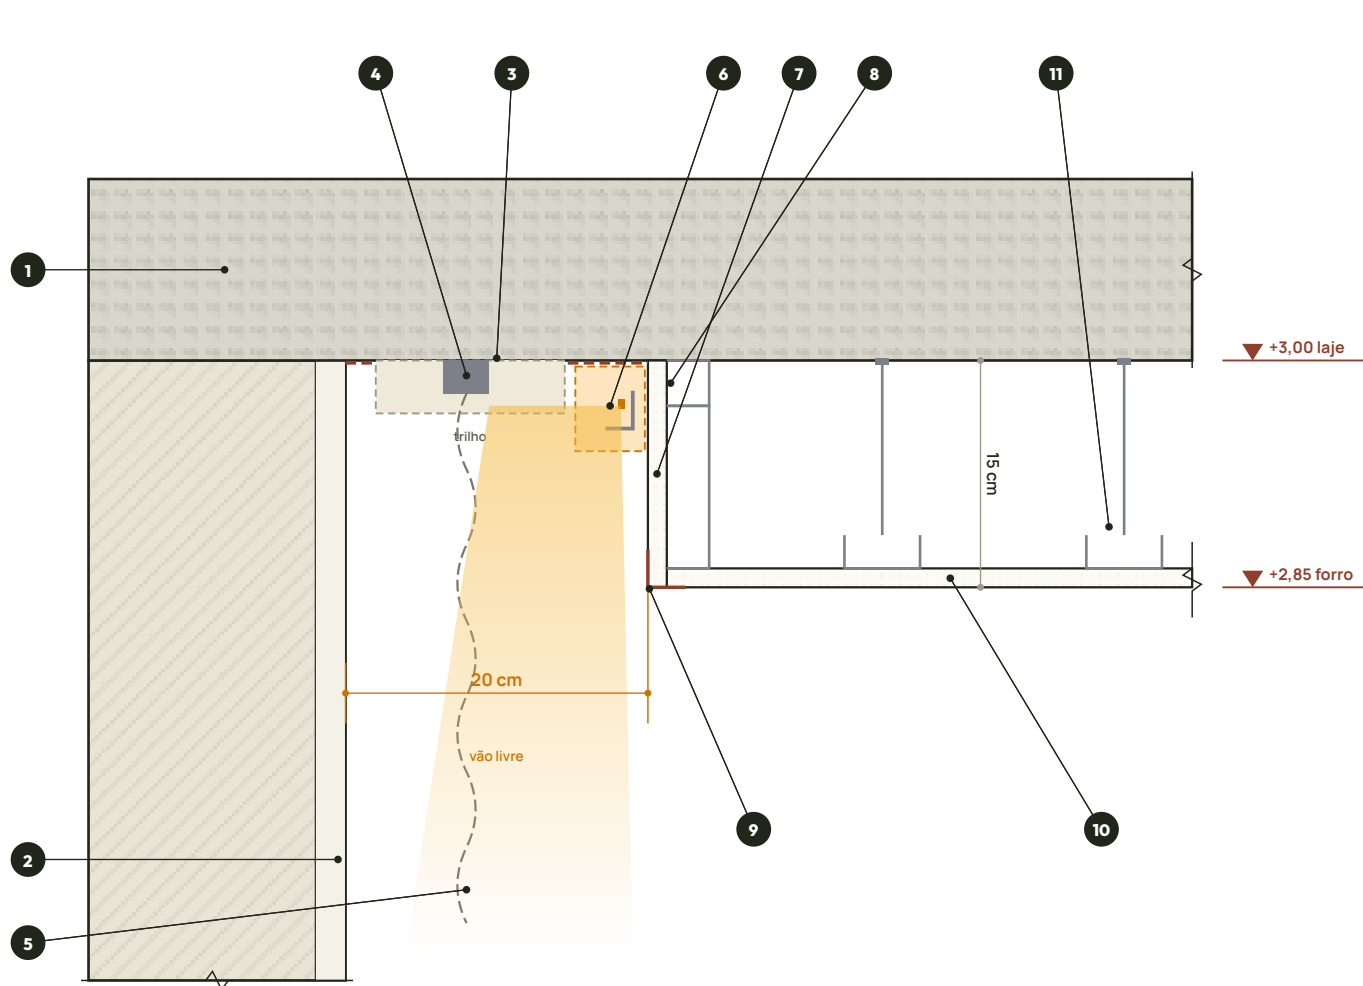



C1 Corte do cortineiro • suite master
escala 1:5 · entreforro 15 cm

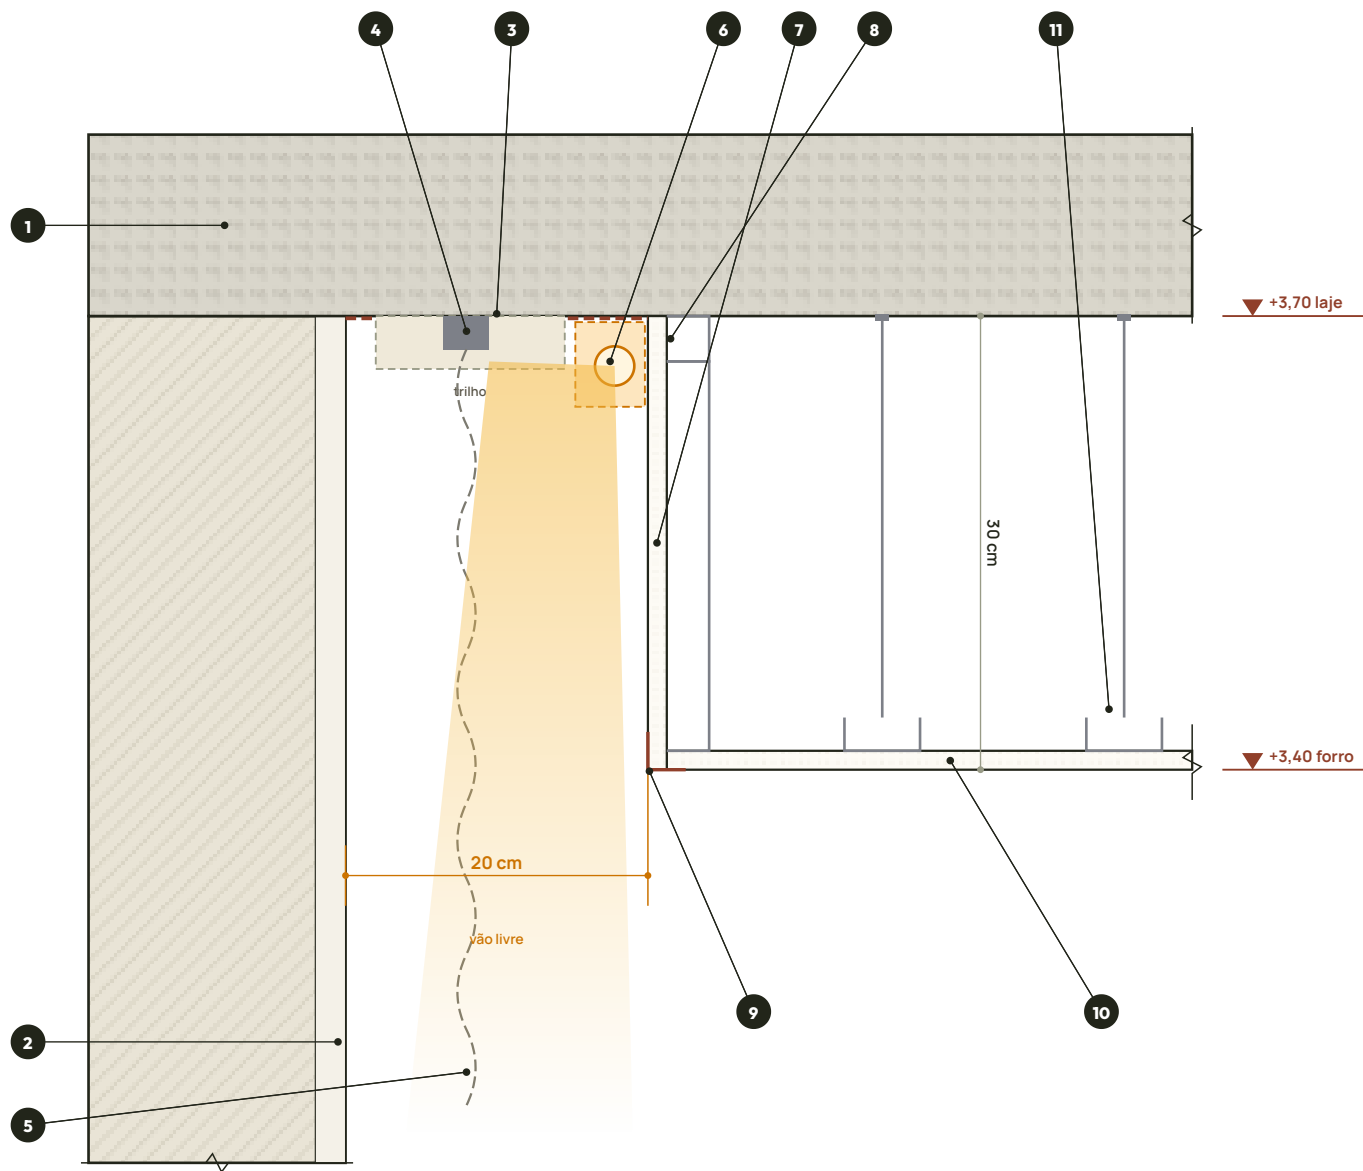


C2 Corte do cortineiro • estar / jantar
escala 1:5 · entreforro 30 cm

02 Cortineiros iluminados


CT1 suite master · CT2 estar/jantar · vão livre 20 cm · cotas em metros (plantas) e centímetros (cortes)

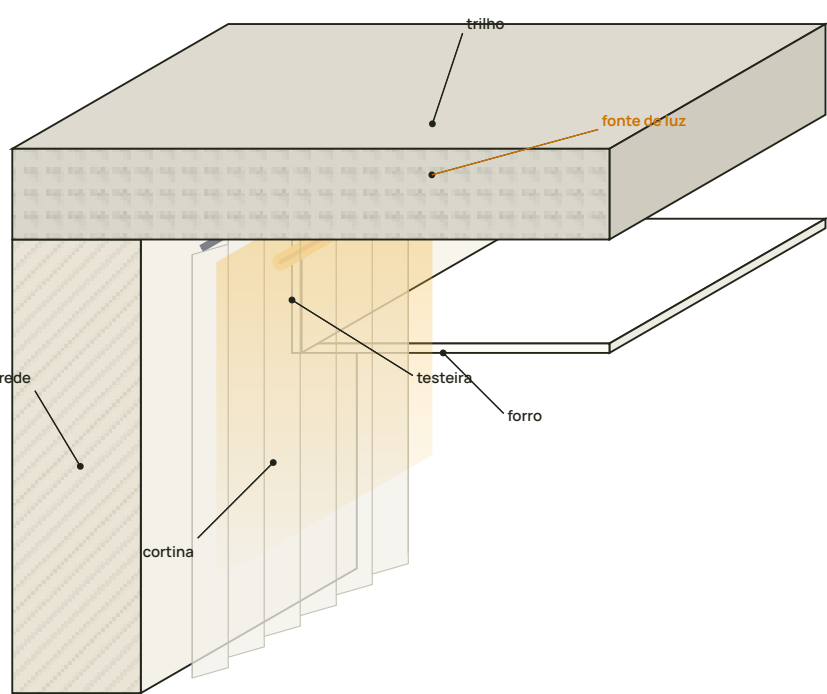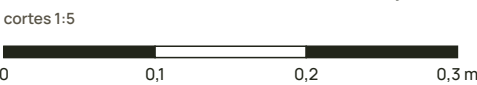

3D Como funciona
perspectiva do corte · sem escala

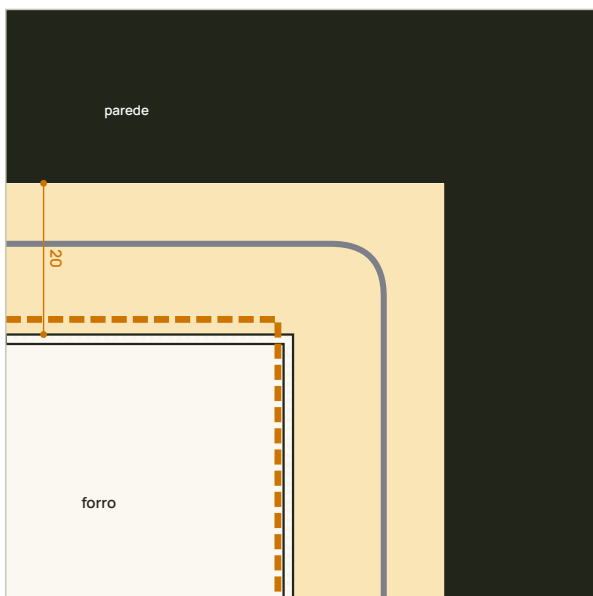

C3 Canto em L • CT2
planta 1:10

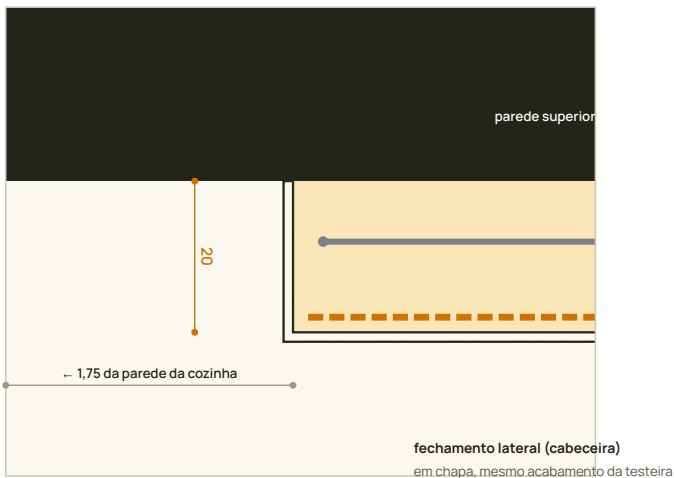

C4 Cabeceira • CT2
planta 1:10

Componentes

QUADRO 1

1	Laje pré-fabricada = fundo do cortineiro Regularizar e pintar em branco fosco no trecho do vão.	PROPOSTA
2	Parede acabada Referência para medir o vão livre de 20 cm (após reboco/pintura).	DOC
3	Trilho da cortina, fixado na laje Tipo, quantidade e posição a definir com o fornecedor da cortina.	A DEFINIR
4	Espaço reservado para o trilho Faixa junto à parede; manter livre de fixações do forro.	PROPOSTA
5	Cortina Tipo a definir com o fornecedor.	A DEFINIR
6	Fonte de luz na face interna da testeira CT1: fita LED em perfil · CT2: TuboLED. Voltada para a cortina, escondida pela testeira. Modelo a definir com a loja.	PROPOSTA
7	Testeira em chapa de gesso até a laje Fecha o entreforro e esconde a fonte. Mesma placa do forro.	PROPOSTA
8	Perfil de fixação da testeira Guia na laje e montante vertical. Tipo e fixação conforme fabricante.	PROPOSTA
9	Cantoneira de proteção da aresta Aresta inferior da testeira; massa e pintura por cima.	PROPOSTA
10	Forro em chapa de gesso ST Espessura conforme fabricante.	DOC
11	Estrutura e pendurais do forro Perfis, pendurais, fixações e espaçamentos conforme manual do fabricante.	A DEFINIR

SEQUÊNCIA DE EXECUÇÃO PROPOSTA

1. Concluir e testar elétrica (pontos e circuitos da fonte) e ar-condicionado no entreforro.
2. Marcar na laje a linha da testeira: 20 cm da parede acabada, em toda a extensão.
3. Fixar o trilho (ou a base do trilho) na laje, antes de fechar a testeira.
4. Montar a estrutura do forro e a testeira; aplicar cantoneira na aresta.
5. Tratar juntas, lixar e pintar; pintar o fundo (laje) em branco fosco.
6. Instalar fonte de luz e driver; testar; instalar a cortina.

Observações

QUADRO 2

Vão livre de 20 cm
Decisão de 30/09/2026. Medido da parede acabada à face interna da testeira, em toda a extensão.

Comprimentos
CT1: parede inteira, 3,50 m. CT2: em L, 3,50 m na parede superior (a partir de 1,75 m da parede da cozinha) + 8,00 m na lateral. Conforme DWG.

Luz
A fonte fica no alto do vão, voltada para a cortina, e não aparece de quem está no ambiente. Deixar o driver dentro do cortineiro, acessível pelo vão.

Manutenção
Fonte, driver e trilho acessíveis por baixo, pelo vão de 20 cm. Não há alçapão.

Conferir
Topo da esquadria abaixo do forro: J01 a 3,00 m (caderno de esquadrias); o DWG indica 2,50 m.

DUNAS duas
design
& arq

CARIMBO

PROJETO
Residência Ivan e Ana Neris
Nova Odessa - SP

RESPONSÁVEIS TÉCNICAS
Lidiane Barbosa · CAU A290220-6
Isadora Ferrari · CAU A263982-8

PLANTA
Cortineiros


DATA
30/09/2026

ESCALA
1:50 · 1:10 · 1:5

PRANCHA
02/06

REVISÃO
R01

Imprimir em A2 sem ajuste de escala

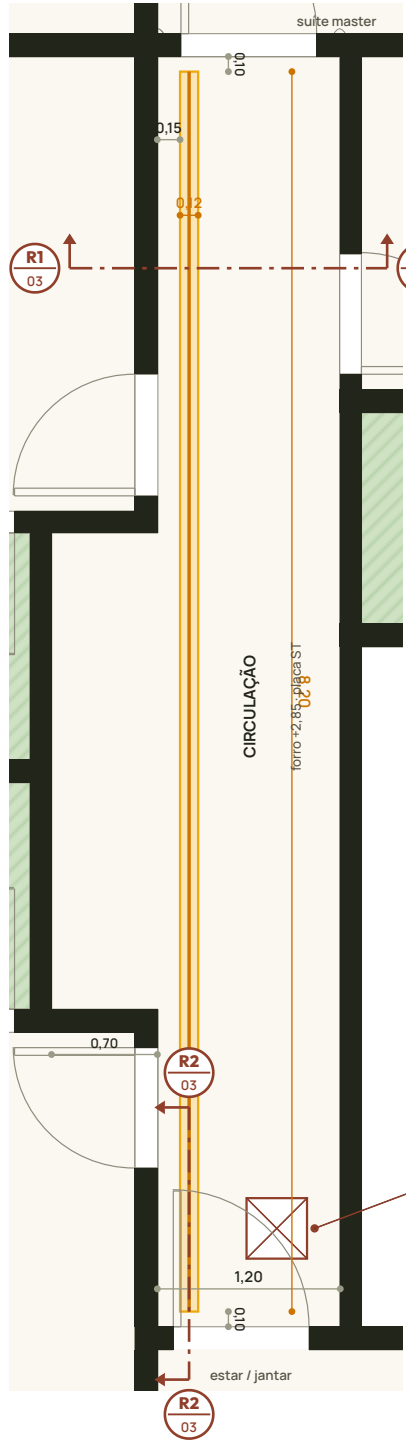

RG1 Rasgo • planta

planta 1:50

PROPOSTA

dimensões a ajustar ao Tuboled escolhido

12 cm

largura do rasgo

15 cm


da parede esquerda

≈ 15 cm

altura até a laje


8,20 m

comprimento

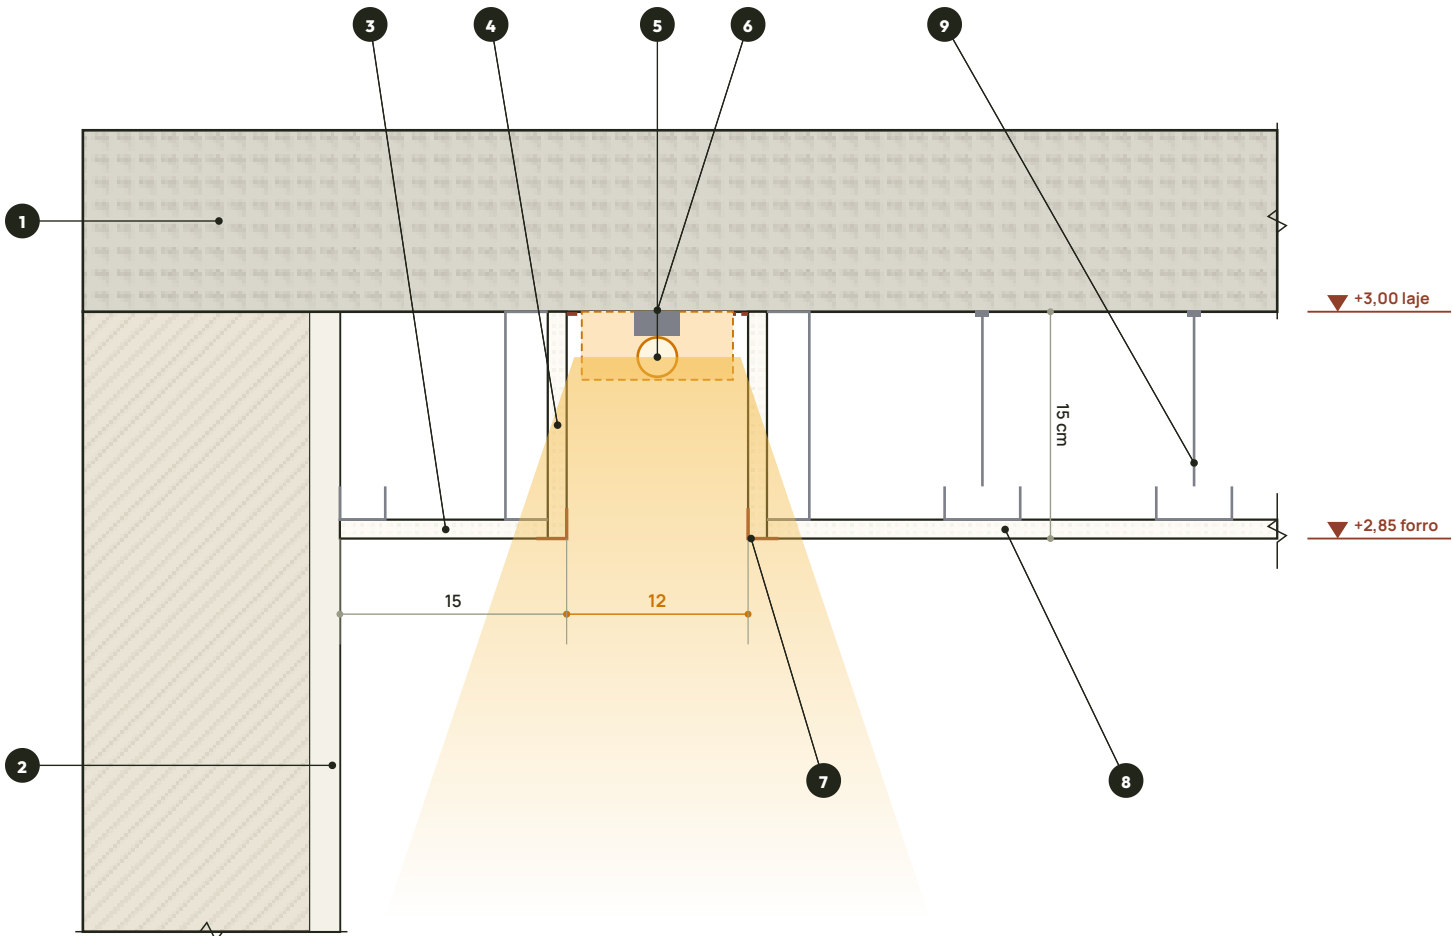


R1 Corte transversal do rasgo

escala 1:5 · luz para baixo

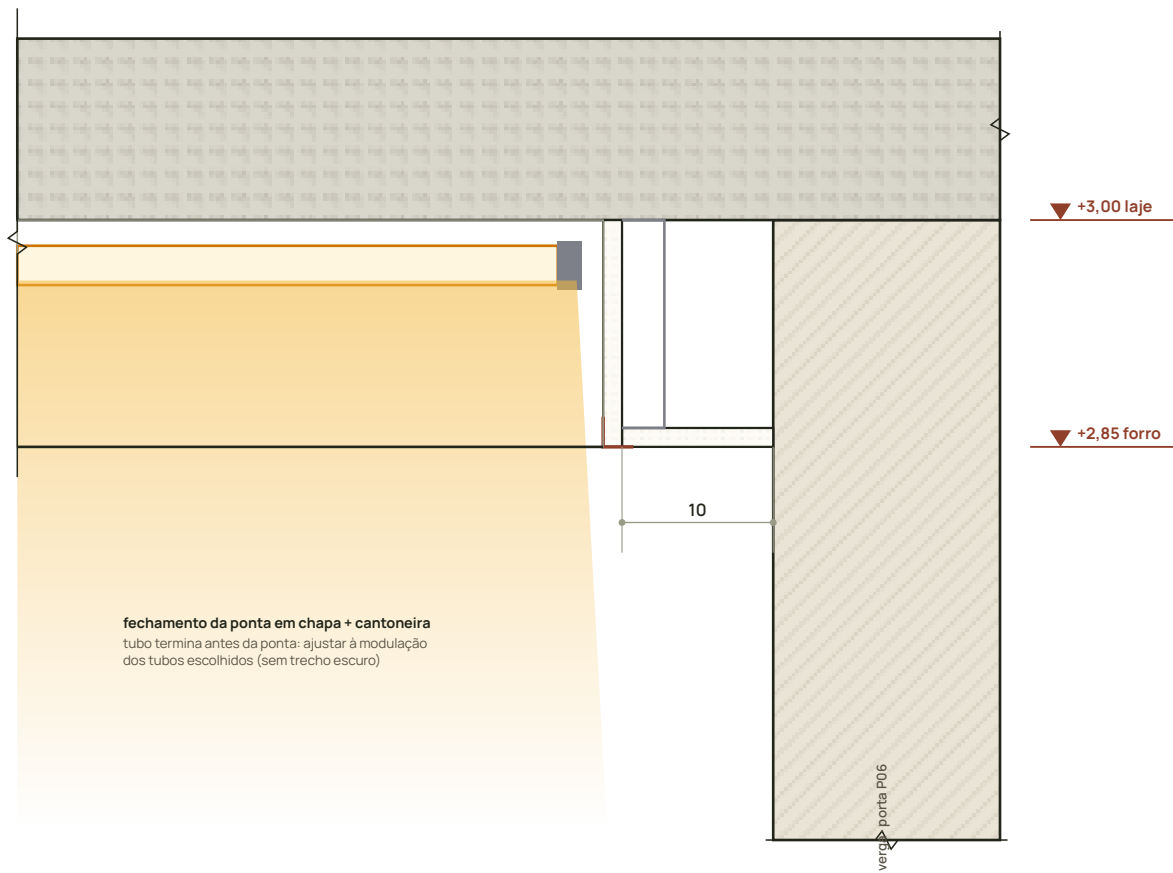

R2 Extremidade do rasgo

escala 1:5 · junto à porta do estar

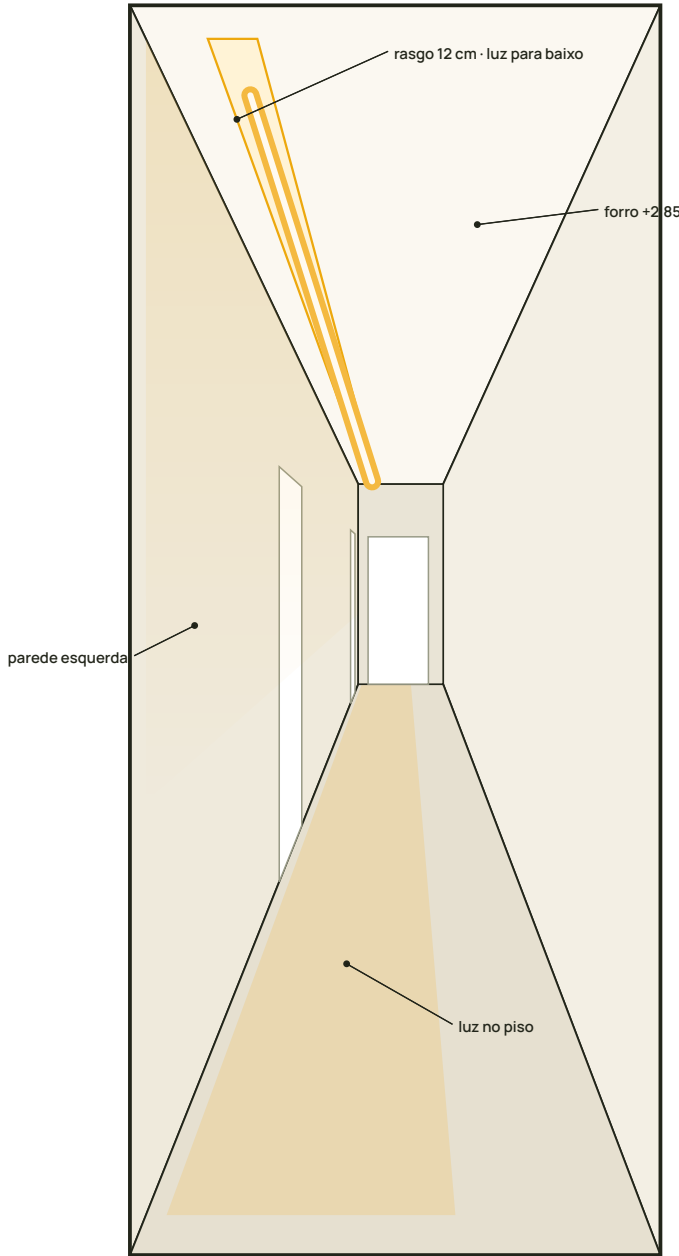


3D Como se vê da circulação

perspectiva · sem escala

03 Rasgo de luz • circulação

RG1 · luz para baixo · dimensões propostas, aguardando aprovação · cotas em metros (planta) e centímetros (cortes)

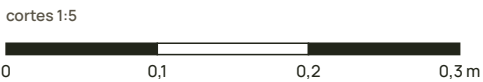

Componentes

QUADRO 1

1	Laje pré-fabricada = fundo do rasgo Regularizar e pintar em branco fosco (melhora o rendimento da luz).	PROPOSTA
2	Parede esquerda acabada Referência para a faixa de 15 cm.	DOC
3	Faixa de forro de 15 cm junto à parede Mantém a luz no piso da circulação, sem mancha forte na parede.	PROPOSTA
4	Laterais do rasgo em chapa até a laje Com perfil de fixação na laje e no forro, conforme fabricante.	PROPOSTA
5	Tuboled (L10) no fundo do rasgo Modelo, suporte e modulação a definir com a loja de iluminação.	A DEFINIR
6	Suporte do tubo fixado na laje Conforme o produto escolhido.	A DEFINIR
7	Cantoneiras nas duas arestas Aresta viva e reta, massa e pintura por cima.	PROPOSTA
8	Forro em chapa de gesso ST Espessura conforme fabricante.	DOC
9	Estrutura e pendurais do forro Conforme manual do fabricante; manter fora do vão do rasgo.	A DEFINIR

SEQUÊNCIA DE EXECUÇÃO PROPOSTA

- Concluir e testar elétrica (alimentação do Tuboled) no entreforro.
- Marcar na laje as duas linhas do rasgo (15 e 27 cm da parede esquerda).
- Fixar os suportes dos tubos na laje, conforme o produto escolhido.
- Montar laterais, fechamentos das pontas e forro; aplicar cantoneiras.
- Tratar juntas e pintar; pintar o fundo (laje) em branco fosco.
- Instalar e testar os tubos; conferir continuidade da luz.

Observações

QUADRO 2

Intenção de iluminação

Rasgo contínuo, com a luz voltada para baixo, reforçando a iluminação geral da circulação. Mantido do lado esquerdo, como no caderno de iluminação (L10).

Dimensões propostas

Largura 12 cm, a 15 cm da parede esquerda, 8,20 m de comprimento (10 cm livres em cada ponta). Altura até a laje: cerca de 15 cm, medir em obra.

Produto

Antes de fechar o forro, confirmar com a loja o diâmetro do tubo, o suporte e o comprimento das peças. Ajustar largura e comprimento do rasgo ao produto.

Manutenção

Tubos trocados por baixo, pelo próprio rasgo. Se o produto usar fonte externa, prever o alçapão AL1 (D7, prancha 05) perto da ponta junto ao estar.

Portas

O rasgo passa acima das portas da circulação (topo a 2,10 m). Não há interferência.



CARIMBO

PROJETO
Residência Ivan e Ana Neris
Nova Odessa – SP

RESPONSÁVEIS TÉCNICAS
Lidiane Barbosa · CAU A290220-6
Isadora Ferrari · CAU A263982-8

PLANTA
Rasgo de luz


ESCALA
1:50 · 1:5

Imprimir em A2 sem ajuste de escala

DATA
30/09/2026

PRANCHA
03/06


REVISÃO
R01

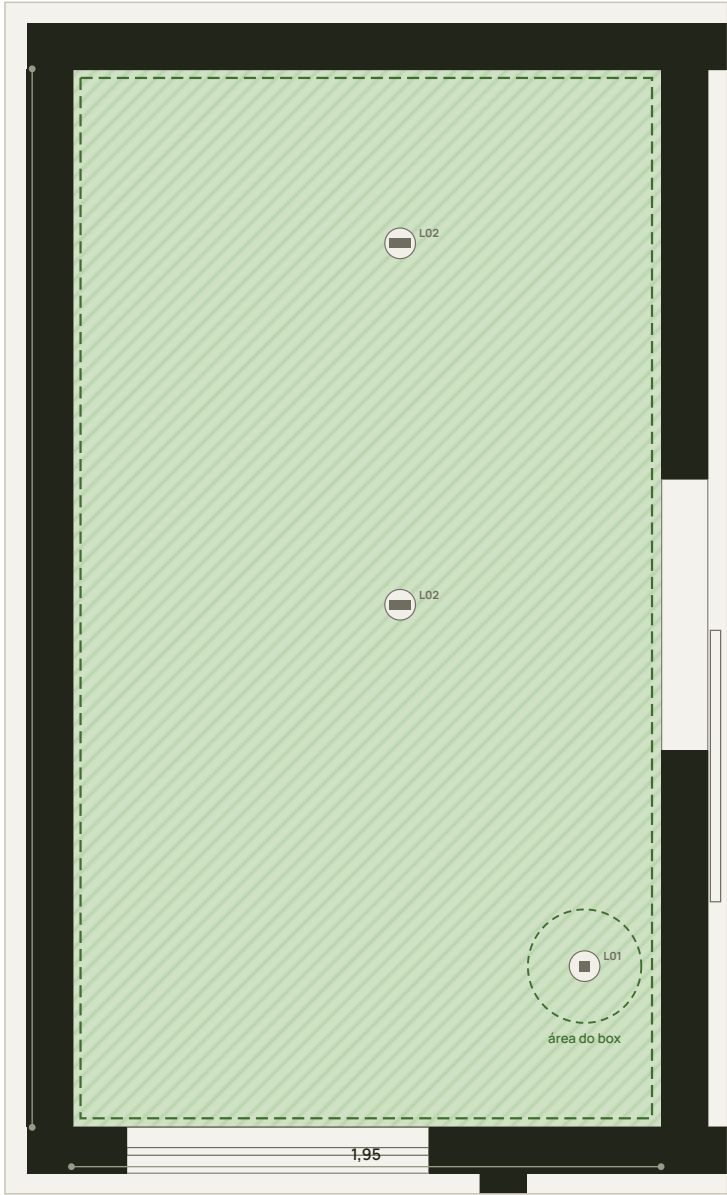


B Banho Suíte Master
planta 1:25 · 6,83 m² · forro +2,85 · placa RU



B Banho Suíte 2
planta 1:25 · 4,20 m² · forro +2,85 · placa RU

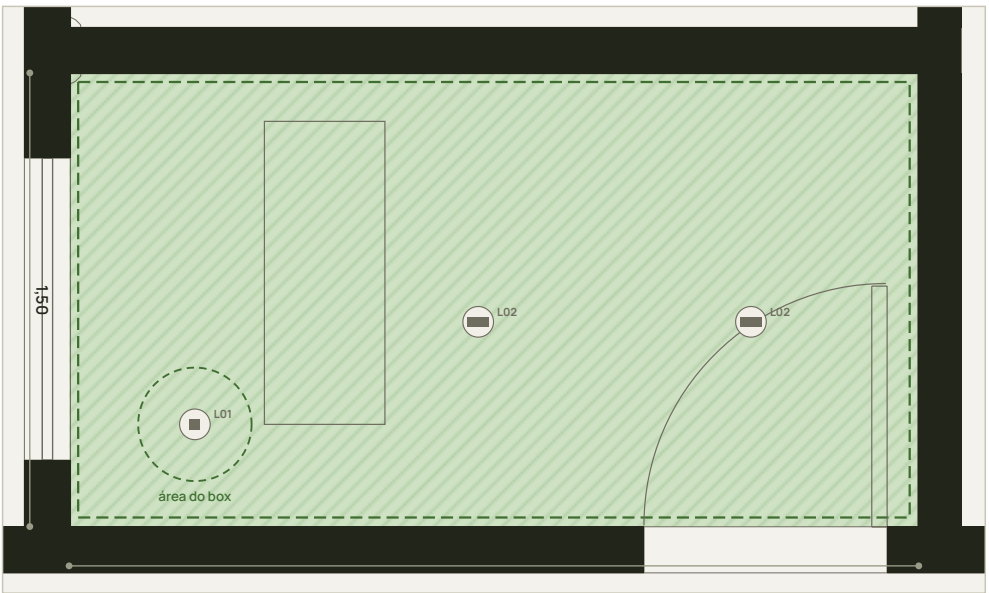


B Banho Suíte 1
planta 1:25 · 4,20 m² · forro +2,85 · placa RU

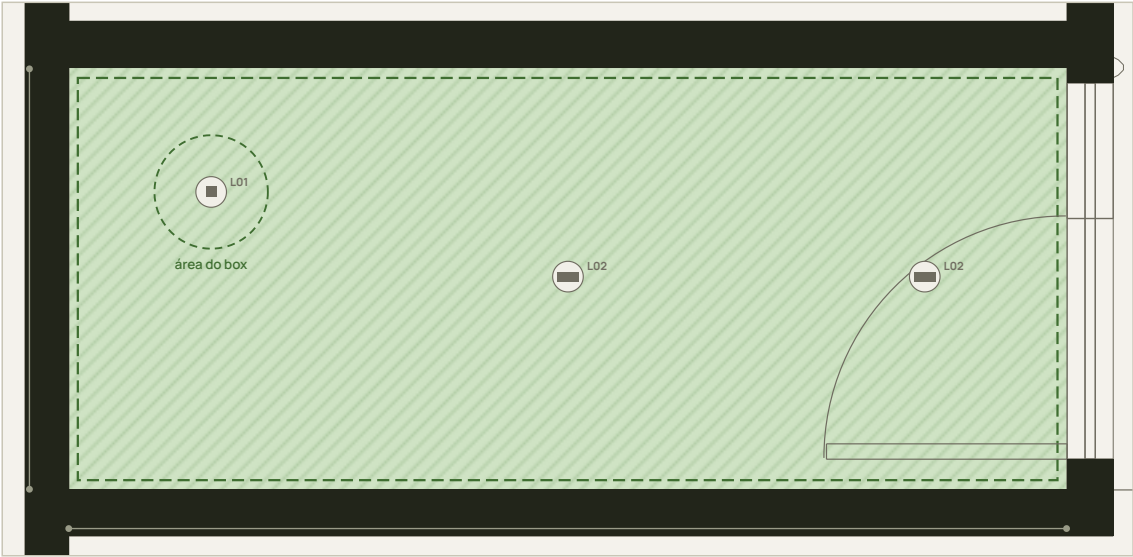


B Banho 4
planta 1:25 · 4,62 m² · forro +2,85 · placa RU



LOCALIZAÇÃO
planta-chave · sem escala
B = banhos com forro RU

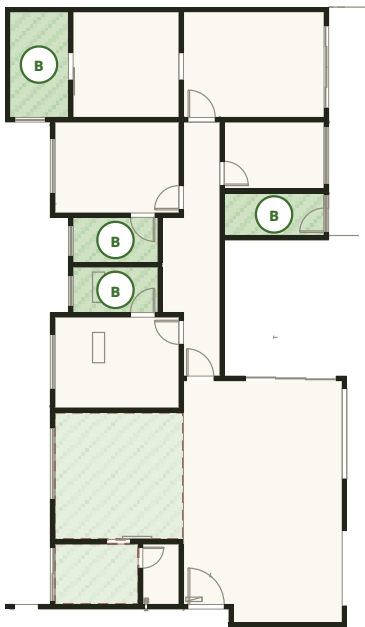

B1 Corte típico · forro RU no banho
escala 1:10 · vale para os 4 banhos

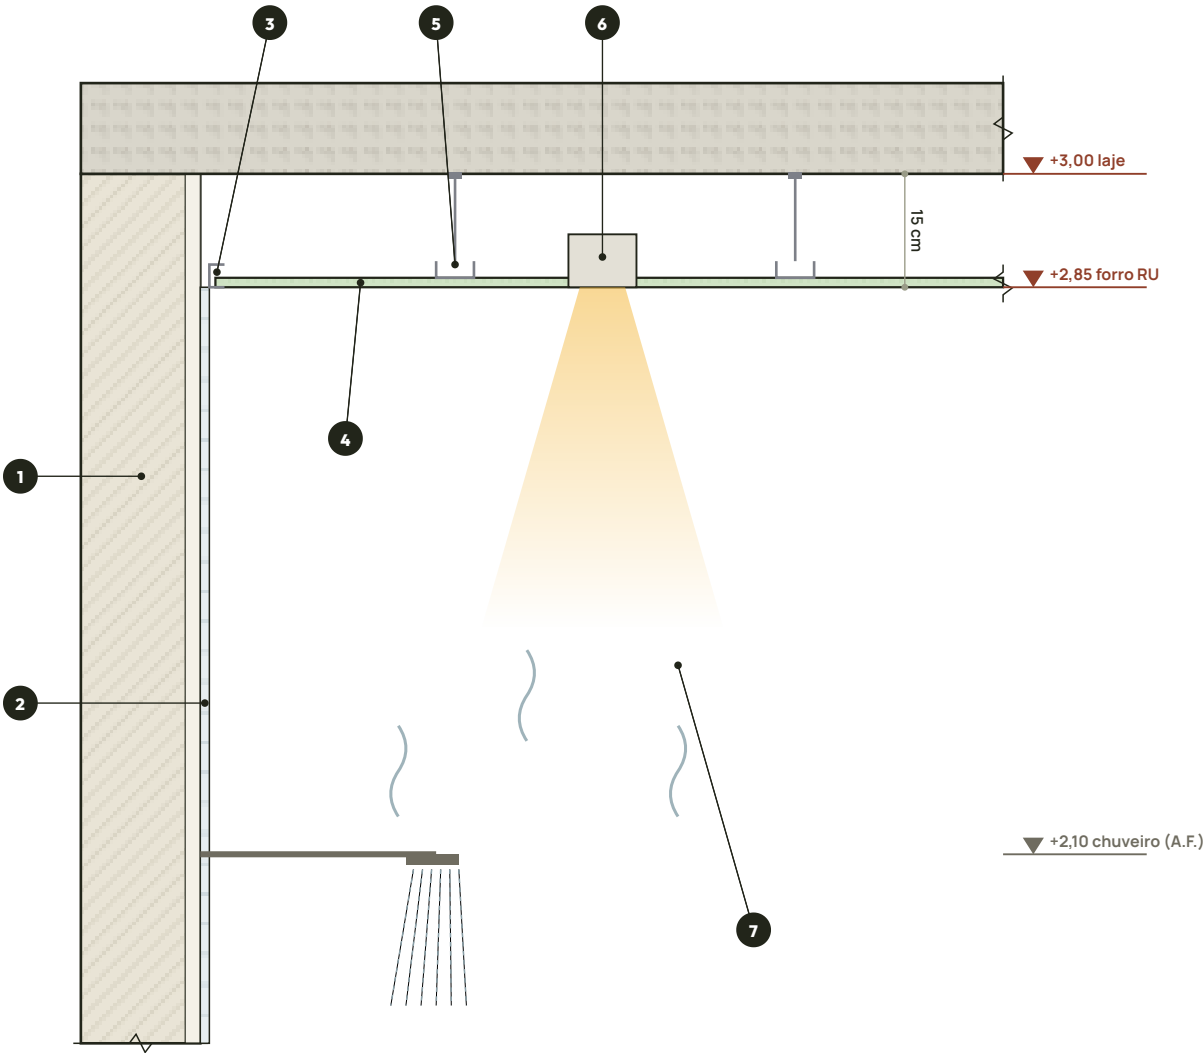

Adequação por banho

BANHO	m²	VENTILAÇÃO NATURAL	CHUVEIRO	BOX ATÉ O TETO?	EXAUSTÃO	PLACA RU
Banho Suite Master	6,83	J04 · basculante DOC	sim DOC	A CONFIRMAR	A CONFIRMAR	Adequada, se as condições ao lado forem atendidas
Banho Suite 2	4,20	J04 · basculante DOC	sim DOC	A CONFIRMAR	A CONFIRMAR	Adequada, se as condições ao lado forem atendidas
Banho Suite 1	4,20	J04 · basculante DOC	sim DOC	A CONFIRMAR	A CONFIRMAR	Adequada, se as condições ao lado forem atendidas
Banho 4	4,62	J06 · ventilação DOC	sim DOC	A CONFIRMAR	A CONFIRMAR	Adequada, se as condições ao lado forem atendidas

Janelas e chuveiros: cadernos de esquadrias e hidráulica. As alturas das janelas serão revistas (mais baixas) e não interferem no forro. Se o box for fechado até o teto, o vapor fica confinado junto ao forro: consultar o fabricante antes de manter a placa RU sobre o box.

Componentes

QUADRO 1

1	Parede	Alvenaria existente/projeto.	DOC
2	Revestimento cerâmico até o forro	B.I. total nos banhos, conforme corte AA do DWG.	DOC
3	Tabica / perfil perimetral	Junta aberta (negativo) entre forro e revestimento, largura conforme modelo da tabica (ver D1).	PROPOSTA
4	Forro em placa RU (verde)	Juntas e massa próprias para áreas úmidas, conforme fabricante.	DOC
5	Estrutura e pendurais	Aço galvanizado; espaçamentos para placa RU conforme manual do fabricante.	A DEFINIR
6	Luminária embutida L01/L02	Peça com grau de proteção adequado a área molhada (a confirmar na ficha técnica).	A DEFINIR
7	Vapor do banho	Ventilar após o uso; forro RU tolera umidade eventual, não água.	DOC

Placa RU

QUADRO 2

Resistente à umidade não é impermeável.

O que a placa RU faz
Absorve menos água que a placa comum e suporta a umidade do ar do banho, de forma intermitente, em ambiente ventilado.

O que ela não faz
Não resiste à água corrente, jato, respingo direto nem vazamento. Não é barreira de água e não substitui impermeabilização.

Condições para usar
Uso interno · ventilação natural ou mecânica · sem contato direto com água · sem vapor contínuo (sauna, ofurô fechado) · pintura própria para áreas úmidas · tratamento de juntas com produtos para RU. Confirmar cada item no manual do fabricante escolhido.

Uso e manutenção
Manter a janela ou o exaustor em uso após o banho. Vazamento no entreforro (hidráulica ou dreno) deve ser corrigido e a placa atingida substituída.



CARIMBO

PROJETO
Residência Ivan e Ana Neris
Nova Odessa - SP

RESPONSÁVEIS TÉCNICAS
Lidiane Barbosa · CAU A290220-6
Isadora Ferrari · CAU A263982-8

PLANTA
Banheiros · RU

DATA
30/09/2026

ESCALA
1:25 · 1:10

PRANCHA
04/06

REVISÃO
R01

Imprimir em A2 sem ajuste de escala

D1 Encontro com parede
escala 1:5

Tabica perimetral em todos os ambientes. Junta aberta evita trinca no encontro forro × parede. Modelo a aprovar.

PROPOSTA

D2 Mudança de nível
escala 1:12,5

Níveis 2,85 / 3,40 do DWG; a troca acontece sempre sobre parede (verga). Tabica dos dois lados, como em D1.

DOCUMENTADO

D3 Recorte · luminária pontual
escala 1:5

L01, L02, L04, L05. Recorte com gabarito da peça; peças pesadas (L05) apoiadas na estrutura, não só na placa.

PROPOSTA

D4 Recorte linear · perfil L07
escala 1:5

Closet (2), home office (2) e cozinha (L). Rasgo reto e contínuo, largura do perfil; bordas reforçadas em todo o comprimento.

PROPOSTA

D5 Cassete de ar-condicionado
escala 1:10

Posição: tomadas R05 (1,80 × 3,95 m). Abertura conforme gabarito Gree; o forro não sustenta o aparelho. Conferir 30 cm.

DOCUMENTADO

D6 Pendentes L15 · jantar
escala 1:5

Peso do pendente vai para a laje, não para a placa. Posição final após definir o modelo (caderno de iluminação).

PROPOSTA

D7 Alçapão de inspeção
escala 1:5

AL1 na circulação, só se a fonte do rasgo for externa. Alçapão pronto para drywall, tampa em placa, fecho por pressão.

PROPOSTA

D8 Junta de controle
escala 1:5

Estar/jantar (41 m²): aplicar se o manual do fabricante exigir para essa área ou comprimento. Posição a definir.

A DEFINIR

Observações

QUADRO 1

Como ler

Cada detalhe traz o selo DOCUMENTADO (dado dos arquivos), PROPOSTA (aguarda sua aprovação) ou A DEFINIR (depende de fornecedor ou fabricante).

Estrutura

Os perfis e pendurais desenhados são simbólicos. Tipo, espessura, espaçamento e fixação seguem o manual do fabricante escolhido.

Carga no forro

Nada pesado apoiado só na placa: cassete, pendentes e luminárias grandes fixados na laje ou na estrutura. Limites conforme fabricante.

Luminárias

Recortes marcados em obra com a peça ou o gabarito na mão. Fichas técnicas a receber da loja de iluminação.

Ordem

Instalações do entreforro testadas antes de fechar o forro.

05 Detalhes complementares

Encontros, níveis, recortes, equipamentos e acessos · cotas em centímetros



CARIMBO

PROJETO
Residência Ivan e Ana Neris
Nova Odessa – SP

RESPONSÁVEIS TÉCNICAS
Lidiane Barbosa · CAU A290220-6
Isadora Ferrari · CAU A263982-8

PLANTA
Detalhes

ESCALA
1:5 · 1:10

Imprimir em A2 sem ajuste de escala

DATA
30/09/2026

PRANCHA
05/06

REVISÃO
R01

Quadro de materiais

CÓD.	MATERIAL	ONDE	ESPECIFICAÇÃO DE PROJETO	DADO TÉCNICO · FONTE	STATUS
M1	Placa de gesso ST (standard)	Closet, suítes, home office, circulação, despensa, estar/jantar; testeiras e laterais do rasgo	Placa para ambiente seco	Espessura e tipo de borda: manual do fabricante	PROPOSTA
M2	Placa de gesso RU (verde)	Banho Suite Master, Banho Suite 1, Banho Suite 2, Banho 4	Resistente à umidade · não impermeável	Espessura e espaçamentos para RU: manual do fabricante	DOC
M3	Placa de gesso RU (verde)	Cozinha e A.S.	Vapor de cocção e lavagem	Idem M2	PROPOSTA
M4	Estrutura de aço galvanizado	Todos os forros, testeiras e laterais	Perfis para forro (ABNT NBR 15217)	Tipo, espaçamento e emendas: manual do fabricante	A DEFINIR
M5	Pendurais e fixação na laje	Todos os forros	Ancoragem adequada à laje pré-fabricada	Tipo, espaçamento e carga: fabricante + projeto estrutural	A DEFINIR
M6	Tabica perimetral	Todos os encontros forro × parede (D1, D2)	Junta aberta (negativo), cor branca	Modelo e largura a aprovar	PROPOSTA
M7	Cantoneira de proteção de aresta	Arestas das testeiras CT1/CT2 e do rasgo RG1	Aresta reta e protegida	Modelo conforme fabricante	PROPOSTA
M8	Fita e massa para juntas	Todas as juntas; nos banhos, produtos para RU	Tratamento de juntas do sistema	Produtos e demãos: manual do fabricante	A DEFINIR
M9	Parafusos e fixações	Placa × perfil, perfil × perfil	Aço com proteção à corrosão	Tipo e espaçamento: fabricante	A DEFINIR
M10	Pintura	ST: acrílica fosca branca · RU: tinta para áreas úmidas · fundo de cortineiros e rasgo: branco fosco	Acabamento final	Preparação e produto: fabricantes do forro e da tinta	PROPOSTA
M11	Alçapão de inspeção	AL1 (circulação), só se o rasgo tiver fonte externa	Alçapão pronto para drywall	Medida do modelo	PROPOSTA
M12	Perfil de junta de controle	Estar/jantar, se exigido	Junta de movimentação	Critério: manual do fabricante	A DEFINIR

Nenhum valor de espessura, espaçamento ou fixação foi adotado sem fonte: esses dados virão do manual do fabricante escolhido (a definir) e da ABNT NBR 15758-2.

Decisões e pendências

Decidido em 30/09/2026

- Cortineiros com vão livre de 20 cm; comprimentos gerais do DWG.
- Rasgo com luz para baixo, reforçando a iluminação geral.
- Garagem, varanda e beirais sem forro (revestimento a detalhar).
- Luminárias sem locação na planta de forro.
- Fita LED, Tuboled e cortina definidos depois, com os fornecedores.

Aguardando aprovação

- RU na cozinha e na A.S.; ST nos secos.
- Tabica perimetral (D1).
- Dimensões e posição do rasgo (12 cm, a 15 cm da parede, 8,20 m).
- Testeira, fonte na testeira e driver no vão (prancha D2).
- Fundos pintados, cantoneiras, alçapão AL1, fixações D3–D6.

A definir

- Fabricante de referência e seu manual técnico.
- Box até o teto? Exaustão nos banhos?
- Modelos de luminárias (fichas técnicas) e do cassete E1.
- CAU da Isadora Ferrari: A263982-8 (iluminação) × A269382-8 (esquadrias).
- Altura da J01: 2,50 m (esquadrias) × 2,00 m (DWG).

NORMAS E REFERÊNCIAS

ABNT NBR 15758-2 (forros em chapas de gesso para drywall) · ABNT NBR 14715-1 (chapas de gesso) · ABNT NBR 15217 (perfis de aço) · manual técnico do fabricante escolhido · cadernos de iluminação 02/04, tomadas 01/04, ar-condicionado 02/02, esquadrias e hidráulica · DWG “Projeto Ivan e Ana R01”.

Quantitativos

AMBIENTE	PLACA	ÁREA m²	PERÍM. m
Banho Suite Master	RU	6,83	10,9
Closet	ST	12,25	14,0
Suite Master	ST	15,75	16,3
Suite 2	ST	12,30	14,2
Banho Suite 2	RU	4,20	8,6
Banho Suite 1	RU	4,20	8,6
Suite 1	ST	12,30	14,2
Circulação	ST	12,85	20,6
Home Office	ST	7,26	11,0
Banho 4	RU	4,62	9,4
Cozinha	RU · prop.	17,85	16,9
A.S.	RU · prop.	5,50	9,5
Despensa	ST	2,40	6,4
Estar / Jantar	ST	41,00	26,5
Total ST		116,11	
Total RU (banhos)		19,85	
Total RU proposta (coz. + A.S.)		23,35	
Tabica (perímetros)			≈ 187,2
Cortineiros CT1 + CT2	20 cm		15,00
Rasgo RG1	12 cm		8,20

Áreas do DWG (planta de forro). Perímetros pelas faces internas. Referência para orçamento: sem perdas, testeiras e recortes. Conferir em obra.

Notas de execução

Antes de começar

- Conferir todas as medidas e níveis no local; marcar o nível do forro nas paredes.
- Concluir e testar elétrica, ar-condicionado (linhas e dreno), hidráulica e coifa no entreforro.
- Marcar na laje as linhas dos cortineiros (20 cm da parede acabada) e do rasgo.

Montagem

- Estrutura, pendurais, fixações e espaçamentos conforme manual do fabricante e NBR 15758-2.
- Nenhuma carga pendurada só na placa: cassete, pendentes e peças pesadas na laje ou na estrutura (D3, D5, D6).
- Recortes de luminárias com a peça ou o gabarito na mão; conferir a altura de embutimento (entreforro de 15 cm).

Cortineiros e rasgo

- Vão livre de 20 cm contínuo, sem pendural ou perfil dentro do vão.
- Fixar trilho e suportes de luz antes de fechar; driver acessível pelo vão.
- Arestas com cantoneira, retas e contínuas; fundo pintado de branco fosco.

Banhos

- Placa RU, massa e fita para áreas úmidas; pintura própria para áreas úmidas.
- RU não é impermeável: sem contato direto com água; ambiente ventilado.

Acabamento

- Tabica em todo o perímetro; juntas tratadas, lixadas e pintadas sem marcas sob luz rasante (cortineiros).

QUADRO 3



duas
design
& arq

CARIMBO

PROJETO
Residência Ivan e Ana Neris
Nova Odessa – SP

RESPONSÁVEIS TÉCNICAS
Lidiane Barbosa · CAU A290220-6
Isadora Ferrari · CAU A263982-8


PLANTA
Materiais e notas

ESCALA
sem escala

DATA
30/09/2026

PRANCHA
06/06

REVISÃO
R01

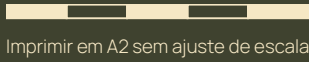

Imprimir em A2 sem ajuste de escala