


01 Planta de pontos hidráulicos

Escala 1:100 · plotagem em A2 · posições conforme Planta Pontos Hidráulicos (29/09/2026)

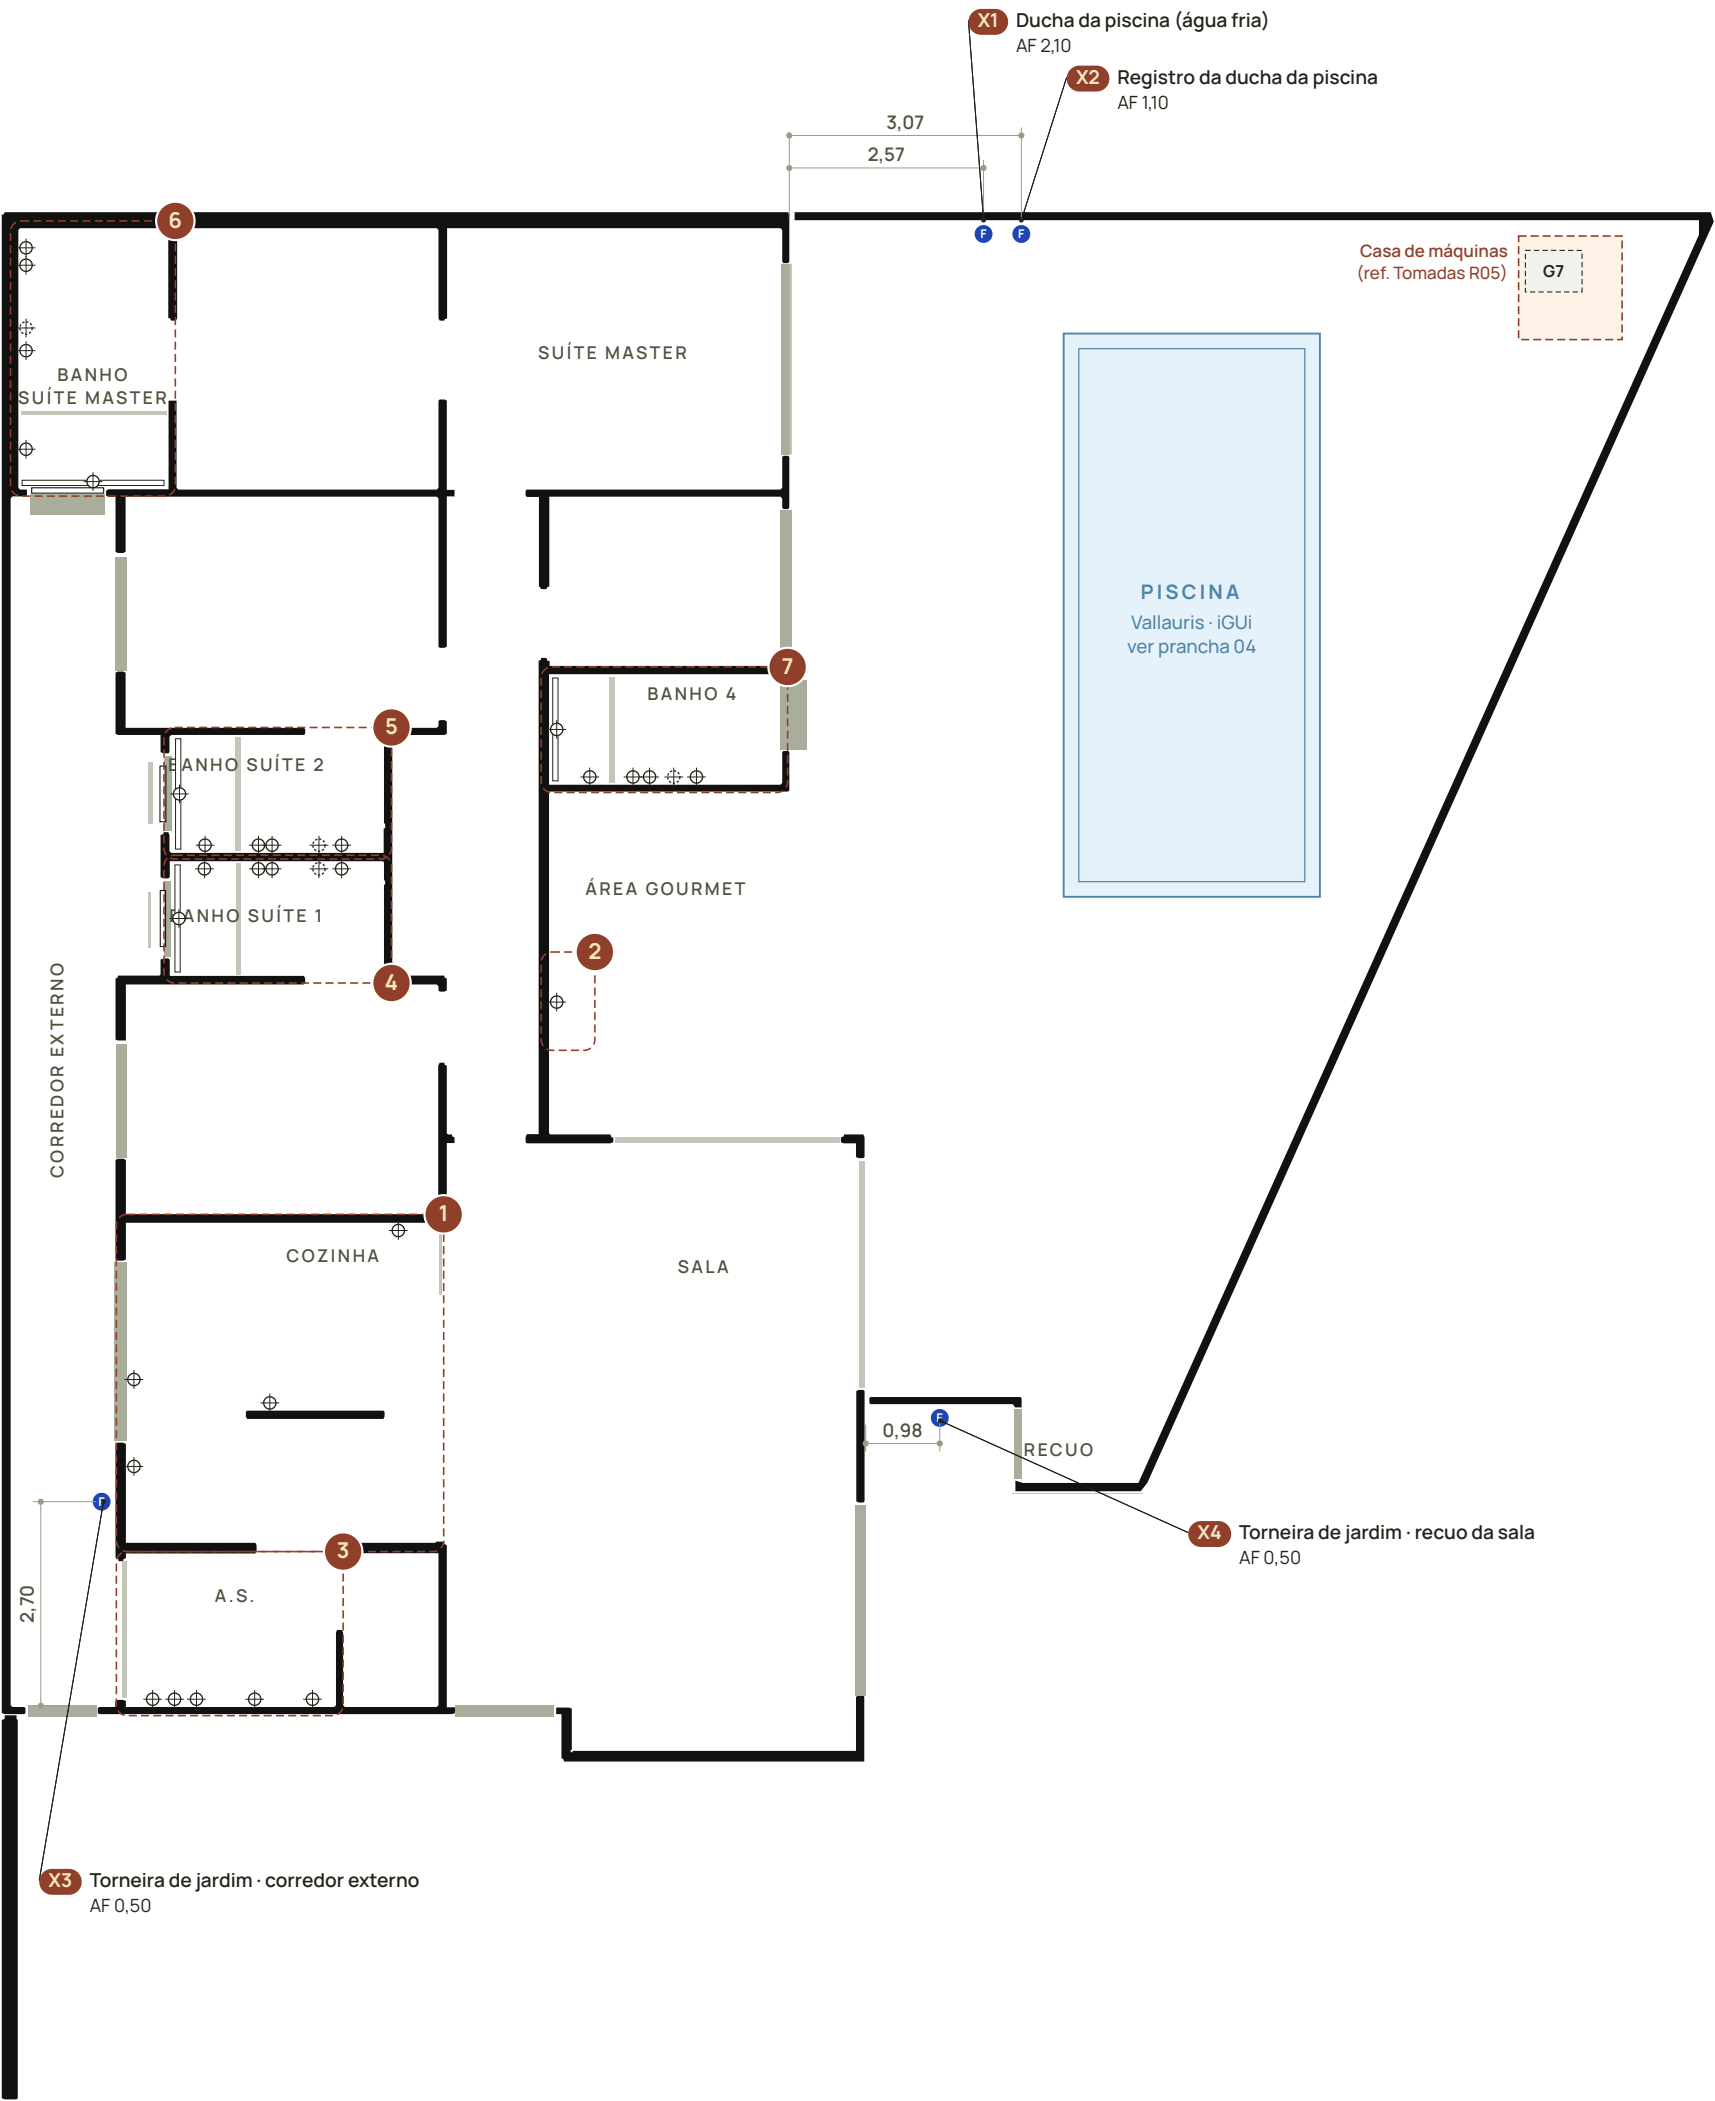

Pontos por ambiente

QUADRO 1

Nº	AMBIENTE · PONTOS	PRANCHA
1	Cozinha C1 a C4 · filtro, cuba, geladeira e lava-louças (mureta)	02
2	Área Gourmet G1 · cuba com misturador	02
3	A.S. · Área de serviço L1 a L5 · torneiras e esgoto do tanque, máquina, tanquinho	02
4	Banho Suíte 1 B1.1 a B1.6 · chuveiro, ducha higiênica, bacia, cuba, registro, ralo	03
5	Banho Suíte 2 B2.1 a B2.6 · espelhado em relação ao Banho Suíte 1	03
6	Banho Suíte Master BM.1 a BM.6 · chuveiro, ducha higiênica, bacia, cuba, registro, ralo	03
7	Banho 4 B4.1 a B4.6 · chuveiro, ducha, bacia, cuba de sobrepor, registro, ralo	03
8	Piscina Ducha e registro (X1, X2), skimmer, retorno, reposição, ladrão, dreno	04

Planta: selos em terracota indicam a ampliação de cada ambiente; o círculo com cruz marca o eixo de cada ponto. Pontos externos X1 a X4 cotados nesta prancha (Quadro 1A).

Pontos externos

QUADRO 1A

Nº	PONTO · POSIÇÃO	ALTURA
X1	Ducha da piscina (água fria) 2,57 da face externa da parede da Suíte Master · no muro.	2,10 m
X2	Registro da ducha da piscina 3,07 da face externa da parede da Suíte Master · no muro.	1,10 m
X3	Torneira de jardim · corredor externo 2,70 do alinhamento do portão · face externa da parede da cozinha.	0,50 m
X4	Torneira de jardim · recuo da sala 0,98 da face externa da parede da sala.	0,50 m

Ducha de água fria junto à piscina (kit chuveirão só água fria): saída 2,10 e registro 1,10, confirmados em 02/10/2026.

Fontes das alturas

QUADRO 1B

- C Caderno Hidráulica Detalhe · Rev. 02 · 24/09/2026
- D Definição do cliente · 30/09 e 02/10/2026
- P Padrão do escritório (R02) · confirmado em 30/09/2026

Cada altura nos quadros das pranchas 02 a 04 traz a letra da sua fonte. Posições: Planta Pontos Hidráulicos (29/09/2026).

R02 (02/10/2026): bacias Roca ONA com caixa acoplada (sem válvula de descarga); lavatórios e gourmet com misturador AF/AQ; lava-louças na face da mureta; nomes dos ambientes conforme a elétrica; CAU corrigido. R03: água fria do L2 eliminada. R04: L2 só com o esgoto do tanque; ralos lineares dos boxes (B1.6, B2.6, BM.6, B4.6).

Legenda

QUADRO 2

ⓘ	Água fria	⊕	Eixo de ponto (planta geral)
⓪	Água quente	Ⓡ	Ponto com eixo sem cota
ⓔ	Esgoto	B1.3	Código do ponto
Ⓡ	Registro geral	4	Ampliação (Quadro 1)
Ⓢ	Saída de chuveiro (misturada)	1.00	Cota em metros
		█	Alvenaria
		█	Janela / vidro
		▤	Ralo linear (indicativo)

Letra no círculo = serviço. Altura do piso acabado ao eixo do ponto.

Observações técnicas

QUADRO 3

1. Escopo

Prancha de localização de pontos. Não é projeto de dimensionamento: diâmetros, trajetetos, declividades, ventilação, caixas e ramais seguem o projeto hidrossanitário do responsável técnico.

2. Posições

Cotas em metros, a partir da face da parede indicada em cada ponto. Os pontos dos ambientes estão cotados nas ampliações (pranchas 02 e 03); os externos, nesta prancha.

3. Alturas

Do piso acabado ao eixo do ponto. A fonte de cada valor está no Quadro 1B.

4. Chuveiros

Kit Deca Acqua Plus com misturador de duas alavancas (água quente e fria); registros já executados. Sem chuveiro elétrico.

5. Registro geral

Dentro do armário da bancada de cada banheiro, a 0,55 m. Eixo sem cota: definir com a marcenaria.

6. Compatibilização

Pontos elétricos conforme a prancha de Tomadas R05. Manter no mínimo 0,30 m entre tomadas e pontos de água e esgoto. Conferir as medidas no local antes de fechar as paredes.

7. Normas

NBR 5626 (água fria e água quente), NBR 8160 (esgoto sanitário) e NBR 10339 (piscinas).



CARIMBO

PROJETO
Residência Ivan e Ana Neris
Nova Odessa – SP

RESPONSÁVEIS TÉCNICAS
Lidiane Barbosa · CAU A290220-6
Isadora Ferrari · CAU A263982-8

PLANTA
Pontos hidráulicos · geral

ESCALA
1:100 · folha A2

DATA
02/10/2026

PRANCHA
01/04


REVISÃO
R04

0 — 5 m

Conferir as medidas no local


1 Cozinha

Escala 1:25 · pontos C1 a C4

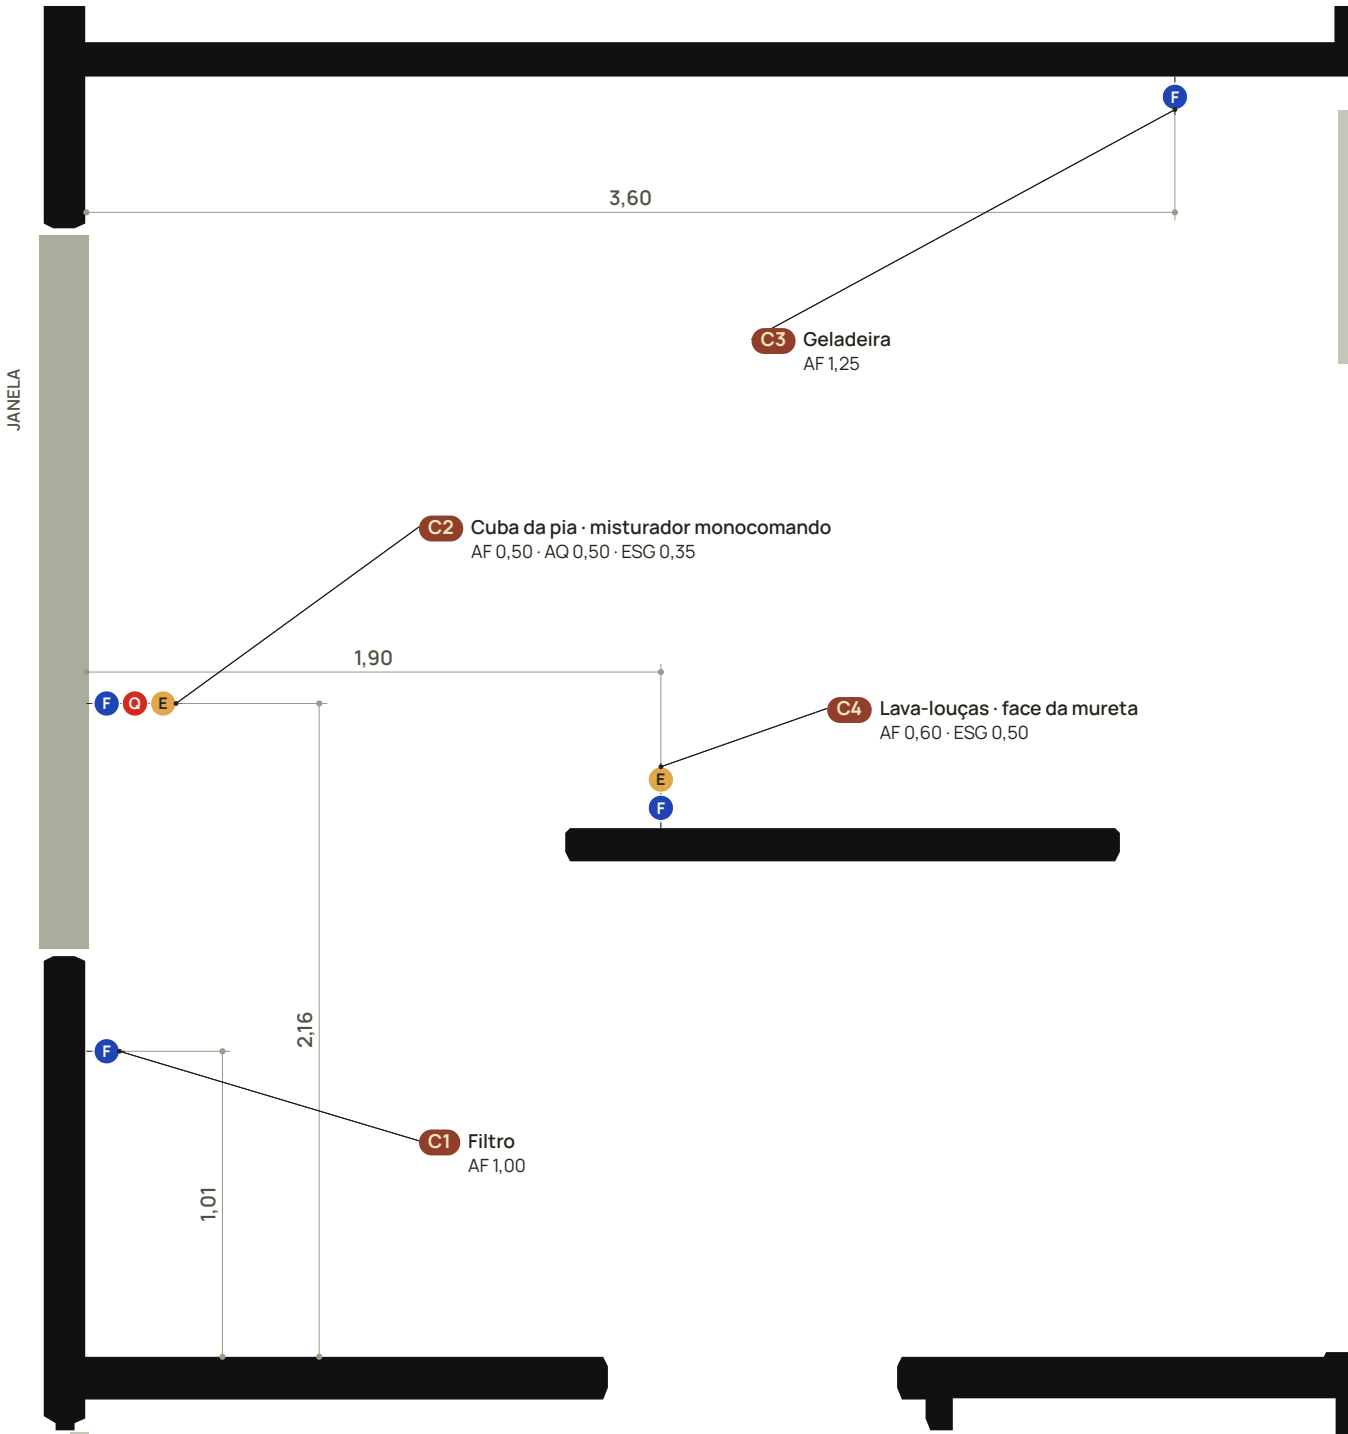


2 Área Gourmet

Escala 1:25 · ponto G1

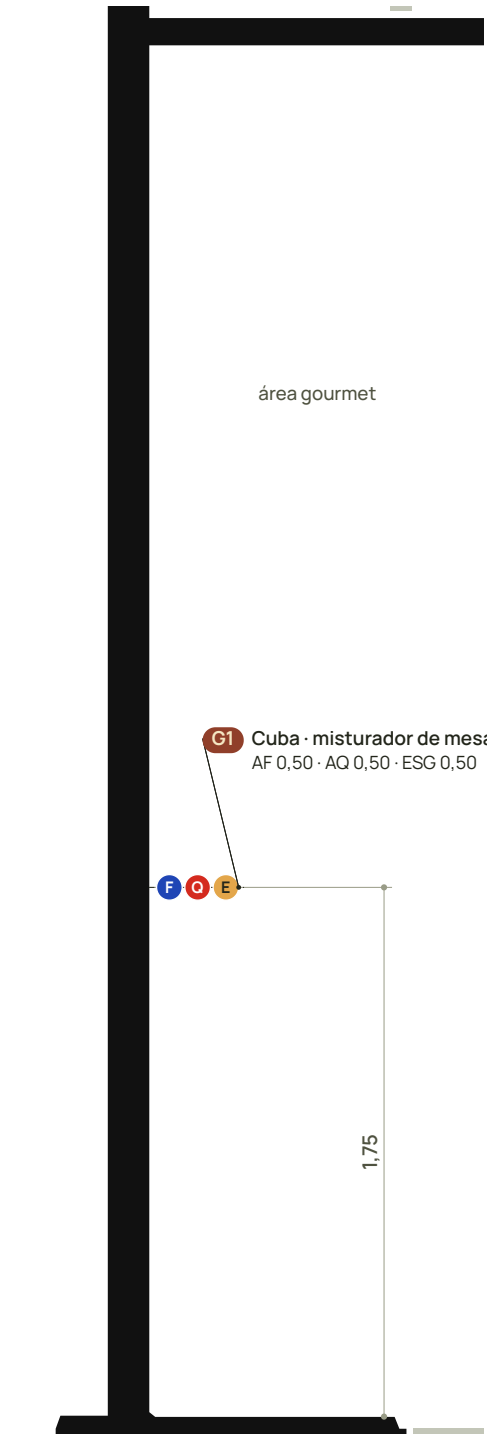


3 A.S. · Área de serviço

Escala 1:25 · pontos L1 a L5

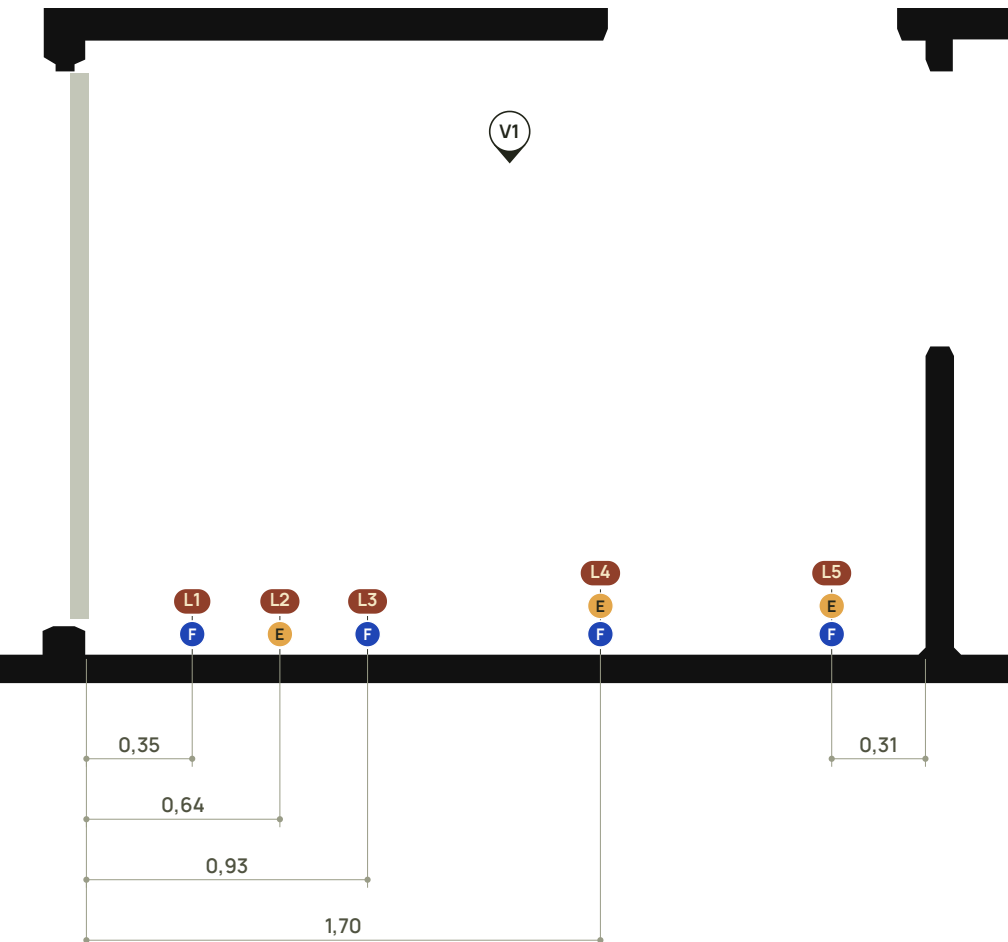

V1 Vista da parede do tanque

Escala 1:25 · do interior (espelhada em relação à planta)

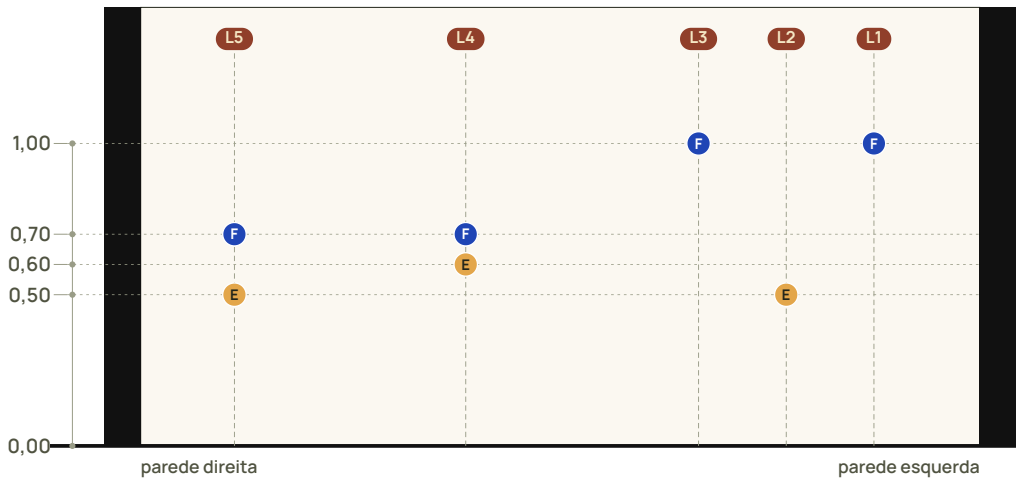

02 Ampliações · cozinha · gourmet · lavanderia

Escala 1:25 · plotagem em A2 · cotas em metros a partir da face da parede indicada



Pontos e alturas

QUADRO 1

CÓD.	PEÇA · EIXO	ALTURAS (m) · FONTE
COZINHA		
C1	Filtro 1,01 da parede inferior P 1,00 ^C	
C2	Cuba da pia · misturador monocomando 2,16 da parede inferior P 0,50 ^D O 0,50 ^C E 0,35 ^C	
C3	Geladeira 3,60 da parede da janela (esquerda) P 1,25 ^C	
C4	Lava-louças · face da mureta 1,90 da parede da janela · na face norte da mureta do balcão (≈0,32 da ponta) P 0,60 ^C E 0,50 ^P	

ÁREA GOURMET

G1	Cuba · misturador de mesa 1,75 da parede inferior (2,80 até a superior, conforme caderno) P 0,50 ^D O 0,50 ^C E 0,50 ^P
----	---

A. S. · ÁREA DE SERVIÇO

L1	Torneira de parede · tanque 0,35 da parede esquerda P 1,00 ^P
L2	Esgoto do tanque 0,64 da parede esquerda (centro do tanque, meio das torneiras) E 0,50 ^P
L3	Torneira de parede · tanque 0,93 da parede esquerda P 1,00 ^P
L4	Máquina de lavar roupas 1,70 da parede esquerda P 0,70 ^C E 0,60 ^P
L5	Tanquinho 0,31 da parede direita P 0,70 ^C E 0,50 ^P

Revisões sobre o caderno

QUADRO 1A

PEÇA	CADERNO	PLANTA 29/09
COZINHA		
Filtro	1,00	1,01
Cuba	2,15	2,16
Lava-louças	0,40 da borda da ilha	1,90 · 2,30 das paredes

A. S.

Torneira · tanque	0,40	0,35
Torneira · tanque	1,00	0,93
Máquina de lavar	1,80	1,70
Tanquinho	2,55 (esq.)	0,31 (dir.)

Eixos em metros. Vale a Planta Pontos Hidráulicos (decisão do cliente, 30/09/2026).

Legenda

QUADRO 2

F	Água fria	R	Ponto com eixo sem cota
O	Água quente	B1.3	Código do ponto
E	Esgoto	4	Ampliação (Quadro 1)
R	Registro geral	1,00	Cota em metros
S	Saída de chuveiro (misturada)		Alvenaria
			Janela / vidro
			Ralo linear (indicativo)

Letra no círculo = serviço. Altura do piso acabado ao eixo do ponto.

Observações técnicas

QUADRO 3

1. Cozinha

Filtro e cuba na parede da janela. Geladeira a 3,60 da parede da janela, na parede superior. Lava-louças: água e esgoto saem pela face norte da mureta do balcão (1,83 × 0,11 m), a 1,90 da parede da janela (R02).

2. Lava-louças

Tomada da face do balcão afastada no mínimo 0,30 m dos pontos de água e esgoto (Tomadas R05, item 13.5).

3. Área Gourmet

Cuba a 1,75 da parede inferior; fecha com os 2,80 até a parede superior do caderno. Misturador Deca Flex Plus (AF/AQ).

4. A.S.

Posições conforme a planta de 29/09. Tanque único l.Corso: L1 e L3 ficam por ora; uma será vedada depois. L2 só com o esgoto do tanque (R04; a água fria saiu na R03). Tanquinho cotado pela parede direita.

5. Alturas

Do piso acabado ao eixo. A letra ao lado de cada altura indica a fonte (Quadro 1B da prancha 01).

6. Escopo

Localização de pontos. Diâmetros, trajetos e declividades: projeto hidrossanitário.



CARIMBO

PROJETO
Residência Ivan e Ana Neris
Nova Odessa – SP

RESPONSÁVEIS TÉCNICAS
Lidiane Barbosa · CAU A290220-6
Isadora Ferrari · CAU A263982-8

PLANTA
Pontos hidráulicos · ampliações

ESCALA
1:25 · folha A2

DATA
02/10/2026

PRANCHA
02/04


REVISÃO
R04

0 – 2 m

Conferir as medidas no local


6 Banho Suíte Master

Escala 1:25 · pontos BM.1 a BM.6

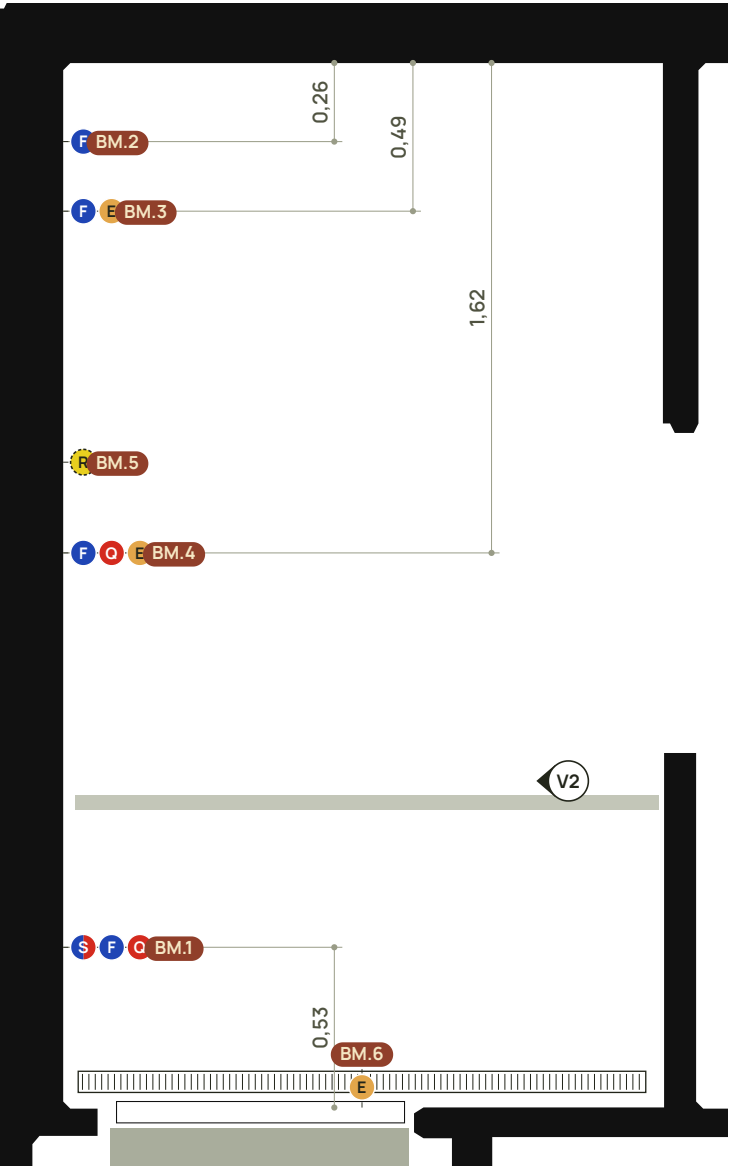


4 Banhos Suíte 1 e Suíte 2

Escala 1:25 · pontos B1.1 a B1.6 e B2.1 a B2.6 (espelhado)

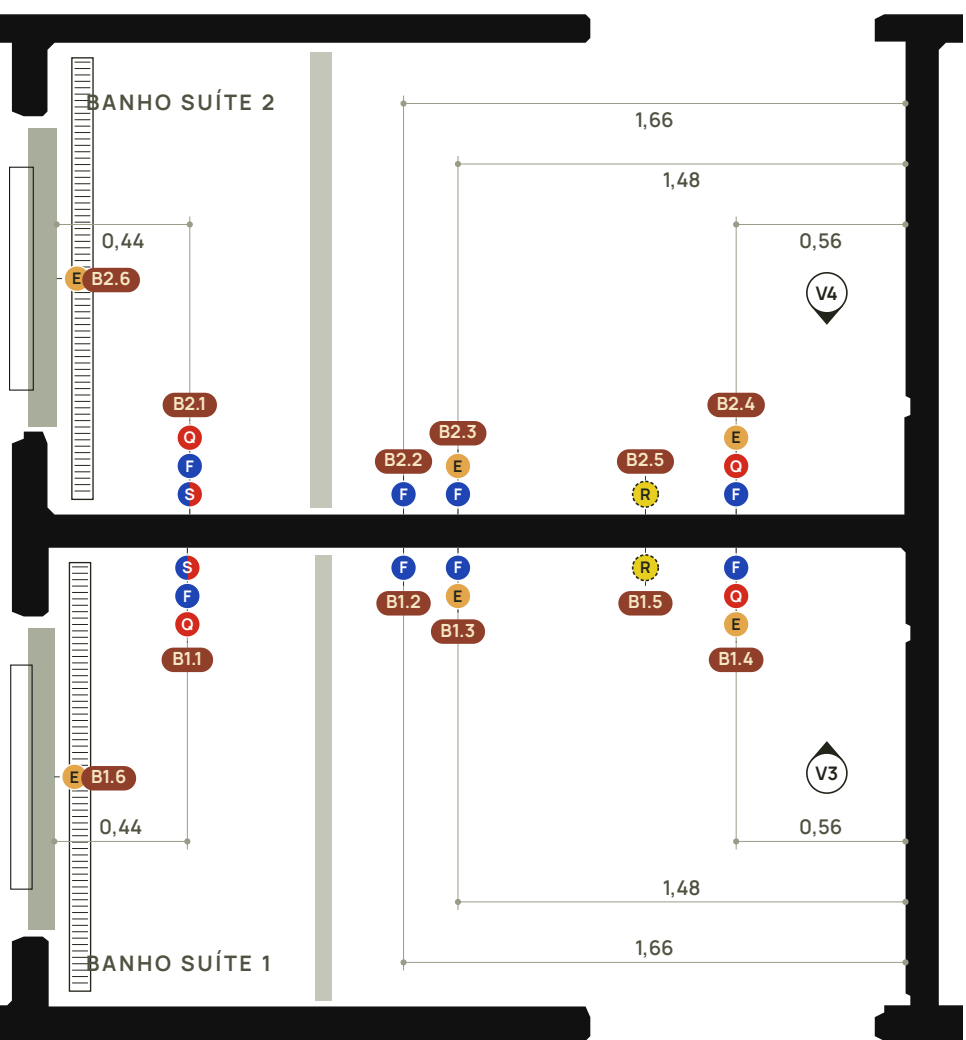


7 Banho 4

Escala 1:25 · pontos B4.1 a B4.6

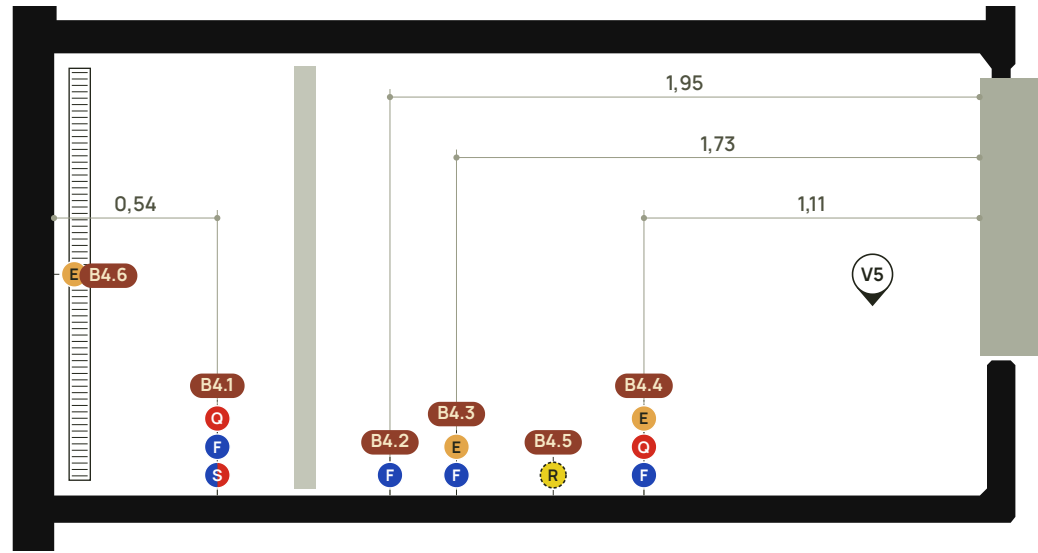

V2 Banho Suíte Master

Escala 1:50 · do interior · alturas do piso acabado

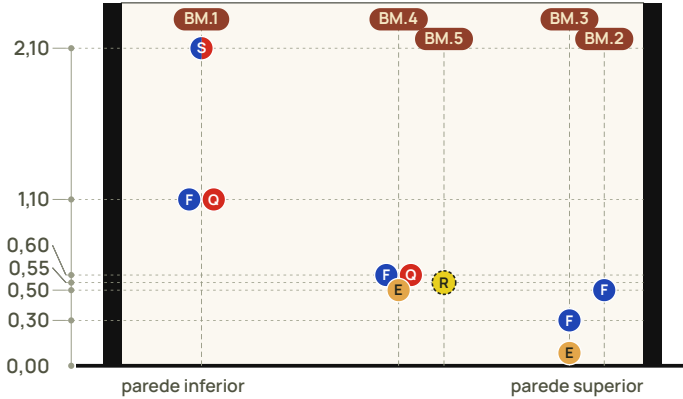


V3 Banho Suíte 1

Escala 1:50 · do interior · alturas do piso acabado




V4 Banho Suíte 2

Escala 1:50 · do interior · alturas do piso acabado

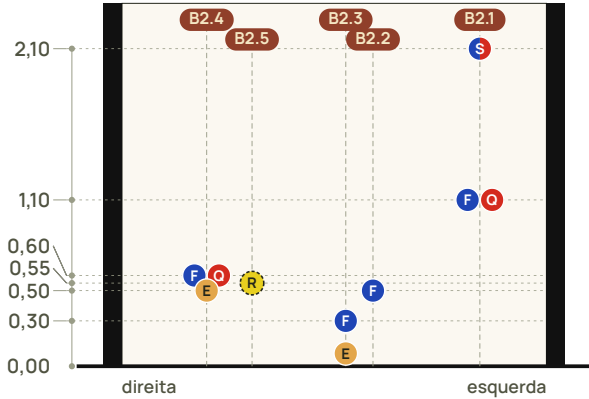

V5 Banho 4

Escala 1:50 · do interior · alturas do piso acabado

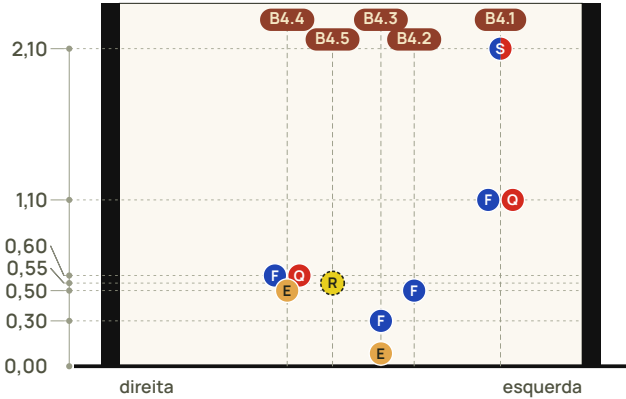

03 Ampliações · banheiros

Plantas 1:25 · vistas 1:50 · plotagem em A2 · cotas em metros a partir da face da parede indicada



Pontos e alturas

QUADRO 1

CÓD. PEÇA · EIXO ALTURAS (m) · FONTE

BANHO SUÍTE 1

- B1.1 Chuveiro
0,44 da parede esquerda
S 2,10^C F 1,10^C O 1,10^C
- B1.2 Ducha higiênica
1,66 da parede direita
F 0,50^P
- B1.3 Bacia sanitária
1,48 da parede direita
F 0,30^P E piso^C
- B1.4 Cuba · misturador de mesa
0,56 da parede direita
F 0,60^C O 0,60^D E 0,50^P
- B1.5 Registro geral
sem cota · dentro do armário
R 0,55^P
- B1.6 Ralo linear do box
junto à parede do fundo do box · comprimento a definir
E piso^D

BANHO SUÍTE 2 (ESPELHADO)

- B2.1 Chuveiro
0,44 da parede esquerda
S 2,10^C F 1,10^C O 1,10^C
- B2.2 Ducha higiênica
1,66 da parede direita
F 0,50^P
- B2.3 Bacia sanitária
1,48 da parede direita
F 0,30^P E piso^C
- B2.4 Cuba · misturador de mesa
0,56 da parede direita
F 0,60^C O 0,60^D E 0,50^P
- B2.5 Registro geral
sem cota · dentro do armário
R 0,55^P
- B2.6 Ralo linear do box
junto à parede do fundo do box · comprimento a definir
E piso^D

BANHO SUÍTE MASTER

- BM.1 Chuveiro
0,53 da parede inferior
S 2,10^C F 1,10^C O 1,10^C
- BM.2 Ducha higiênica
0,26 da parede superior
F 0,50^P
- BM.3 Bacia sanitária
0,49 da parede superior
F 0,30^P E piso^C
- BM.4 Cuba · misturador de mesa
1,62 da parede superior
F 0,60^C O 0,60^D E 0,50^P
- BM.5 Registro geral
sem cota · dentro do armário
R 0,55^P
- BM.6 Ralo linear do box
junto à parede do fundo do box · comprimento a definir
E piso^D

BANHO 4

- B4.1 Chuveiro
0,54 da parede esquerda
S 2,10^C F 1,10^C O 1,10^C
- B4.2 Ducha higiênica
1,95 da parede direita
F 0,50^P
- B4.3 Bacia sanitária
1,73 da parede direita
F 0,30^P E piso^C
- B4.4 Cuba de sobrepor · misturador bica alta
1,11 da parede direita
F 0,60^D O 0,60^D E 0,50^P
- B4.5 Registro geral
sem cota · dentro do armário
R 0,55^C
- B4.6 Ralo linear do box
junto à parede do fundo do box · comprimento a definir
E piso^D

Legenda

QUADRO 2

- F Água fria
O Água quente
E Esgoto
R Registro geral
S Saída de chuveiro (misturada)
- R Ponto com eixo sem cota
B1.3 Código do ponto
4 Ampliação (Quadro 1)
1,00 Cota em metros
Alvenaria
Janela / vidro
Ralo linear (indicativo)

Letra no círculo = serviço. Altura do piso acabado ao eixo do ponto.

Observações técnicas

QUADRO 3

1. Chuveiro

Kit Acqua Plus: saída a 2,10; misturador de duas alavancas (AF/AQ) a 1,10, já executado: afastamento a medir em obra.

2. Bacia

Roca ONA com caixa acoplada: alimentação a 0,30 (conferir na ficha da Roca) e esgoto no piso. Sem válvula de descarga.

3. Registro geral

A 0,55, dentro do armário da bancada. Eixo sem cota (marcador tracejado): definir com a marcenaria.

4. Referências

Banhos Suíte 1, Suíte 2 e Banho 4: chuveiro pela parede esquerda, demais peças pela direita. Banho Suite Master: peças pela parede superior, chuveiro pela inferior. Vistas esquemáticas: eixos e alturas, sem louças.

Revisões sobre o caderno

QUADRO 3 A

PEÇA	CADERNO	PLANTA
Banhos Suíte 1 e 2		
Ducha higiênica	1,20 (esq.)	1,66 (dir.)
Bacia	1,40 (esq.)	1,48 (dir.)
Cuba	2,35 (esq.)	0,56 (dir.)
Chuveiro	0,45	0,44
Banho Suíte Master		
Ducha higiênica	0,25	0,26
Bacia	0,45	0,49
Cuba	1,60	1,62
Chuveiro (da inferior)	0,55	0,53
Banho 4		
Chuveiro	0,55	0,54
Bacia (da dir.)	1,75	1,73
Torneira (da dir.)	1,15	1,11

Vale a planta de 29/09. Nos Banhos Suíte 1/2 a soma das cotas do caderno (2,90) excedia a largura do ambiente.



CARIMBO

PROJETO
Residência Ivan e Ana Neris
Nova Odessa – SP

RESPONSÁVEIS TÉCNICAS
Lidiane Barbosa · CAU A290220-6
Isadora Ferrari · CAU A263982-8

PLANTA
Pontos hidráulicos · banheiros

ESCALA
1:25 e 1:50 · folha A2

0 – 2 m (1:25)

Conferir as medidas no local


DATA
02/10/2026

PRANCHA
03/04

REVISÃO
R04


1 Implantação da piscina

Escala 1:100 · * cotas medidas na planta de layout (01/05/2026) · a conferir

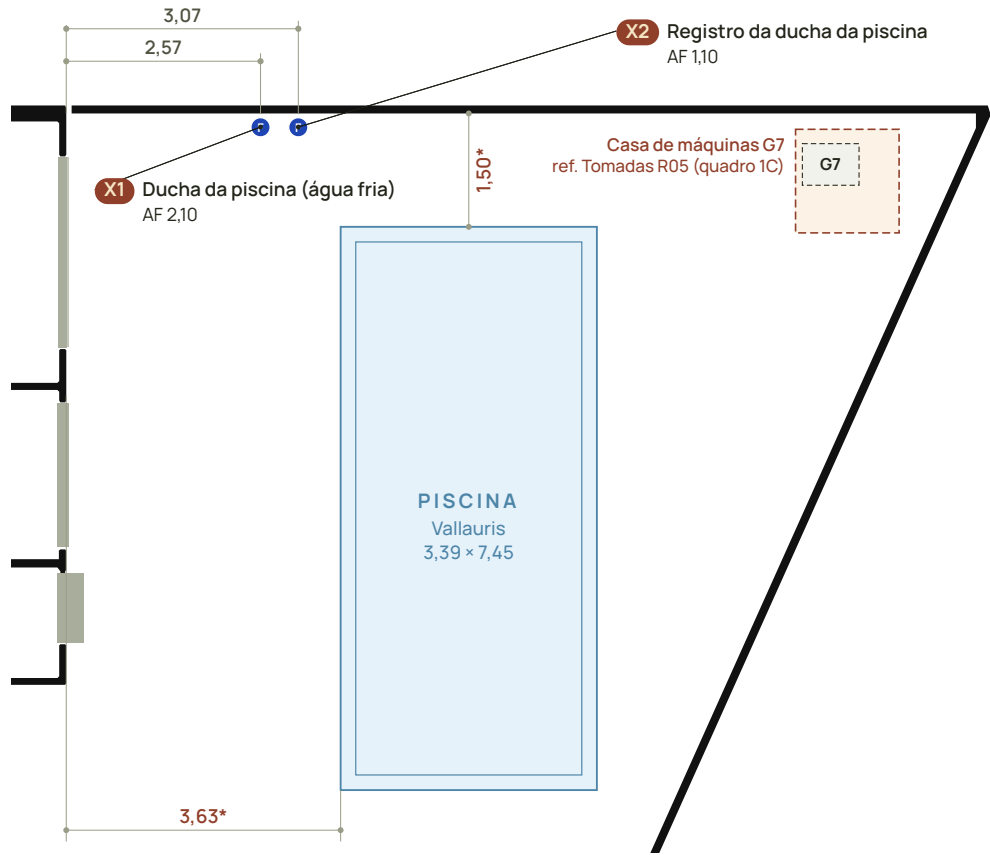


3 Modelo Vallauris · planta

Escala 1:50 · redesenhado do desenho técnico iGui (01/01)

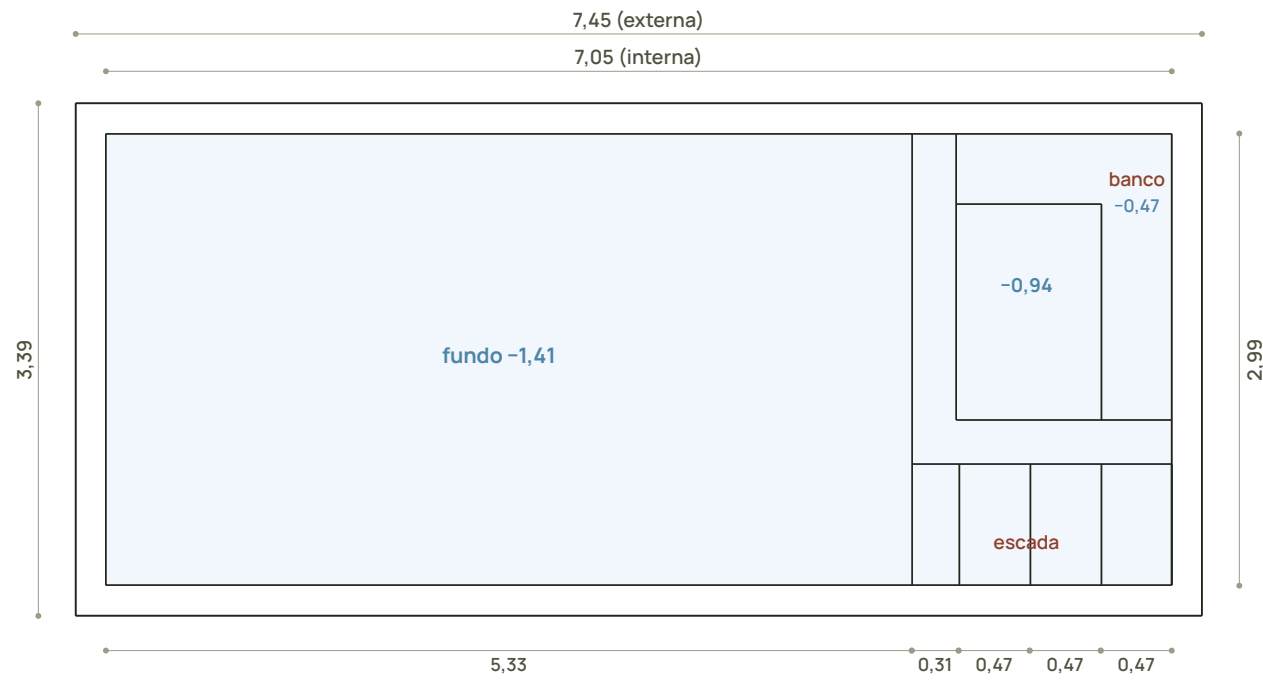


4 Corte longitudinal

Escala 1:50 · iGui

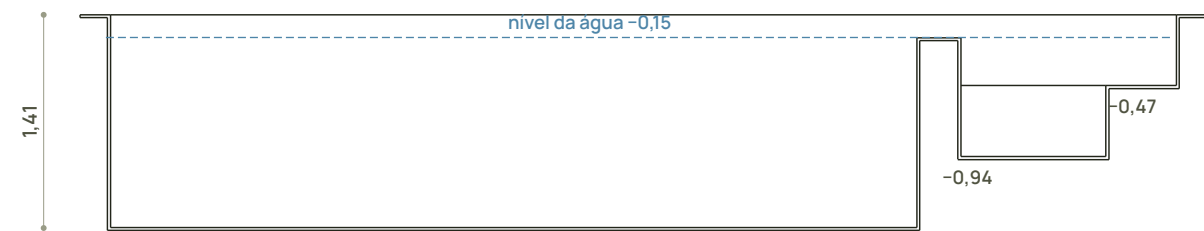

5 Corte transversal

Escala 1:50 · iGui

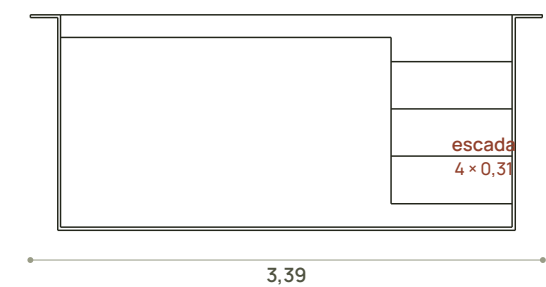


04 Piscina Vallauris · pontos hidráulicos

Implantação 1:100 · modelo e cortes 1:50 · plotagem em A2



2 Esquema dos pontos

Sem escala · funcional · não indica trajeto nem diâmetro

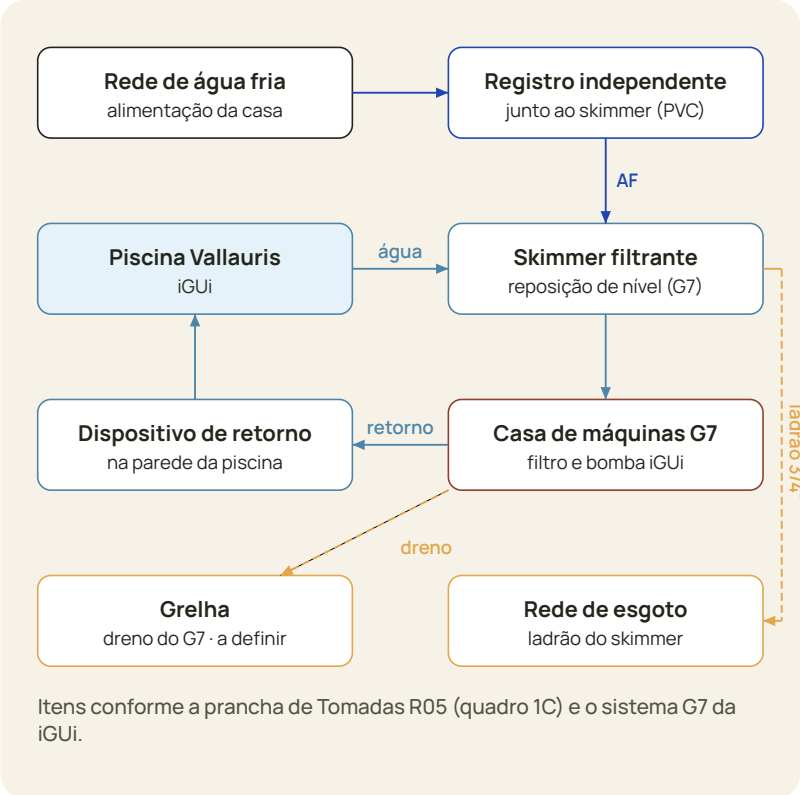

Pontos da piscina

QUADRO 1

Nº	ITEM · ORIGEM DA INFORMAÇÃO	POSIÇÃO
X1	Ducha de água fria Saída a 2,10 m* · 2,57 da face externa da Suíte Master, no muro. Planta de pontos (29/09).	cotada
X2	Registro da ducha A 1,10 m* · 3,07 da mesma face, no muro. Planta de pontos (29/09).	cotada
P1	Reposição de água (AF) Registro independente junto ao skimmer, em PVC (Tomadas R05, quadro 1C).	iGui
P2	Skimmer filtrante Sistema G7 da iGui.	iGui
P3	Dispositivo de retorno Sistema G7 da iGui; ligação à casa de máquinas.	iGui
P4	Ladrão 3/4" do skimmer Para a rede de esgoto (Tomadas R05, quadro 1C).	iGui
P5	Dreno do G7 Para a grelha (Tomadas R05, quadro 1C). Grelha não localizada nos arquivos.	a definir
G7	Casa de máquinas Canto superior do lote, junto ao muro, como na prancha de Tomadas R05.	ref. elétrica

* Alturas da ducha adotadas do padrão do chuveiro: confirmar. Pontos P1 a P5 sem cota: posição, trajeto e diâmetro conforme a instaladora iGui e o projeto hidrossanitário.

Modelo Vallauris

QUADRO 1A

Fabricante	iGui · desenho técnico Vallauris 01/01
Medidas externas	7,45 × 3,39 m (borda de 0,20)
Medidas internas	7,05 × 2,99 m
Profundidade	1,41 m no fundo
Plataforma	0,96 m a -0,94 m
Banco	0,47 m a -0,47 m
Escada	4 degraus de 0,31 m · largura 0,80 m
Nível da água	0,15 m abaixo da borda
Estrutura	Mão francesa ao longo da borda e reforços a cada 45 cm, em média (iGui)
Implantação	Borda externa a 3,63 m da fachada da Suíte Master e a 1,50 m do muro, medidas na planta de layout (01/05/2026) · a conferir
Orientação	Lado da escada e do banco a definir com a iGui

Legenda

QUADRO 2

Água fria	Ponto com eixo sem cota
Água quente	Código do ponto
Esgoto	Ampliação (Quadro 1)
Registro geral	Cota em metros
Saída de chuveiro (misturada)	Alvenaria
	Janela / vidro
	Ralo linear (indicativo)

Letra no círculo = serviço. Altura do piso acabado ao eixo do ponto.

Observações técnicas

QUADRO 3

1. Escopo

Localização dos pontos hidráulicos ligados à piscina. Instalação, tubulação e equipamentos conforme o manual da iGui e o projeto hidrossanitário.

2. Implantação

Posição da piscina medida graficamente na planta de layout (Rev. 01). Conferir no local e com o projeto de implantação antes da escavação.

3. Ducha

Ducha de água fria com registro próprio, no muro, entre a casa e a piscina.

4. Elétrica

Q.C. MAX, conduites e trocador de calor conforme a prancha de Tomadas R05 (quadro 1C). Equipotencialização da piscina conforme NBR 5410.

5. Normas

NBR 10339 (piscinas) e NBR 5626 (água fria e água quente).



CARIMBO

PROJETO
Residência Ivan e Ana Neris
Nova Odessa - SP

RESPONSÁVEIS TÉCNICAS
Lidiane Barbosa · CAU A290220-6
Isadora Ferrari · CAU A263982-8

PLANTA
Pontos hidráulicos · piscina

ESCALA
1:100 e 1:50 · folha A2

0 — 4 m (1:50)

Conferir as medidas no local

DATA
02/10/2026

PRANCHA
04/04

REVISÃO
R04