


Planta geral de pontos hidráulicos

Visão de conjunto · base de paredes: PROJETO IVAN E ANA - R01.dwg, camada PLANTA DE PISO

PLANTA GERAL · ESC 1/90

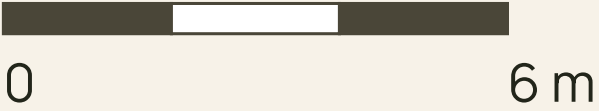

Índice de pranchas

01	Cozinha	4 pontos
02	Gourmet	1 pontos
03	Lavanderia	5 pontos
04	WC 01	7 pontos
05	WC 02	7 pontos
06	WC Suite Master	7 pontos
07	WC Externo	7 pontos

Esta planta geral tem finalidade de localização e coordenação entre ambientes (prumadas, shafts compartilhados). As cotas de execução de cada ponto estão nas pranchas 01 a 07, não nesta.

Observações técnicas

- Base de paredes e ambientes extraída do DWG "PROJETO IVAN E ANA - R01.dwg" (mesmo arquivo usado no Caderno de Detalhamento de Piso), camada geométrica "PLANTA DE PISO", em metros. Confirmado pelo cliente como planta-base (28/09/2026).
- O DWG NÃO contém pontos hidráulicos internos: as únicas camadas de água/esgoto do arquivo ("Esgoto", "AGUAS PLUVIAIS") estão na planta de implantação (ligação à rede pública), não na planta de piso. Os pontos aqui representados vêm do caderno hidráulico original e das propostas sinalizadas nas pranchas 01 a 07.
- Ambientes hachurados em tom mais escuro: os 7 ambientes com pontos hidráulicos detalhados neste caderno.
- Nomenclatura do DWG difere em alguns casos da adotada nas pranchas de detalhe (ex.: "Banheiro Casal" no DWG = "WC Suite Master" aqui; "Varanda Gourmet" no DWG = "Gourmet" aqui) – mantida a nomenclatura do caderno hidráulico original por decisão do cliente.

DUAS

design & arq

00/08

REVISÃO R01

PROJETO
Residência IC · Detalhamento de pontos hidráulicos

CLIENTES
Ivan e Carol

ENDEREÇO
Nova Odessa, SP

TIPO DE PLANTA
Planta geral de pontos hidráulicos

RESPONSÁVEIS TÉCNICOS (projeto de interiores)
Arq. Lidiane Barbosa · CAU A290220-6
Arq. Isadora Ferrari · CAU A269382-8

DATA
28/09/2026


ESCALA
1/90 (esquemático, reduzido para A2)

ORIGEM
Caderno Detalhamento Residencia IC - Hidraulica Detalhe, Rev. 02, 24/09/2026 + PROJETO IVAN E ANA - R01.dwg

CONFERIR AS MEDIDAS SINALIZADAS COMO PROPOSTA/PENDÊNCIA ANTES DE EXECUTAR - VÁLIDO EM A2 A 100%

Eixos verticais a partir da parede inferior (filtro). Geladeira a partir das paredes esquerda e direita. Lava-loucas a partir da borda da ilha (posicao da ilha ainda nao determinada - ver observacao).

PLANTA DE EIXOS HIDRÁULICOS · ESC 1/26

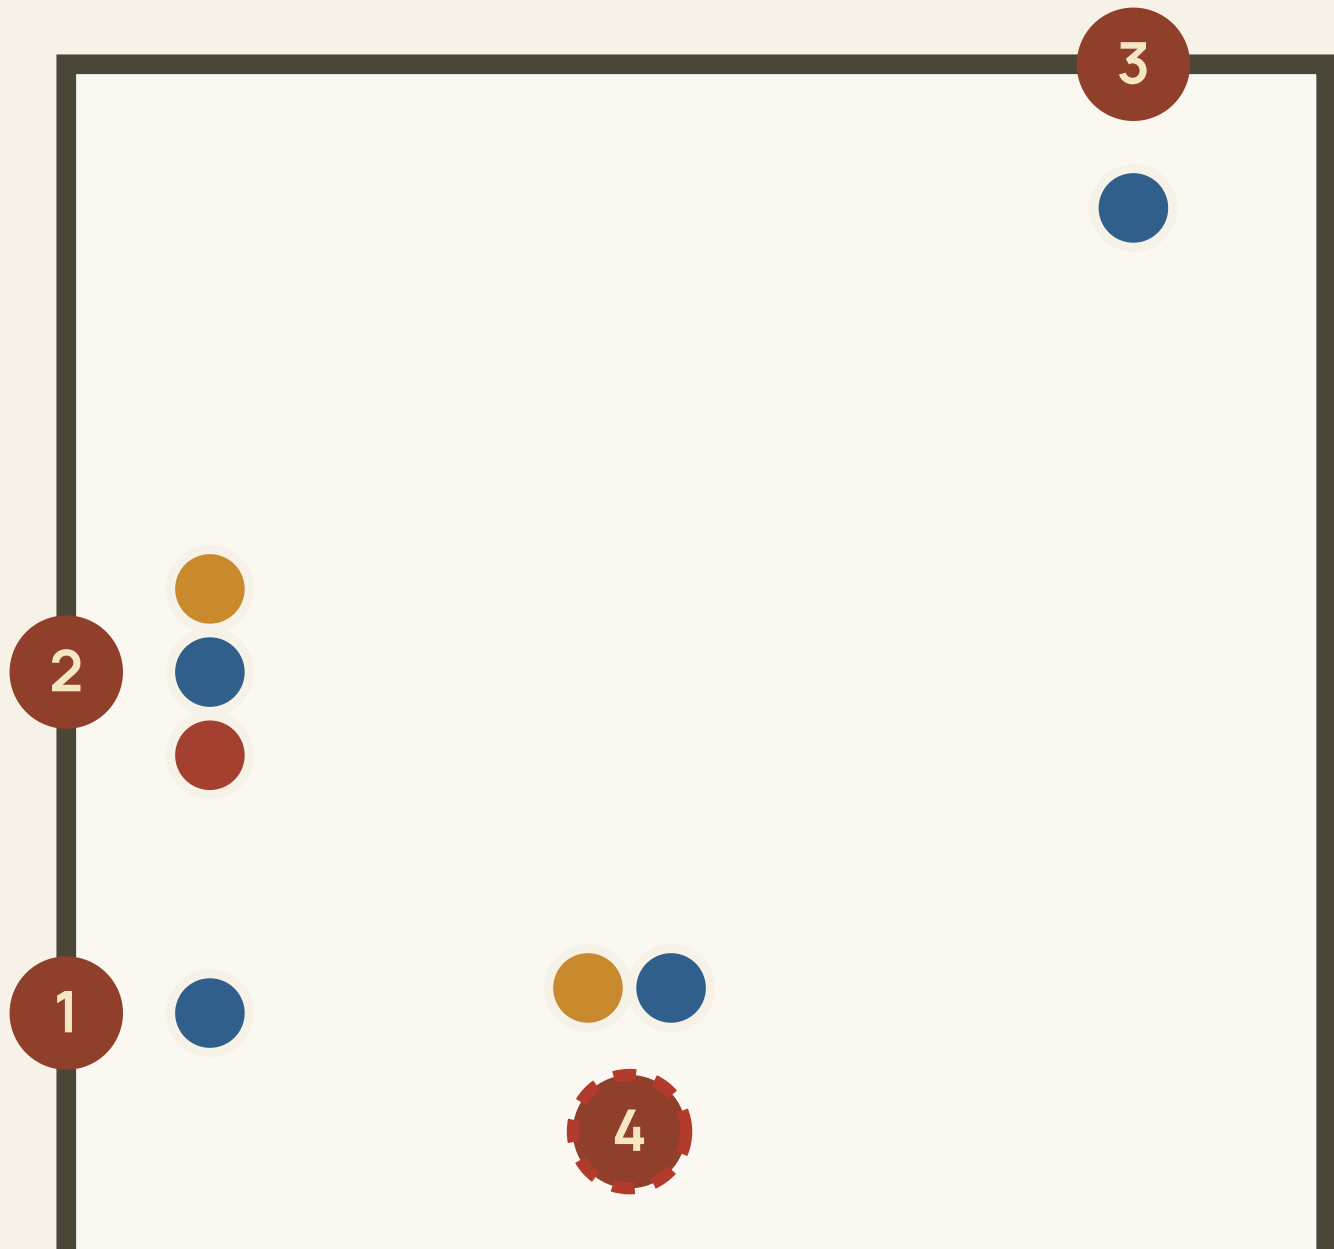

● A.F. 1,00 m

- **A.Q.** 0,50 m
- **A.F.** 0,50 m* *mesma linha do A.Q. confirmado*
- **ESG** 0,35 m

- A.F. 1,25 m

saida de sifao sob a cuba, pratica usual

Confirmado - dado do caderno original, Revisão 02.
Proposta - valor usual de mercado adotado por nós (não consta no original) – marcado com asterisco (*) no quadro de pontos, a validar com o responsável hidrossanitário.
Pendente - posição de projeto sem informação suficiente para propor – aguarda definição.

4 Normas de referencia: NBR 5626 (água fria), NBR 7198 (água quente) e NBR 8160 (esgoto sanitário).

01/08
REVISÃO R01

ORIGEM
Caderno Detalhamento Residencia IC - Hidraulica Detalhe, Rev. 02, 24/09/2026 + PROJETO IVAN E ANA - R01.dwg


CONFERIR AS MEDIDAS SINALIZADAS COMO PROPOSTA/PENDÊNCIA ANTES DE EXECUTAR - VÁLIDO EM A2 A 100%

Gourmet

Planta de eixos · pontos de água fria, água quente e esgoto

Parede superior (2,80) e parede inferior (1,75). Afastamento da parede esquerda NAO COTADO no caderno original.

PLANTA DE EIXOS HIDRÁULICOS · ESC 1/27

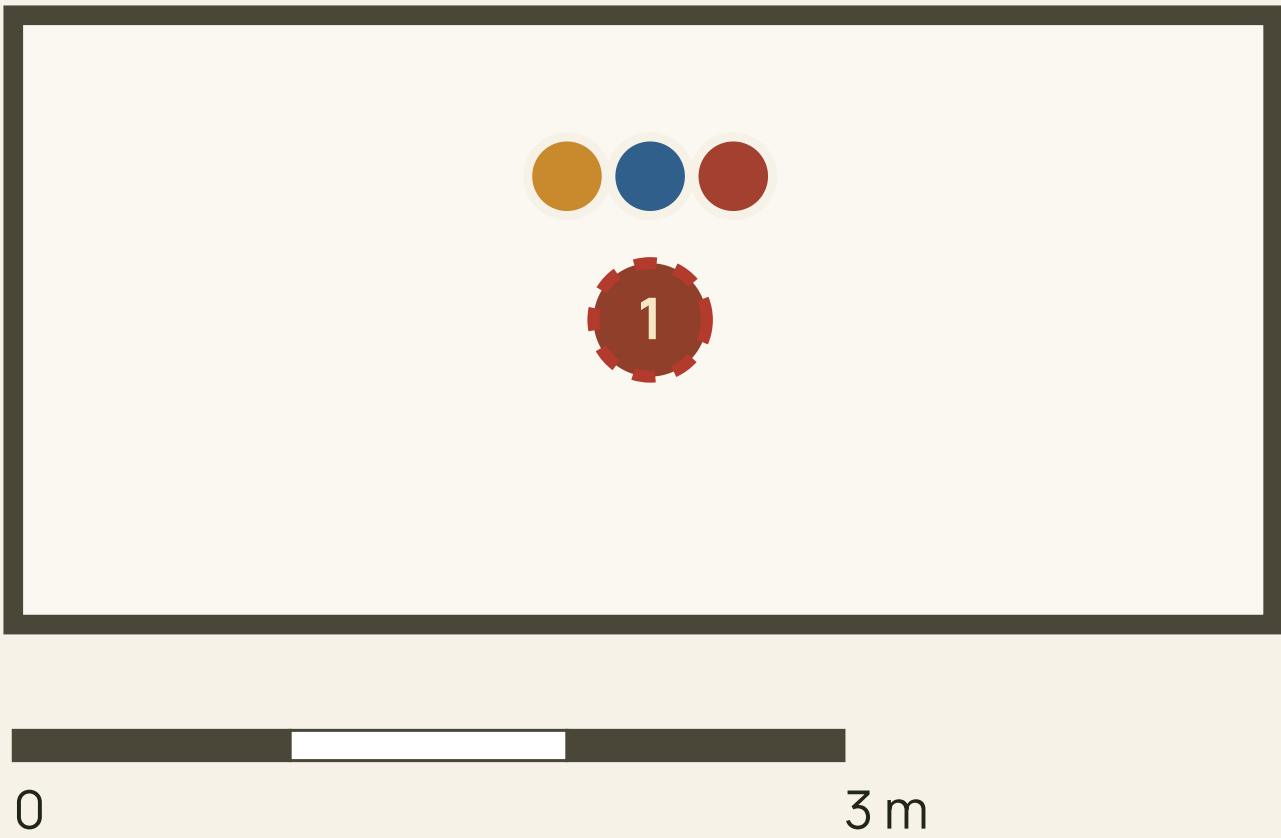

Quadro de pontos

1

Cuba · torneira de bancada

EIXO 2,80 da parede superior · 1,75 ate a parede inferior (fecha com a profundidade do ambiente) — afastamento da parede esquerda NAO COTADO: posicao horizontal aproximada, NAO cotar em obra sem confirmar

A.Q.

0,50 m

A.F.

0,50 m*

ESG

0,50 m*

mesma linha do A.Q. confirmado

saida de sifao sob a cuba, pratica usual

Legenda

- A.F.

Agua fria
- A.Q.

Agua quente
- ESG

Esgoto
- V.D.

Valvula de descarga
- R.G.

Registro geral
- 1

Selo numerado do ponto (remete ao quadro de pontos)
- 1

Selo tracejado: posição em planta NÃO COTADA no caderno original — esquemática, não cotar em obra

Confirmado · dado do caderno original, Revisão 02.
Proposta · valor usual de mercado adotado por nós (não consta no original) — marcado com asterisco (*) no quadro de pontos, a validar com o responsável hidrossanitário.
Pendente · posição de projeto sem informação suficiente para propor — aguarda definição.

Observações técnicas

- 1

Cliente confirmou (28/09/2026): este ambiente nao tera nenhum equipamento adicional de agua (sem geladeira/adega/maquina de gelo).
- 2

Falta o afastamento da parede esquerda da cuba/torneira de bancada — nao e uma altura de instalacao padronizavel, e uma posicao de projeto. Precisamos dessa medida (planta cotada complementar, SketchUp ou medicao em campo) antes de fixar o eixo definitivo.
- 3

Altura de A.F. e de E.S.G.: PROPOSTA nossa (mercado), a validar com o responsavel hidrossanitario.

DUAS

design & arq

02/08

REVISÃO R01

PROJETO
Residência IC · Detalhamento de pontos hidráulicos

CLIENTES
Ivan e Carol

ENDEREÇO
Nova Odessa, SP

TIPO DE PLANTA
Planta de eixos hidráulicos · Gourmet

RESPONSÁVEIS TÉCNICOS (projeto de interiores)
Arq. Lidiane Barbosa · CAU A290220-6
Arq. Isadora Ferrari · CAU A269382-8

DATA
28/09/2026

ESCALA
1/27 (esquemático, reduzido para A2)

ORIGEM
Caderno Detalhamento Residencia IC - Hidraulica Detalhe, Rev. 02, 24/09/2026 + PROJETO IVAN E ANA - R01.dwg


CONFERIR AS MEDIDAS SINALIZADAS COMO PROPOSTA/PENDÊNCIA ANTES DE EXECUTAR · VÁLIDO EM A2 A 100%

Lavanderia

Planta de eixos · pontos de água fria, água quente e esgoto

Parede esquerda, com cotas encadeadas (0,40 · 0,60 · 0,80 · 0,75).

PLANTA DE EIXOS HIDRÁULICOS · ESC 1/15

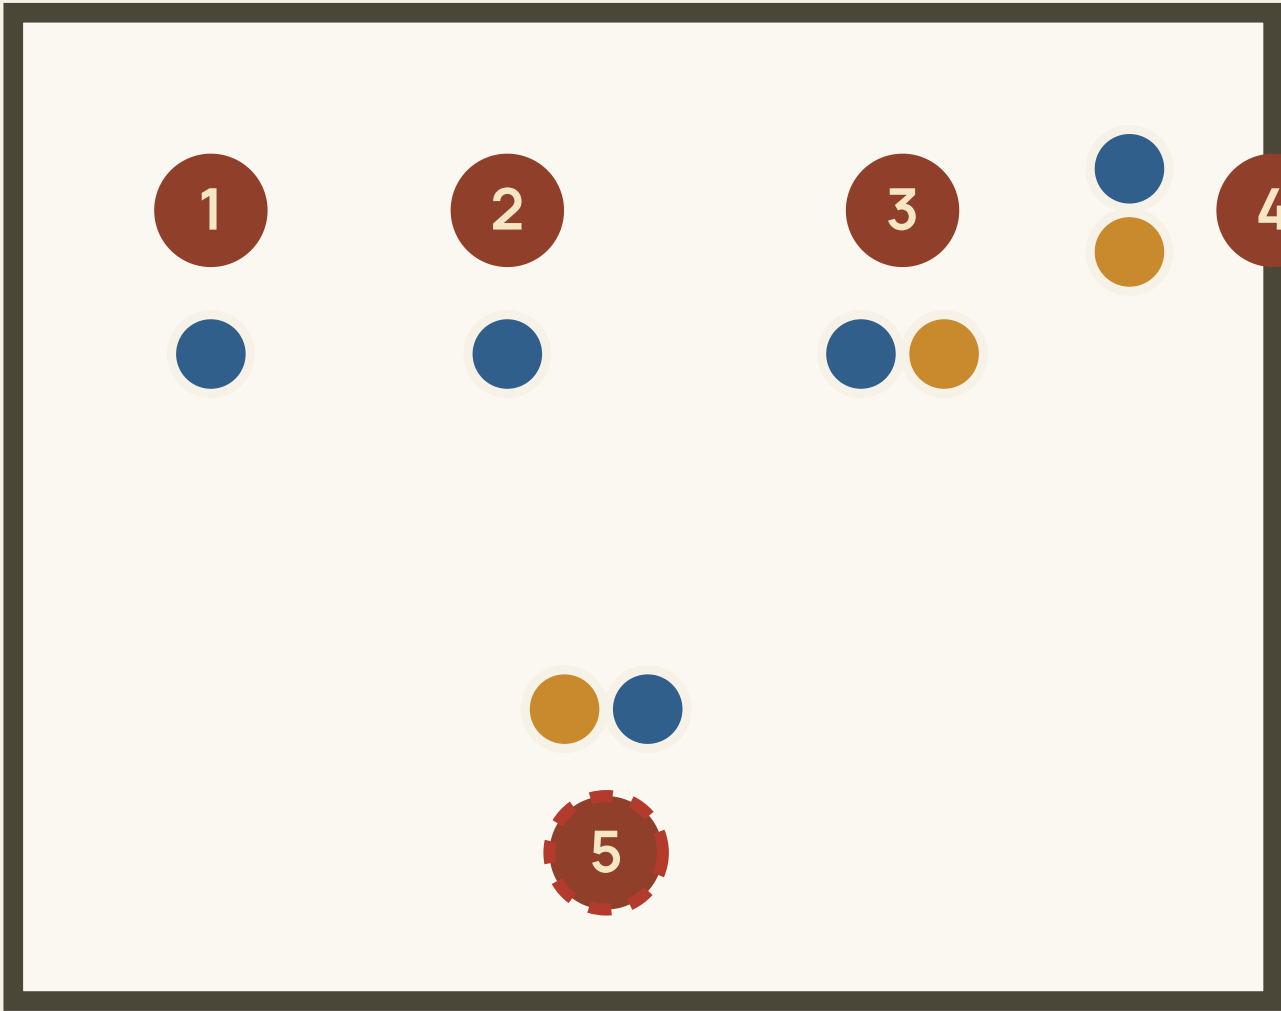

Quadro de pontos

1

Torneira de parede · tanque

EIXO 0,40 da parede esquerda

A.F.

1,00 m*

altura usual de torneira de parede alta para tanque

2

Torneira de parede · tanque

EIXO 0,60 a partir do eixo 1

A.F.

1,00 m*

altura usual de torneira de parede alta para tanque

3

Maquina de lavar roupas

EIXO 0,80 a partir do eixo 2

A.F.

0,70 m

altura usual de saída da maquina de lavar

ESG

0,60 m*

4

Tanquinho

EIXO 0,75 a partir do eixo 3

A.F.

0,70 m

saída de sifão do tanquinho, pratica usual

ESG

0,50 m*

5

A.F. + ESG da bancada do tanque

EIXO EIXO NAO COTADO no caderno original — posicao esquematica, NAO cotar em obra

A.F.

1,00 m

saída de sifão, pratica usual

ESG

0,50 m*

Legenda

- A.F.

Água fria
- A.Q.

Água quente
- ESG

Esgoto
- V.D.

Valvula de descarga
- R.G.

Registro geral
- 1

Selo numerado do ponto (remete ao quadro de pontos)
- 1

Selo tracejado: posição em planta NÃO COTADA no caderno original — esquemática, não cotar em obra

Confirmado - dado do caderno original, Revisão 02.
Proposta - valor usual de mercado adotado por nós (não consta no original) — marcado com asterisco (*) no quadro de pontos, a validar com o responsável hidrossanitário.
Pendente - posição de projeto sem informação suficiente para propor — aguarda definição.

Observações técnicas

- 1

PENDENCIA DE PROJETO (mantida por decisao do cliente, 28/09/2026) : sao DOIS eixos de torneira de parede independentes (pontos 1 e 2), reproduzindo o caderno original tal como esta. A vista do caderno original mostrava um unico ponto de A.F. entre as duas torneiras — nao reproduzimos essa vista; os dois eixos em planta valem como projetados.
- 2

Secadora: cliente confirmou (28/09/2026) que sera ELETTRICA — nao ha ponto de agua ou esgoto dedicado a ela nesta prancha.
- 3

Alturas de A.F. nas torneiras de parede e de E.S.G. na maquina de lavar e no tanquinho: PROPOSTA nossa (mercado), a validar com o responsavel hidrossanitario.
- 4

Eixo do ponto 5 nao consta no caderno original e nao e um dado padronizavel — posicao em planta pendente de definicao.

DUAS

design & arq

03/08

REVISÃO R01

PROJETO
Residência IC · Detalhamento de pontos hidráulicos

CLIENTES
Ivan e Carol

ENDEREÇO
Nova Odessa, SP

TIPO DE PLANTA
Planta de eixos hidráulicos · Lavanderia

RESPONSÁVEIS TÉCNICOS (projeto de interiores)
Arq. Lidiane Barbosa · CAU A290220-6
Arq. Isadora Ferrari · CAU A269382-8

DATA
28/09/2026

ESCALA
1/15 (esquemático, reduzido para A2)

ORIGEM
Caderno Detalhamento Residencia IC - Hidraulica Detalhe, Rev. 02, 24/09/2026 + PROJETO IVAN E ANA - R01.dwg


CONFERIR AS MEDIDAS SINALIZADAS COMO PROPOSTA/PENDÊNCIA ANTES DE EXECUTAR - VÁLIDO EM A2 A 100%

WC 01

Planta de eixos · pontos de água fria, água quente e esgoto

Parede de referencia, cotas encadeadas: 0,45 · 0,75 · 0,20 · 0,95 · 0,55 (chuveiro / ducha / bacia / cuba / parede direita).

PLANTA DE EIXOS HIDRÁULICOS · ESC 1/17

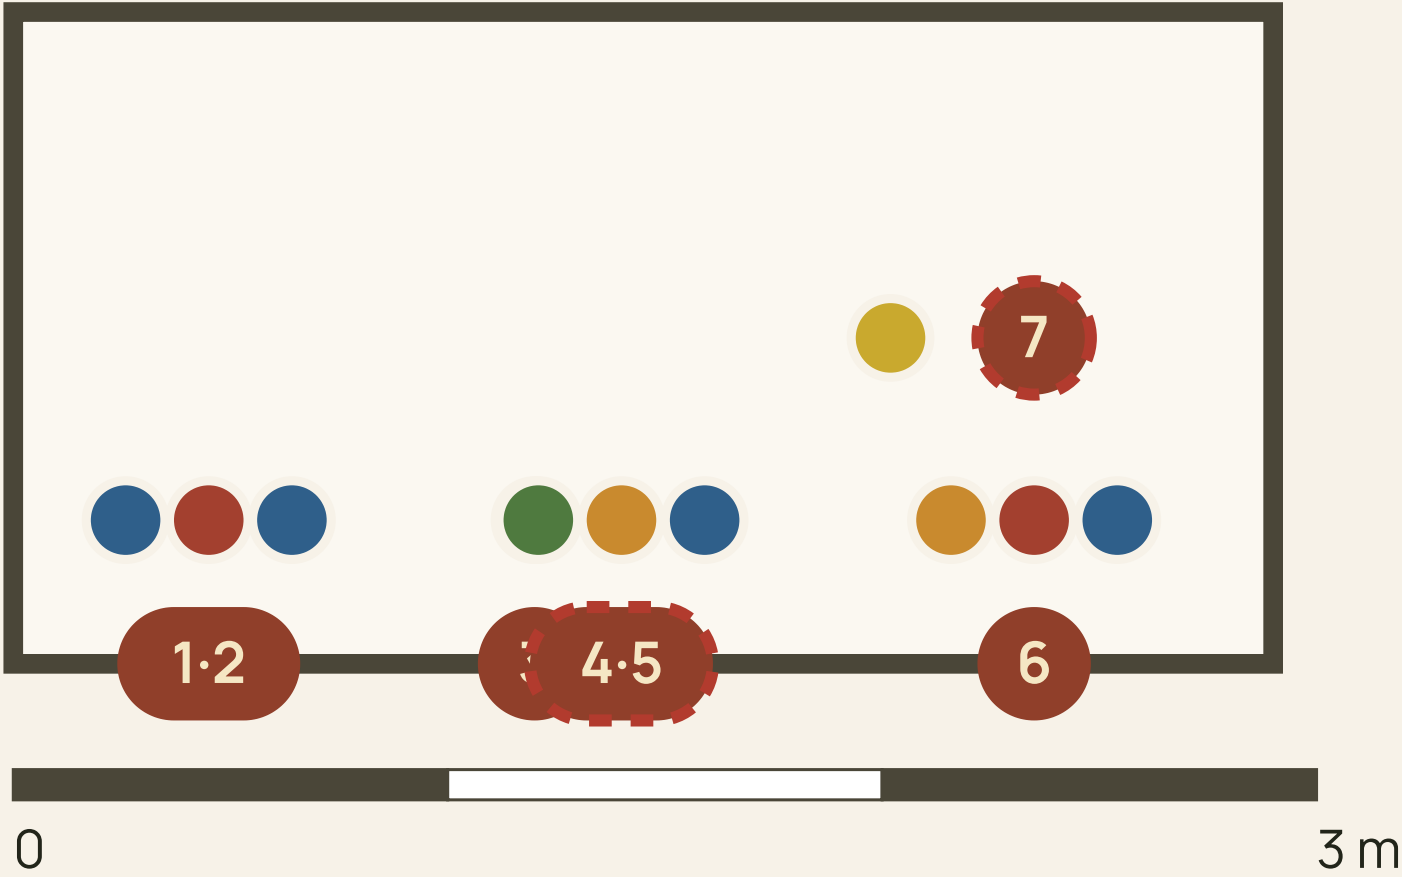

Legenda

- A.F. Água fria
- A.Q. Água quente
- ESG Esgoto
- V.D. Valvula de descarga
- R.G. Registro geral
- 1 Selo numerado do ponto (remete ao quadro de pontos)
- 1 Selo tracejado: posição em planta NÃO COTADA no caderno original — esquemática, não cotar em obra

Confirmado - dado do caderno original, Revisão 02.
Proposta - valor usual de mercado adotado por nós (não consta no original) — marcado com asterisco (*) no quadro de pontos, a validar com o responsável hidrossanitário.
Pendente - posição de projeto sem informação suficiente para propor — aguarda definição.

Observações técnicas

- Chuveiro mantido como tipo ducha (misturador), alimentado por agua quente de origem externa (nao eletrico) — decisao do cliente, 28/09/2026.
- Cotas de eixo em planta reproduzidas do caderno original (Revisao 02), 0,45 · 0,75 · 0,20 · 0,95 · 0,55 (chuveiro / ducha / bacia / cuba / parede direita).
- Alturas marcadas como PROPOSTA sao valores usuais de mercado (nao constam no caderno original) — decisao do cliente (28/09/2026): adotar e sinalizar, aguardando validacao do responsavel hidrossanitario antes da execucao.
- Eixo do registro geral nao consta no caderno original: e uma posicao de projeto (local dentro do armario), nao um dado padronizavel — mantido pendente.
- Normas de referencia: NBR 5626 (agua fria), NBR 7198 (agua quente) e NBR 8160 (esgoto sanitario).

Quadro de pontos

- 1 Chuveiro (tipo ducha)**
EIXO 0.45 da parede de referencia

 - A.F. 2,10 m
- 2 Registros do chuveiro**
EIXO mesmo eixo do chuveiro — afastamento lateral entre A.Q. e A.F. NAO COTADO no caderno original (PROPOSTA: 0.06 m, afastamento usual entre registros)

 - A.Q. 1,10 m
 - A.F. 1,10 m
- 3 Ducha higienica**
EIXO 1.20 da parede de referencia

 - A.F. 0,50 m* altura usual de ducha higienica

- 4 Bacia sanitaria**
EIXO 1.40 da parede de referencia

 - A.F. 0,30 m* altura usual de alimentacao de caixa acoplada
 - ESG 0,00 m ESG no piso, conforme caderno original
- 5 Valvula de descarga**
EIXO mesmo eixo da bacia sanitaria (posicao usual — valvula fica sobre a saida da bacia)

 - V.D. 1,10 m* altura usual de acionamento de valvula de descarga
- 6 Cuba pia · torneira de bancada**
EIXO 2.35 da parede de referencia

 - A.F. 0,60 m
 - A.Q. 0,60 m* mesma linha do A.F. confirmado
 - ESG 0,50 m* saida de sifao, pratica usual

DUAS
design & arq

04/08
REVISÃO R01

PROJETO
Residência IC · Detalhamento de pontos hidráulicos

CLIENTES
Ivan e Carol

ENDEREÇO
Nova Odessa, SP

TIPO DE PLANTA
Planta de eixos hidráulicos · WC 01

RESPONSÁVEIS TÉCNICOS (projeto de interiores)
Arq. Lidiane Barbosa · CAU A290220-6
Arq. Isadora Ferrari · CAU A269382-8

DATA
28/09/2026

ESCALA
1/17 (esquemático, reduzido para A2)

ORIGEM
Caderno Detalhamento Residencia IC - Hidraulica Detalhe, Rev. 02, 24/09/2026 + PROJETO IVAN E ANA - R01.dwg


CONFERIR AS MEDIDAS SINALIZADAS COMO PROPOSTA/PENDÊNCIA ANTES DE EXECUTAR - VÁLIDO EM A2 A 100%

WC 02

Planta de eixos · pontos de água fria, água quente e esgoto

Parede de referencia, cotas encadeadas: 0,45 · 0,75 · 0,20 · 0,95 · 0,55 (chuveiro / ducha / bacia / cuba / parede direita) — disposicao espelhada em relacao ao WC 01.

PLANTA DE EIXOS HIDRÁULICOS · ESC 1/17

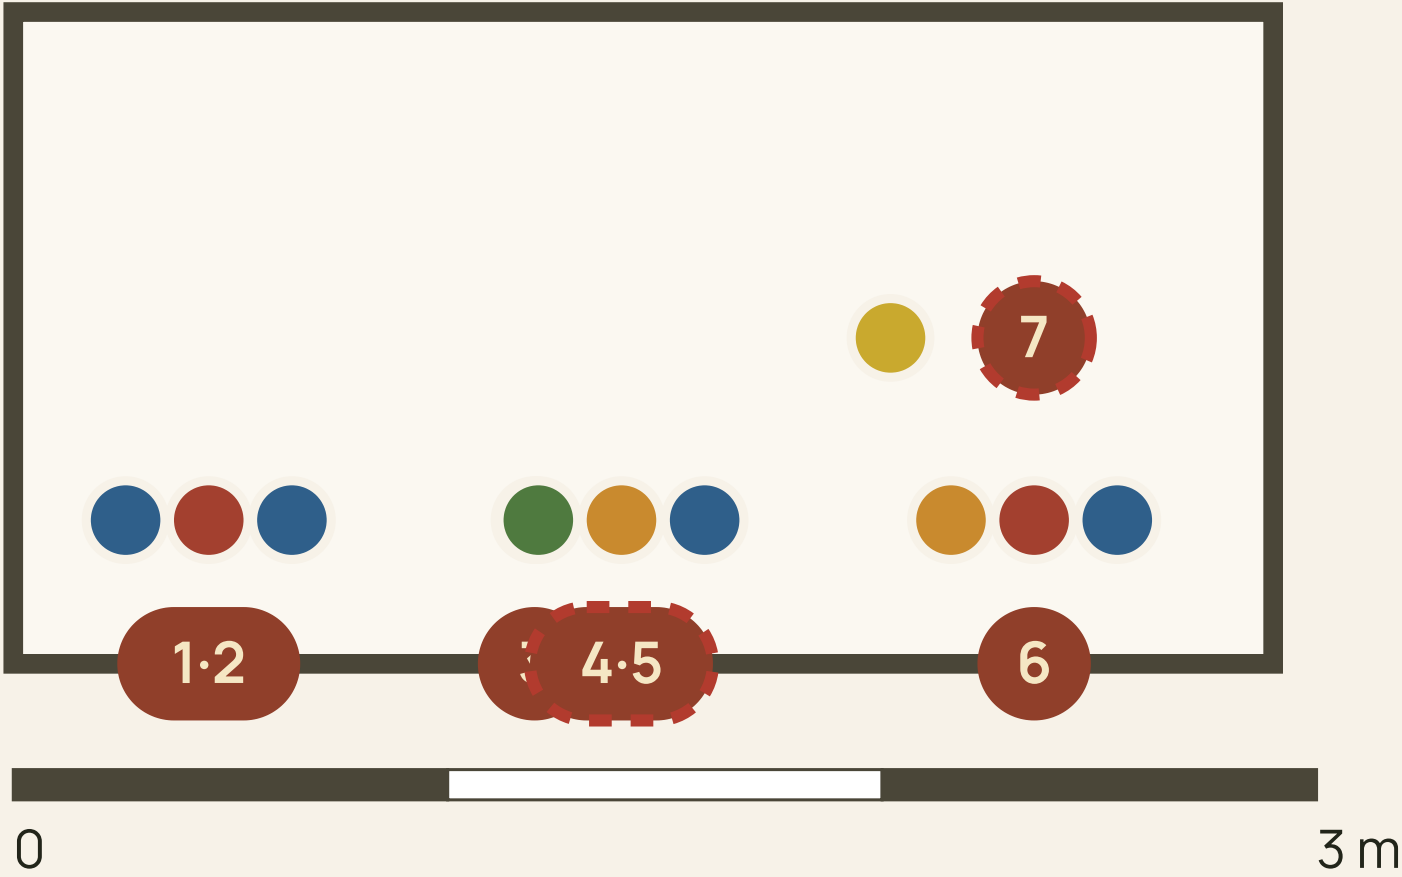

Legenda

- **A.F.** Água fria
- **A.Q.** Água quente
- **ESG** Esgoto
- **V.D.** Valvula de descarga
- **R.G.** Registro geral
- 1 Selo numerado do ponto (remete ao quadro de pontos)
- 1 Selo tracejado: posição em planta NÃO COTADA no caderno original — esquemática, não cotar em obra

Confirmado - dado do caderno original, Revisão 02.
Proposta - valor usual de mercado adotado por nós (não consta no original) — marcado com asterisco (*) no quadro de pontos, a validar com o responsável hidrossanitário.
Pendente - posição de projeto sem informação suficiente para propor — aguarda definição.

Observações técnicas

- Chuveiro mantido como tipo ducha (misturador), alimentado por agua quente de origem externa (nao eletrico) — decisao do cliente, 28/09/2026.
- Cotas de eixo em planta reproduzidas do caderno original (Revisao 02), 0,45 · 0,75 · 0,20 · 0,95 · 0,55 (chuveiro / ducha / bacia / cuba / parede direita) — disposicao espelhada em relacao ao WC 01.
- Alturas marcadas como PROPOSTA sao valores usuais de mercado (nao constam no caderno original) — decisao do cliente (28/09/2026): adotar e sinalizar, aguardando validacao do responsavel hidrossanitario antes da execucao.
- Eixo do registro geral nao consta no caderno original: e uma posicao de projeto (local dentro do armario), nao um dado padronizavel — mantido pendente.
- Normas de referencia: NBR 5626 (agua fria), NBR 7198 (agua quente) e NBR 8160 (esgoto sanitario).

Quadro de pontos

1 Chuveiro (tipo ducha) EIXO 0,45 da parede de referencia A.F. 2,10 m	4 Bacia sanitaria EIXO 1,40 da parede de referencia A.F. 0,30 m* <i>altura usual de alimentacao de caixa acoplada</i> ESG 0,00 m <i>ESG no piso, conforme caderno original</i>
2 Registros do chuveiro EIXO mesmo eixo do chuveiro — afastamento lateral entre A.Q. e A.F. NAO COTADO no caderno original (PROPOSTA: 0,06 m, afastamento usual entre registros) A.Q. 1,10 m A.F. 1,10 m	5 Valvula de descarga EIXO mesmo eixo da bacia sanitaria (posicao usual — valvula fica sobre a saida da bacia) V.D. 1,10 m* <i>altura usual de acionamento de valvula de descarga</i>
3 Ducha higienica EIXO 1,20 da parede de referencia A.F. 0,50 m* <i>altura usual de ducha higienica</i>	6 Cuba pia · torneira de bancada EIXO 2,35 da parede de referencia A.F. 0,60 m A.Q. 0,60 m* <i>mesma linha do A.F. confirmado</i> ESG 0,50 m* <i>saida de sifao, pratica usual</i>

DUAS

design & arq

05/08

REVISÃO R01

PROJETO
Residência IC · Detalhamento de pontos hidráulicos

CLIENTES
Ivan e Carol

ENDEREÇO
Nova Odessa, SP

TIPO DE PLANTA
Planta de eixos hidráulicos · WC 02

RESPONSÁVEIS TÉCNICOS (projeto de interiores)
Arq. Lidiane Barbosa · CAU A290220-6
Arq. Isadora Ferrari · CAU A269382-8

DATA
28/09/2026

ESCALA
1/17 (esquemático, reduzido para A2)

ORIGEM
Caderno Detalhamento Residencia IC - Hidraulica Detalhe, Rev. 02, 24/09/2026 + PROJETO IVAN E ANA - R01.dwg


CONFERIR AS MEDIDAS SINALIZADAS COMO PROPOSTA/PENDÊNCIA ANTES DE EXECUTAR - VÁLIDO EM A2 A 100%

WC Suíte Master

Planta de eixos · pontos de água fria, água quente e esgoto

Parede superior, cotas encadeadas: 0,25 (ducha) · 0,20 (bacia) · 1,15 (cuba). Chuveiro em parede propria: 1,25 a partir do eixo da cuba · 0,55 ate a parede inferior (fecha com tolerancia de 0,10 m em relacao a cadeia acumulada).

PLANTA DE EIXOS HIDRÁULICOS · ESC 1/21

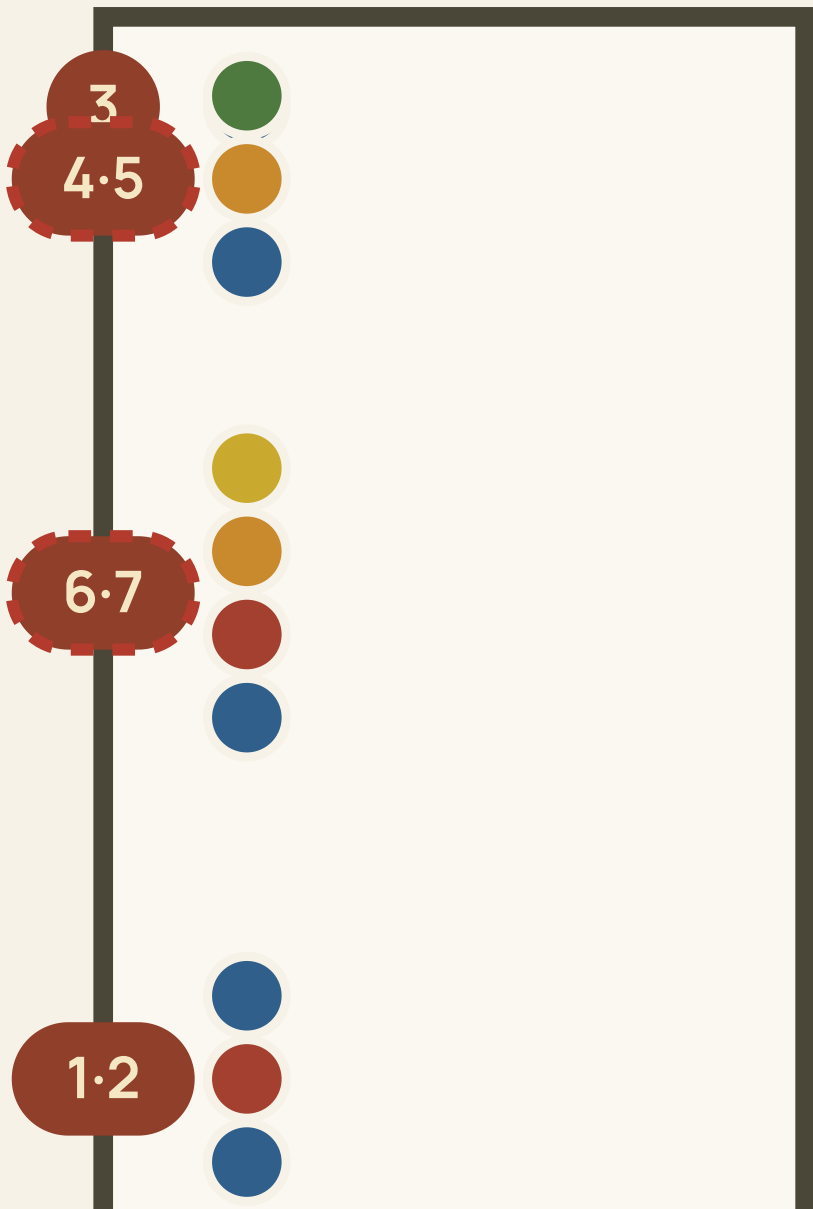

Legenda

- A.F.** Água fria
- A.Q.** Água quente
- ESG** Esgoto
- V.D.** Valvula de descarga
- R.G.** Registro geral
- 1** Selo numerado do ponto (remete ao quadro de pontos)
- 5** Selo tracejado: posição em planta NÃO COTADA no caderno original — esquemática, não cotar em obra

Confirmado - dado do caderno original, Revisão 02.
Proposta - valor usual de mercado adotado por nós (não consta no original) — marcado com asterisco (*) no quadro de pontos, a validar com o responsável hidrossanitário.
Pendente - posição de projeto sem informação suficiente para propor — aguarda definição.

Observações técnicas

- Nome do ambiente mantido como 'WC Suite Master' (decisao do cliente, 28/09/2026) — no caderno original ele aparece como 'WC Casal' e no DWG de referencia como 'Banheiro Casal'.
- Chuveiro mantido como tipo ducha (misturador), alimentado por agua quente de origem externa (nao eletrico) — decisao do cliente, 28/09/2026.
- O chuveiro fica em parede propria, distinta da parede onde estao ducha/bacia/cuba — a cadeia de cotas do caderno original fecha com 0,10 m de tolerancia; nao e uma cota exata, e sim a soma dos trechos publicados.
- Falta a cota que fecha a cuba/torneira de bancada contra a parede lateral oposta — nao e uma altura padronizavel, precisamos dessa medida.
- Alturas marcadas como PROPOSTA sao valores usuais de mercado (nao constam no caderno original) — decisao do cliente (28/09/2026): adotar e sinalizar, aguardando validacao do responsavel hidrossanitario.
- Normas de referencia: NBR 5626 (agua fria), NBR 7198 (agua quente) e NBR 8160 (esgoto sanitario).

Quadro de pontos

3 Ducha higienica EIXO 0,25 da parede superior A.F. 0,50 m* altura usual de ducha higienica	6 Cuba pia · torneira de bancada EIXO 1,15 a partir do eixo da bacia — falta a cota de fechamento ate a parede lateral oposta A.F. 0,60 m A.Q. 0,60 m* mesma linha do A.F. confirmado ESG 0,50 m* saida de sifao, pratica usual
4 Bacia sanitaria EIXO 0,20 a partir do eixo da ducha A.F. 0,30 m* altura usual de alimentacao de caixa acoplada ESG 0,00 m ESG no piso, conforme caderno original	1 Chuveiro (tipo ducha) EIXO 1,25 a partir do eixo da cuba · 0,55 ate a parede inferior A.F. 2,10 m
5 Valvula de descarga EIXO mesmo eixo da bacia sanitaria (posicao usual) V.D. 1,10 m* altura usual de acionamento de valvula de descarga	2 Registros do chuveiro EIXO mesmo eixo do chuveiro — afastamento lateral entre A.Q. e A.F. NAO COTADO (PROPOSTA: 0,06 m) A.Q. 1,10 m A.F. 1,10 m

DUAS
design & arq

06/08
REVISÃO R01

PROJETO
Residência IC · Detalhamento de pontos hidráulicos

CLIENTES
Ivan e Carol
ENDEREÇO
Nova Odessa, SP

TIPO DE PLANTA
Planta de eixos hidráulicos · WC Suite Master

RESPONSÁVEIS TÉCNICOS (projeto de interiores)
Arq. Lidiane Barbosa · CAU A290220-6
Arq. Isadora Ferrari · CAU A269382-8

DATA
28/09/2026
ESCALA
1/21 (esquemático, reduzido para A2)

ORIGEM
Caderno Detalhamento Residencia IC - Hidraulica Detalhe, Rev. 02, 24/09/2026 + PROJETO IVAN E ANA - R01.dwg


CONFERIR AS MEDIDAS SINALIZADAS COMO PROPOSTA/PENDÊNCIA ANTES DE EXECUTAR - VÁLIDO EM A2 A 100%

WC Externo

Planta de eixos · pontos de água fria, água quente e esgoto

Parede de referencia, cotas encadeadas: 0,55 · 0,60 · 0,20 · 0,60 · 1,15 (chuveiro / ducha / bacia / cuba / parede direita).

PLANTA DE EIXOS HIDRÁULICOS · ESC 1/19

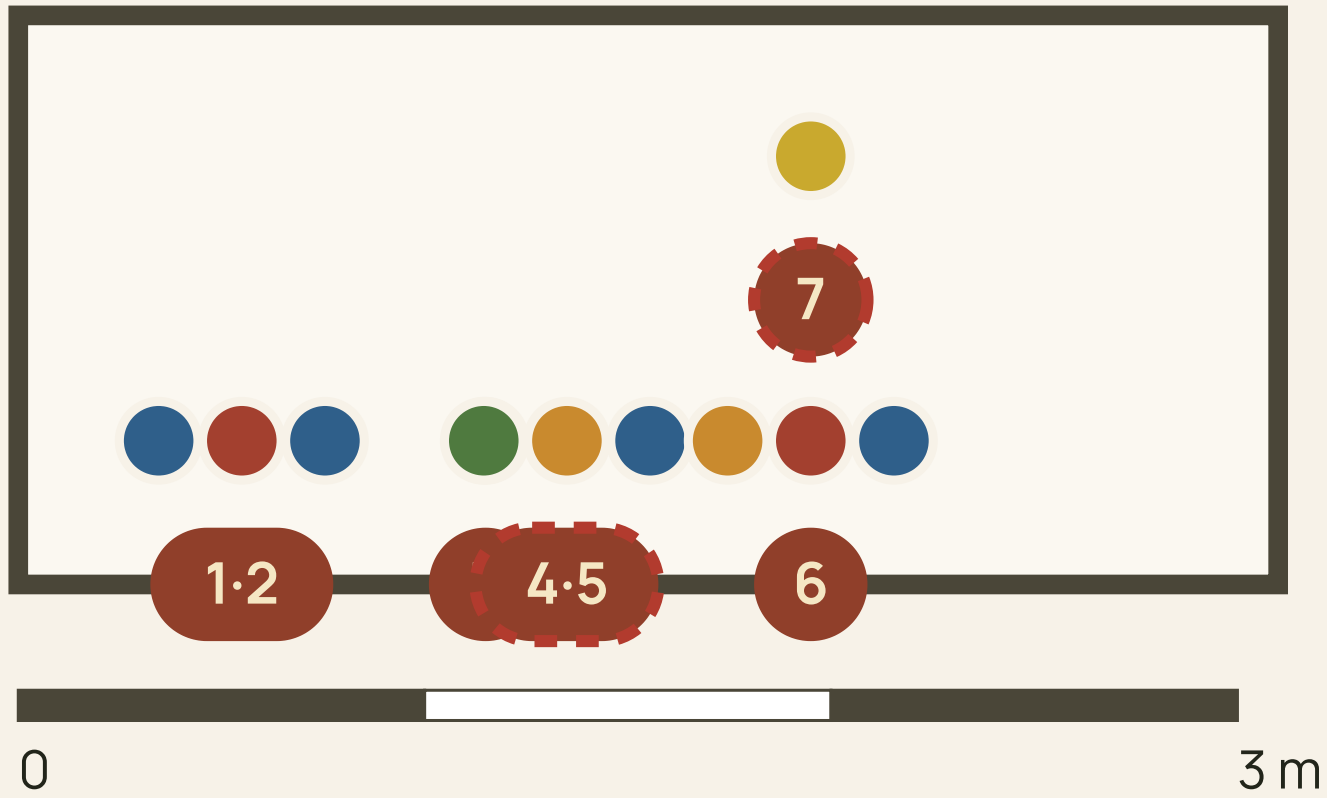

Legenda

- A.F. Água fria
- A.Q. Água quente
- ESG Esgoto
- V.D. Valvula de descarga
- R.G. Registro geral
- 1 Selo numerado do ponto (remete ao quadro de pontos)
- 1 Selo tracejado: posição em planta NÃO COTADA no caderno original — esquemática, não cotar em obra

Confirmado - dado do caderno original, Revisão 02.
Proposta - valor usual de mercado adotado por nós (não consta no original) — marcado com asterisco (*) no quadro de pontos, a validar com o responsável hidrossanitário.
Pendente - posição de projeto sem informação suficiente para propor — aguarda definição.

Observações técnicas

- Divergencia resolvida (decisao do cliente, 28/09/2026): a altura do A.F. da cuba/torneira de bancada passa a ser 0,60 m, igual aos demais WCs — no caderno original ela aparecia na vista sobreposta a linha do registro geral (0,55 m), sem cota propria. O registro geral deste ambiente mantem seus 0,55 m, que sao o UNICO valor de R.G. confirmado em todo o caderno original — por isso foi adotado por analogia nos demais banheiros.
- Chuveiro mantido como tipo ducha (misturador), alimentado por agua quente de origem externa (nao eletrico) — decisao do cliente, 28/09/2026.
- Cotas de eixo em planta reproduzidas do caderno original (Revisao 02), 0,55 · 0,60 · 0,20 · 0,60 · 1,15 (chuveiro / ducha / bacia / cuba / parede direita).
- Alturas marcadas como PROPOSTA sao valores usuais de mercado (nao constam no caderno original) — decisao do cliente (28/09/2026): adotar e sinalizar, aguardando validacao do responsavel hidrossanitario antes da execucao.
- Eixo do registro geral nao consta no caderno original: e uma posicao de projeto (local dentro do armario), nao um dado padronizavel — mantido pendente.
- Normas de referencia: NBR 5626 (agua fria), NBR 7198 (agua quente) e NBR 8160 (esgoto sanitario).

Quadro de pontos

1 Chuveiro (tipo ducha) EIXO 0.55 da parede de referencia A.F. 2,10 m	4 Bacia sanitaria EIXO 1.35 da parede de referencia A.F. 0,30 m* altura usual de alimentacao de caixa acoplada ESG 0,00 m ESG no piso, conforme caderno original
2 Registros do chuveiro EIXO mesmo eixo do chuveiro — afastamento lateral entre A.Q. e A.F. NAO COTADO no caderno original (PROPOSTA: 0,06 m, afastamento usual entre registros) A.Q. 1,10 m A.F. 1,10 m	5 Valvula de descarga EIXO mesmo eixo da bacia sanitaria (posicao usual — valvula fica sobre a saida da bacia) V.D. 1,10 m* altura usual de acionamento de valvula de descarga
3 Ducha higienica EIXO 1.15 da parede de referencia A.F. 0,50 m* altura usual de ducha higienica	6 Cuba pia · torneira de bancada EIXO 1.95 da parede de referencia A.F. 0,60 m decisao do cliente 28/09/2026: usar 0,60 m, mesma referencia dos demais WCs, em vez do valor de 0,55 m que no caderno original estava sobreposto ao do registro geral A.Q. 0,60 m* mesma linha do A.F. ESG 0,50 m* saida de sifao, pratica usual

DUAS
design & arq

07/08
REVISÃO R01

PROJETO
Residência IC · Detalhamento de pontos hidráulicos

CLIENTES
Ivan e Carol

ENDEREÇO
Nova Odessa, SP

TIPO DE PLANTA
Planta de eixos hidráulicos · WC Externo

RESPONSÁVEIS TÉCNICOS (projeto de interiores)
Arq. Lidiane Barbosa · CAU A290220-6
Arq. Isadora Ferrari · CAU A269382-8

DATA
28/09/2026

ESCALA
1/19 (esquemático, reduzido para A2)

ORIGEM
Caderno Detalhamento Residencia IC - Hidraulica Detalhe, Rev. 02, 24/09/2026 + PROJETO IVAN E ANA - R01.dwg

CONFERIR AS MEDIDAS SINALIZADAS COMO PROPOSTA/PENDÊNCIA ANTES DE EXECUTAR - VÁLIDO EM A2 A 100%

Quadro consolidado e pendências

Pr.	Ambiente	Pt.	Peça	Tipo	Altura	Status altura	Status eixo
01	Cozinha	1	Filtro	A.F.	1,00 m	Confirmado	Confirmado
01	Cozinha	2	Cuba pia - torneira de bancada	A.Q.	0,50 m	Confirmado	Confirmado
01	Cozinha	2	Cuba pia - torneira de bancada	A.F.	0,50 m	Proposta	Confirmado
01	Cozinha	2	Cuba pia - torneira de bancada	ESG	0,35 m	Confirmado	Confirmado
01	Cozinha	3	Geladeira	A.F.	1,25 m	Confirmado	Confirmado
01	Cozinha	4	Lava-louças (ilha)	A.F.	0,60 m	Confirmado	Pendente
01	Cozinha	4	Lava-louças (ilha)	ESG	0,50 m	Proposta	Pendente
02	Gourmet	1	Cuba - torneira de bancada	A.Q.	0,50 m	Confirmado	Pendente
02	Gourmet	1	Cuba - torneira de bancada	A.F.	0,50 m	Proposta	Pendente
02	Gourmet	1	Cuba - torneira de bancada	ESG	0,50 m	Proposta	Pendente
03	Lavanderia	1	Torneira de parede - tanque	A.F.	1,00 m	Proposta	Confirmado
03	Lavanderia	2	Torneira de parede - tanque	A.F.	1,00 m	Proposta	Confirmado
03	Lavanderia	3	Maquina de lavar roupas	A.F.	0,70 m	Confirmado	Confirmado
03	Lavanderia	3	Maquina de lavar roupas	ESG	0,60 m	Proposta	Confirmado
03	Lavanderia	4	Tanquinho	A.F.	0,70 m	Confirmado	Confirmado
03	Lavanderia	4	Tanquinho	ESG	0,50 m	Proposta	Confirmado
03	Lavanderia	5	A.F. + ESG da bancada do tanque	A.F.	1,00 m	Confirmado	Pendente
03	Lavanderia	5	A.F. + ESG da bancada do tanque	ESG	0,50 m	Proposta	Pendente
04	WC 01	1	Chuveiro (tipo ducha)	A.F.	2,10 m	Confirmado	Confirmado
04	WC 01	2	Registros do chuveiro	A.Q.	1,10 m	Confirmado	Confirmado
04	WC 01	2	Registros do chuveiro	A.F.	1,10 m	Confirmado	Confirmado
04	WC 01	3	Ducha higienica	A.F.	0,50 m	Proposta	Confirmado
04	WC 01	4	Bacia sanitaria	A.F.	0,30 m	Proposta	Confirmado
04	WC 01	4	Bacia sanitaria	ESG	0,00 m	Confirmado	Confirmado
04	WC 01	5	Valvula de descarga	V.D.	1,10 m	Proposta	Pendente
04	WC 01	6	Cuba pia - torneira de bancada	A.F.	0,60 m	Confirmado	Confirmado
04	WC 01	6	Cuba pia - torneira de bancada	A.Q.	0,60 m	Proposta	Confirmado
04	WC 01	6	Cuba pia - torneira de bancada	ESG	0,50 m	Proposta	Confirmado
04	WC 01	7	Registro geral (dentro do armario)	R.G.	0,55 m	Proposta	Pendente
05	WC 02	1	Chuveiro (tipo ducha)	A.F.	2,10 m	Confirmado	Confirmado
05	WC 02	2	Registros do chuveiro	A.Q.	1,10 m	Confirmado	Confirmado
05	WC 02	2	Registros do chuveiro	A.F.	1,10 m	Confirmado	Confirmado
05	WC 02	3	Ducha higienica	A.F.	0,50 m	Proposta	Confirmado
05	WC 02	4	Bacia sanitaria	A.F.	0,30 m	Proposta	Confirmado
05	WC 02	4	Bacia sanitaria	ESG	0,00 m	Confirmado	Confirmado
05	WC 02	5	Valvula de descarga	V.D.	1,10 m	Proposta	Pendente
05	WC 02	6	Cuba pia - torneira de bancada	A.F.	0,60 m	Confirmado	Confirmado
05	WC 02	6	Cuba pia - torneira de bancada	A.Q.	0,60 m	Proposta	Confirmado
05	WC 02	6	Cuba pia - torneira de bancada	ESG	0,50 m	Proposta	Confirmado
05	WC 02	7	Registro geral (dentro do armario)	R.G.	0,55 m	Proposta	Pendente
06	WC Suite Master	3	Ducha higienica	A.F.	0,50 m	Proposta	Confirmado
06	WC Suite Master	4	Bacia sanitaria	A.F.	0,30 m	Proposta	Confirmado
06	WC Suite Master	4	Bacia sanitaria	ESG	0,00 m	Confirmado	Confirmado
06	WC Suite Master	5	Valvula de descarga	V.D.	1,10 m	Proposta	Pendente
06	WC Suite Master	6	Cuba pia - torneira de bancada	A.F.	0,60 m	Confirmado	Confirmado
06	WC Suite Master	6	Cuba pia - torneira de bancada	A.Q.	0,60 m	Proposta	Confirmado
06	WC Suite Master	6	Cuba pia - torneira de bancada	ESG	0,50 m	Proposta	Confirmado
06	WC Suite Master	1	Chuveiro (tipo ducha)	A.F.	2,10 m	Confirmado	Confirmado
06	WC Suite Master	2	Registros do chuveiro	A.Q.	1,10 m	Confirmado	Confirmado
06	WC Suite Master	2	Registros do chuveiro	A.F.	1,10 m	Confirmado	Confirmado
06	WC Suite Master	7	Registro geral (dentro do armario)	R.G.	0,55 m	Proposta	Pendente
07	WC Externo	1	Chuveiro (tipo ducha)	A.F.	2,10 m	Confirmado	Confirmado
07	WC Externo	2	Registros do chuveiro	A.Q.	1,10 m	Confirmado	Confirmado
07	WC Externo	2	Registros do chuveiro	A.F.	1,10 m	Confirmado	Confirmado
07	WC Externo	3	Ducha higienica	A.F.	0,50 m	Proposta	Confirmado
07	WC Externo	4	Bacia sanitaria	A.F.	0,30 m	Proposta	Confirmado
07	WC Externo	4	Bacia sanitaria	ESG	0,00 m	Confirmado	Confirmado
07	WC Externo	5	Valvula de descarga	V.D.	1,10 m	Proposta	Pendente
07	WC Externo	6	Cuba pia - torneira de bancada	A.F.	0,60 m	Confirmado	Confirmado
07	WC Externo	6	Cuba pia - torneira de bancada	A.Q.	0,60 m	Proposta	Confirmado
07	WC Externo	6	Cuba pia - torneira de bancada	ESG	0,50 m	Proposta	Confirmado
07	WC Externo	7	Registro geral (dentro do armario)	R.G.	0,55 m	Confirmado	Pendente

Como usar este quadro

- 1

Confirmado : dado do caderno hidráulico original (Revisão 02) ou decisão explícita do cliente em 28/09/2026. Pode ser executado.
- 2

Proposta : valor usual de mercado, adotado por nós na ausência de cota no caderno original, sinalizado a pedido do cliente. Precisa de validação do responsável pelo projeto hidrossanitário antes da execução.
- 3

Pendente : posição em planta sem cota no caderno original e sem base segura para propor (afeta o eixo/posição do ponto, não apenas a altura) – ver observações da prancha do ambiente.
- 4

Pendências em aberto que dependem de arquivo ainda não recebido: modelo SketchUp (posição da ilha da cozinha); prancha 01/02 do caderno de ar condicionado (possível interferência de dreno de condensado); afastamento da parede esquerda da bancada do Gourmet.

DUAS

design & arq

08/08

REVISÃO R01

PROJETO

Residência IC - Detalhamento de pontos hidráulicos

CLIENTES

Ivan e Carol

ENDEREÇO

Nova Odessa, SP

TIPO DE PLANTA

Quadro consolidado de pontos hidráulicos

RESPONSÁVEIS TÉCNICOS (projeto de interiores)

Arq. Lidiane Barbosa - CAU A290220-6

Arq. Isadora Ferrari - CAU A269382-8

DATA

28/09/2026

ESCALA

sem escala (tabela)

ORIGEM

Caderno Detalhamento Residencia IC - Hidraulica Detalhe, Rev. 02, 24/09/2026 + PROJETO IVAN E ANA - R01.dwg

CONFERIR AS MEDIDAS SINALIZADAS COMO PROPOSTA/PENDÊNCIA ANTES DE EXECUTAR - VÁLIDO EM A2 A 100%