


Cozinha

Planta de eixos + Vistas A, B e C

Planta de eixos hidráulicos

ESC 1/40

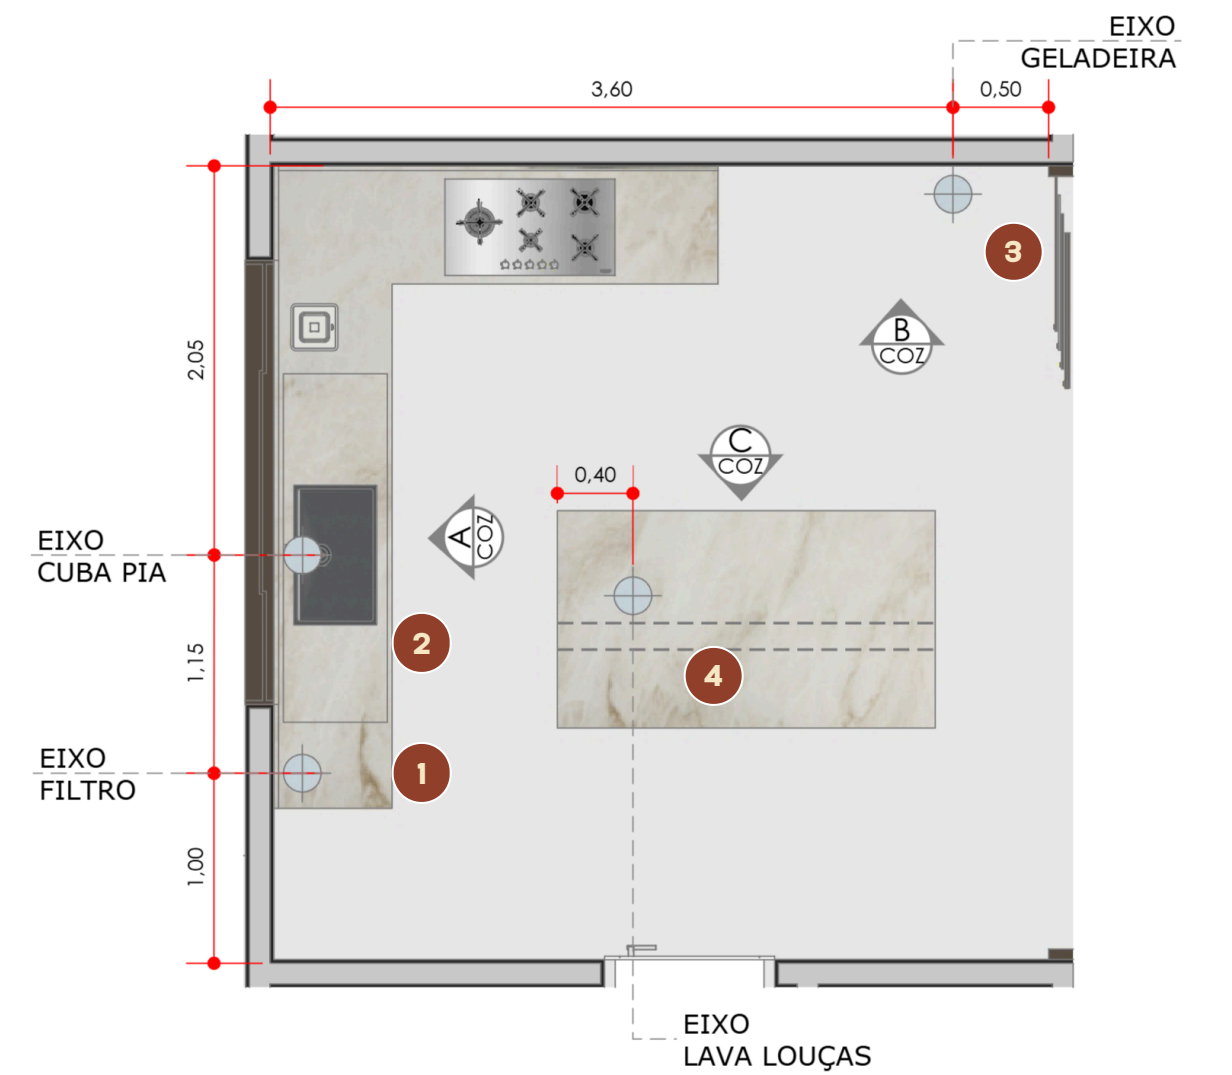


PAREDE DE REFERÊNCIA: eixos verticais a partir da parede inferior (filtro); geladeira a partir das paredes esquerda e direita; lava-louças a partir da borda da ilha.

Quadro de pontos

- Filtro**
EIXO 1,00 da parede inferior
A.F. 1,00
- Cuba pia · torneira de bancada**
EIXO 1,15 a partir do eixo do filtro; 2,05 até a parede superior
A.Q. 0,50
A.F. NÃO COTADO NA PRANCHA ORIGINAL / A CONFIRMAR
ESG 0,35
- Geladeira**
EIXO 3,60 da parede esquerda; 0,50 até a parede direita
A.F. 1,25
- Lava-louças (ilha)**
EIXO 0,40 da borda esquerda da ilha
A.F. 0,60
ESG NÃO COTADO NA PRANCHA ORIGINAL / A CONFIRMAR

Vista A · Cozinha

ESC 1/20

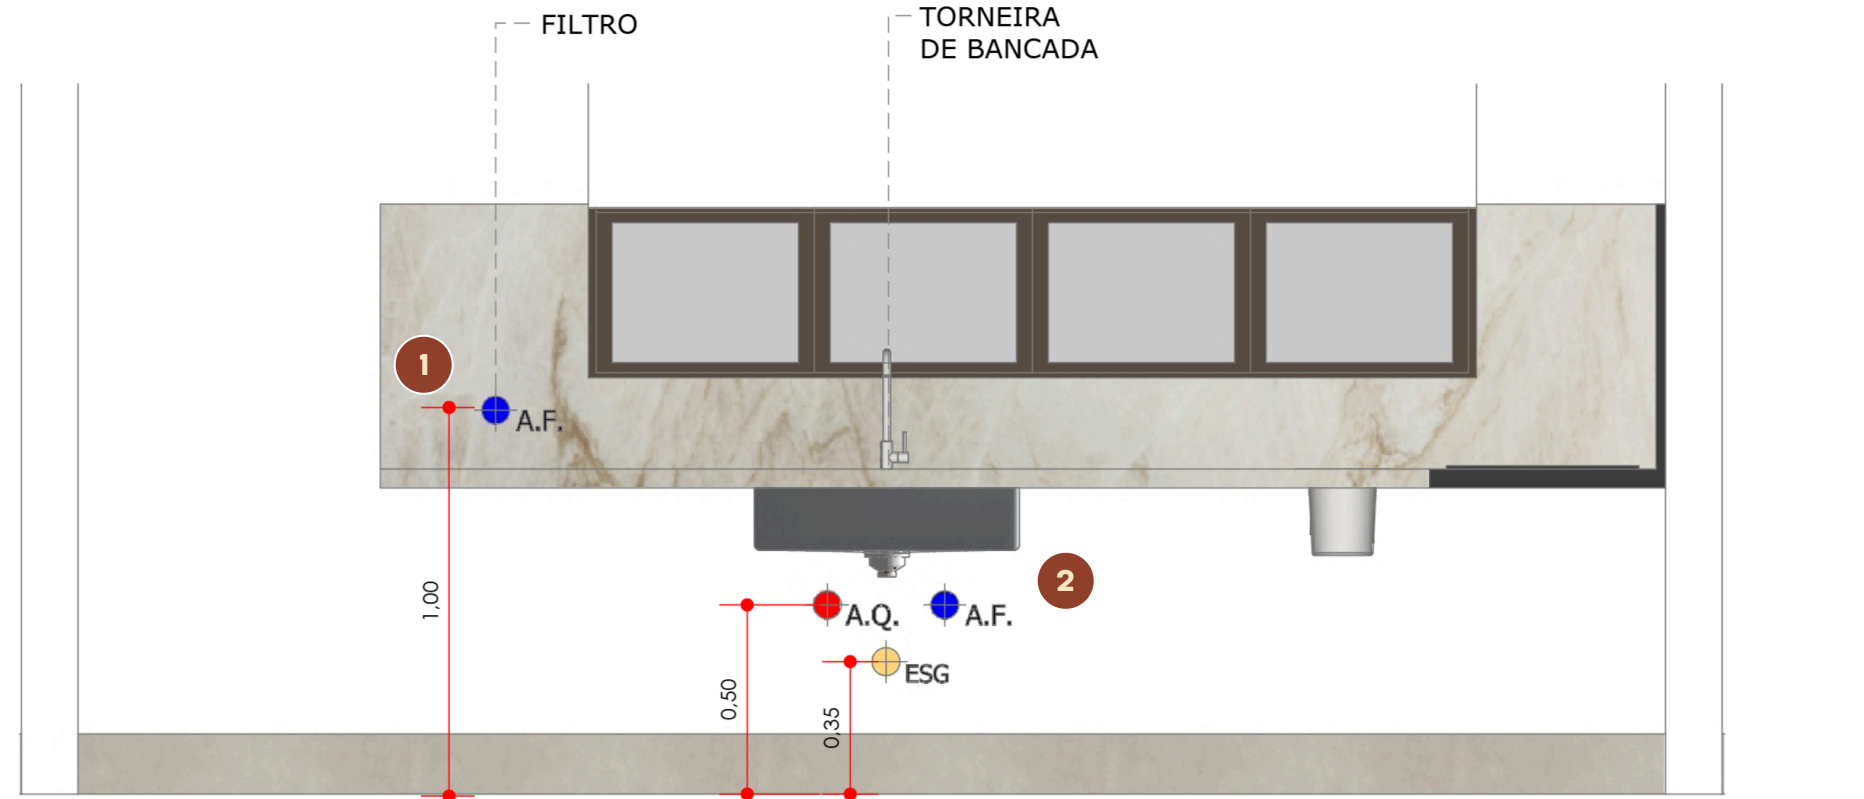


Vista B · Cozinha

ESC 1/20



Vista C · Cozinha

ESC 1/20

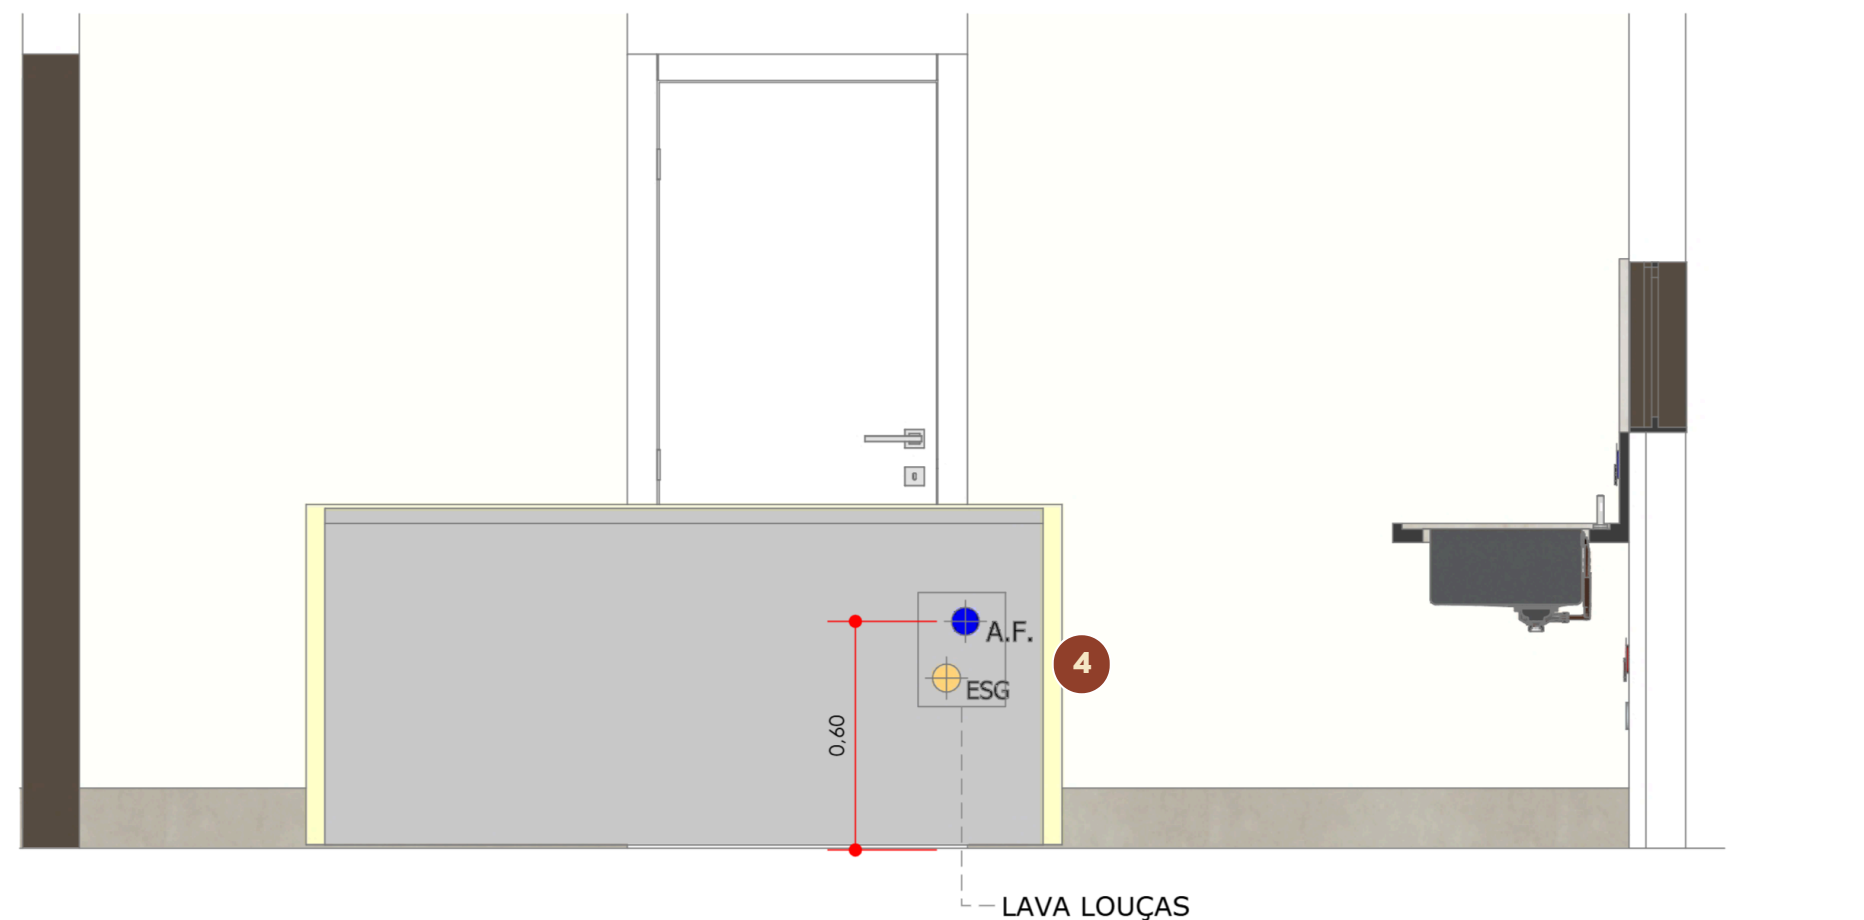

Legenda

- A.F. · Água fria
- A.Q. · Água quente
- ESG · Esgoto
- V.D. · Válvula de descarga
- R.G. · Registro geral
- 1 Selo do ponto / peça
- Cota da prancha original (m)

NÃO COTADO NA PRANCHA ORIGINAL / A CONFIRMAR: valor ausente no caderno original. Não executar sem confirmação da equipe.

Observações técnicas

- OBSERVAÇÃO** Eixo do lava-louças cotado a partir da borda da ilha, não de parede. Referência não inequívoca: conferir na folha original 01/16.
- OBSERVAÇÃO** Na Vista A, a cota de 0,50 m está ligada ao A.Q. da cuba; o A.F. ao lado não tem cota própria.
- COMPATIBILIZAÇÃO** Planta de tomadas: tomada baixa a 0,30 m e média a 1,15 m do piso acabado. Conferir afastamento em relação aos pontos de A.F., A.Q. e ESG sob a bancada antes de fechar as paredes.
- OBSERVAÇÃO** Cotas em metros, reproduzidas do caderno original sem alteração. Alturas medidas a partir do piso acabado.
- NORMAS** NBR 5626 (água fria), NBR 7198 (água quente) e NBR 8160 (esgoto sanitário).

PROJETO
Residência IC · Design de interiores de casa unifamiliar térrea

CLIENTES
Ivan e Carol

ENDEREÇO
Nova Odessa, SP

TIPO DE PLANTA
Planta de eixos hidráulicos e Vistas A, B e C · Cozinha

RESPONSÁVEIS TÉCNICOS
Arq. Lidiane Barbosa · CAU A290220-6
Arq. Isadora Ferrari · CAU A269382-8

DATA
24/09/2026

ORIGEM
Folhas 01 a 04/16 · rev. 01

ESCALAS
1/40 planta · 1/20 vistas


Válidas em A2 a 100%

Conferir as medidas no local

Planta de eixos hidráulicos


ESC 1/40

0 1 2 m

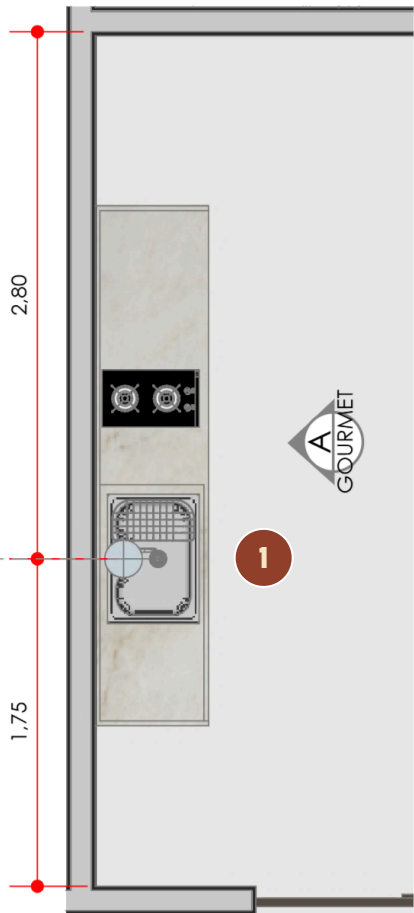EIXO CUBA
TORNEIRA DE BANCADA

Vista A · Gourmet ESC 1/20

0 – 1 m

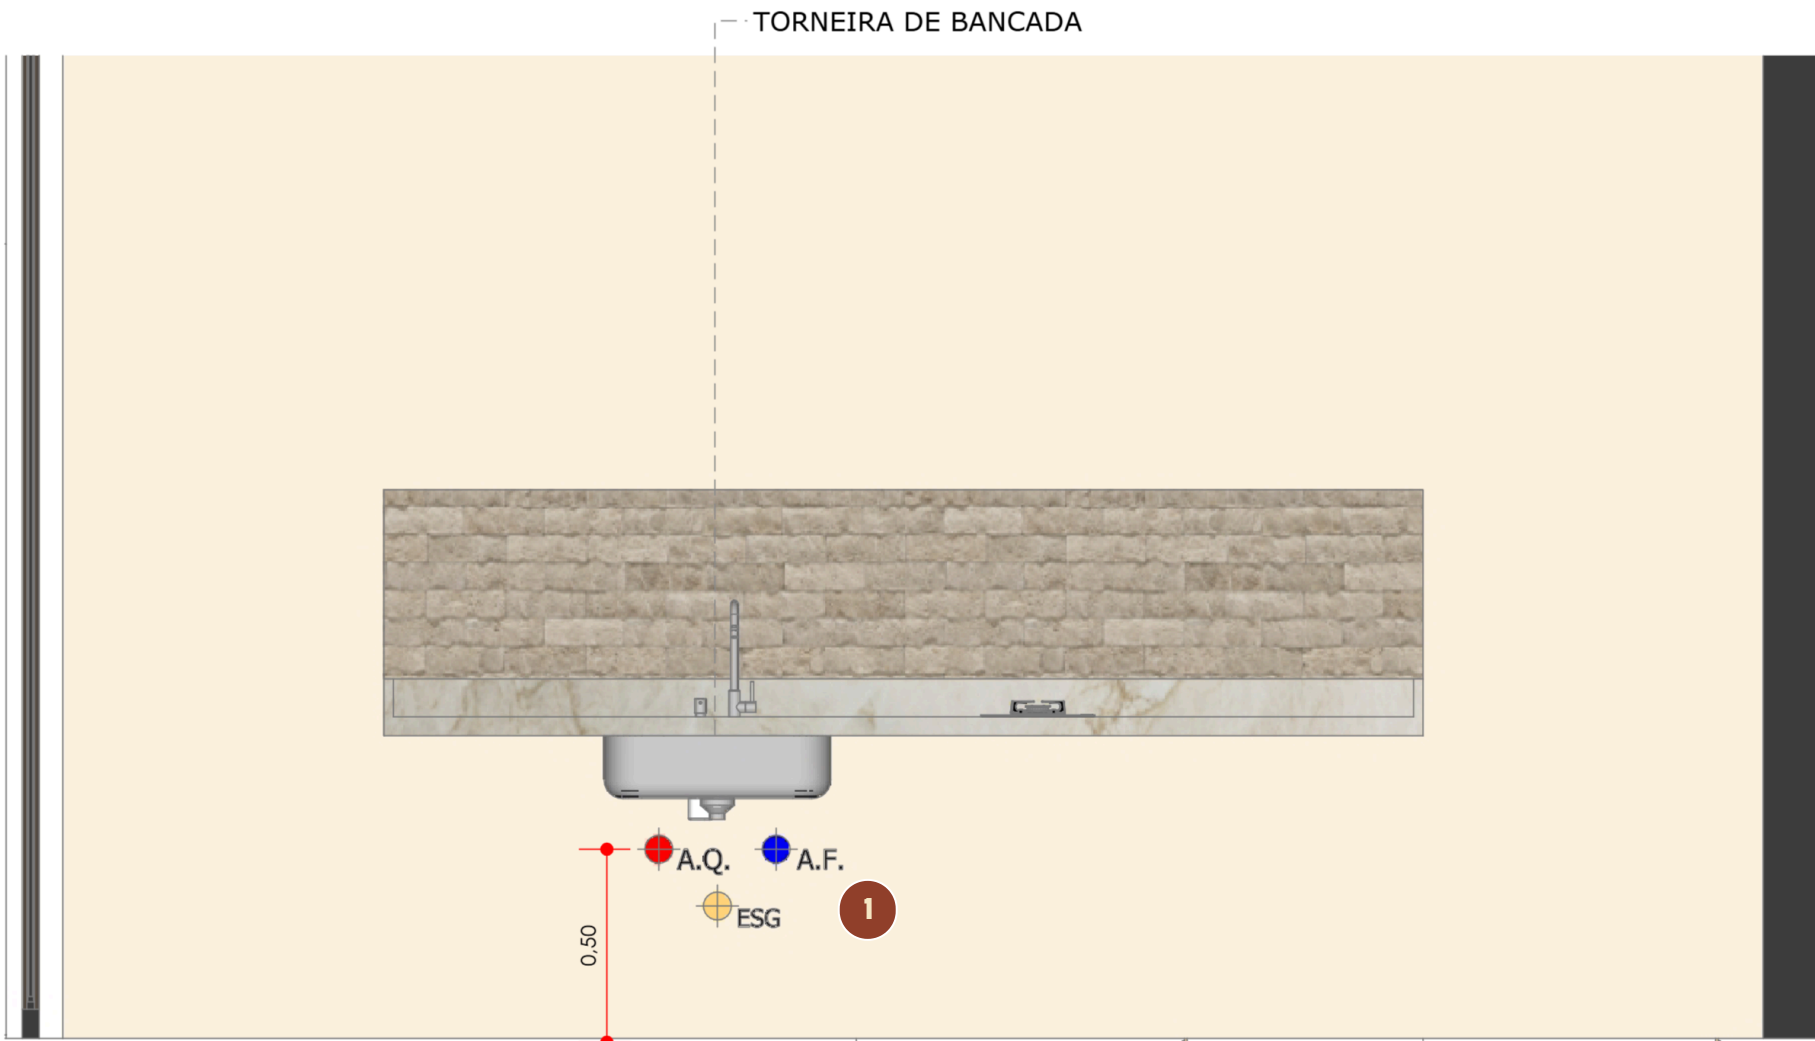

Legenda

- A.F. · Água fria
- A.Q. · Água quente
- ESG · Esgoto
- V.D. · Válvula de descarga
- R.G. · Registro geral
- 1 Selo do ponto / peça
- Cota da prancha original (m)

NÃO COTADO NA PRANCHA ORIGINAL / A CONFIRMAR: valor ausente no caderno original. Não executar sem confirmação da equipe.

Observações técnicas

- OBSERVAÇÃO** A cota de 0,50 m na Vista A está ligada ao A.Q.; A.F. e ESG sem cota própria. Conferir na folha original 06/16.
- COMPATIBILIZAÇÃO** Planta de tomadas: tomada baixa a 0,30 m e média a 1,15 m do piso acabado. Conferir afastamento em relação aos pontos de A.F., A.Q. e ESG sob a bancada antes de fechar as paredes.
- OBSERVAÇÃO** Cotas em metros, reproduzidas do caderno original sem alteração. Alturas medidas a partir do piso acabado.
- NORMAS** NBR 5626 (água fria), NBR 7198 (água quente) e NBR 8160 (esgoto sanitário).

Quadro de pontos

- 1 Cuba · torneira de bancada**
EIXO 2,80 da parede superior; 1,75 até a parede inferior
- A.Q. 0,50
 - A.F. NÃO COTADO NA PRANCHA ORIGINAL / A CONFIRMAR
 - ESG NÃO COTADO NA PRANCHA ORIGINAL / A CONFIRMAR

PROJETO
Residência IC · Design de interiores de casa unifamiliar térrea

CLIENTES

Ivan e Carol

ENDEREÇO

Nova Odessa, SP

TIPO DE PLANTA

Planta de eixos hidráulicos e Vista A · Gourmet

RESPONSÁVEIS TÉCNICOS

Arq. Lidiane Barbosa · CAU A290220-6

Arq. Isadora Ferrari · CAU A269382-8

DATA

24/09/2026

ORIGEM

Folhas 05 e 06/16 · rev. 01

ESCALAS

1/40 planta · 1/20 vistas

Válidas em A2 a 100%


Conferir as medidas no local

Lavanderia

Planta de eixos + Vista A


Planta de eixos hidráulicos

ESC 1/40

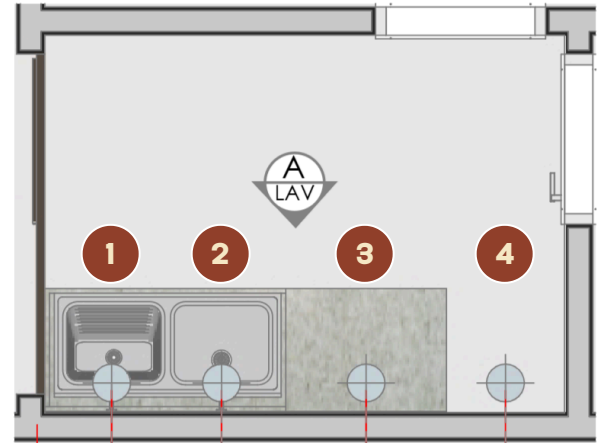

Vista A · Lavanderia

ESC 1/20

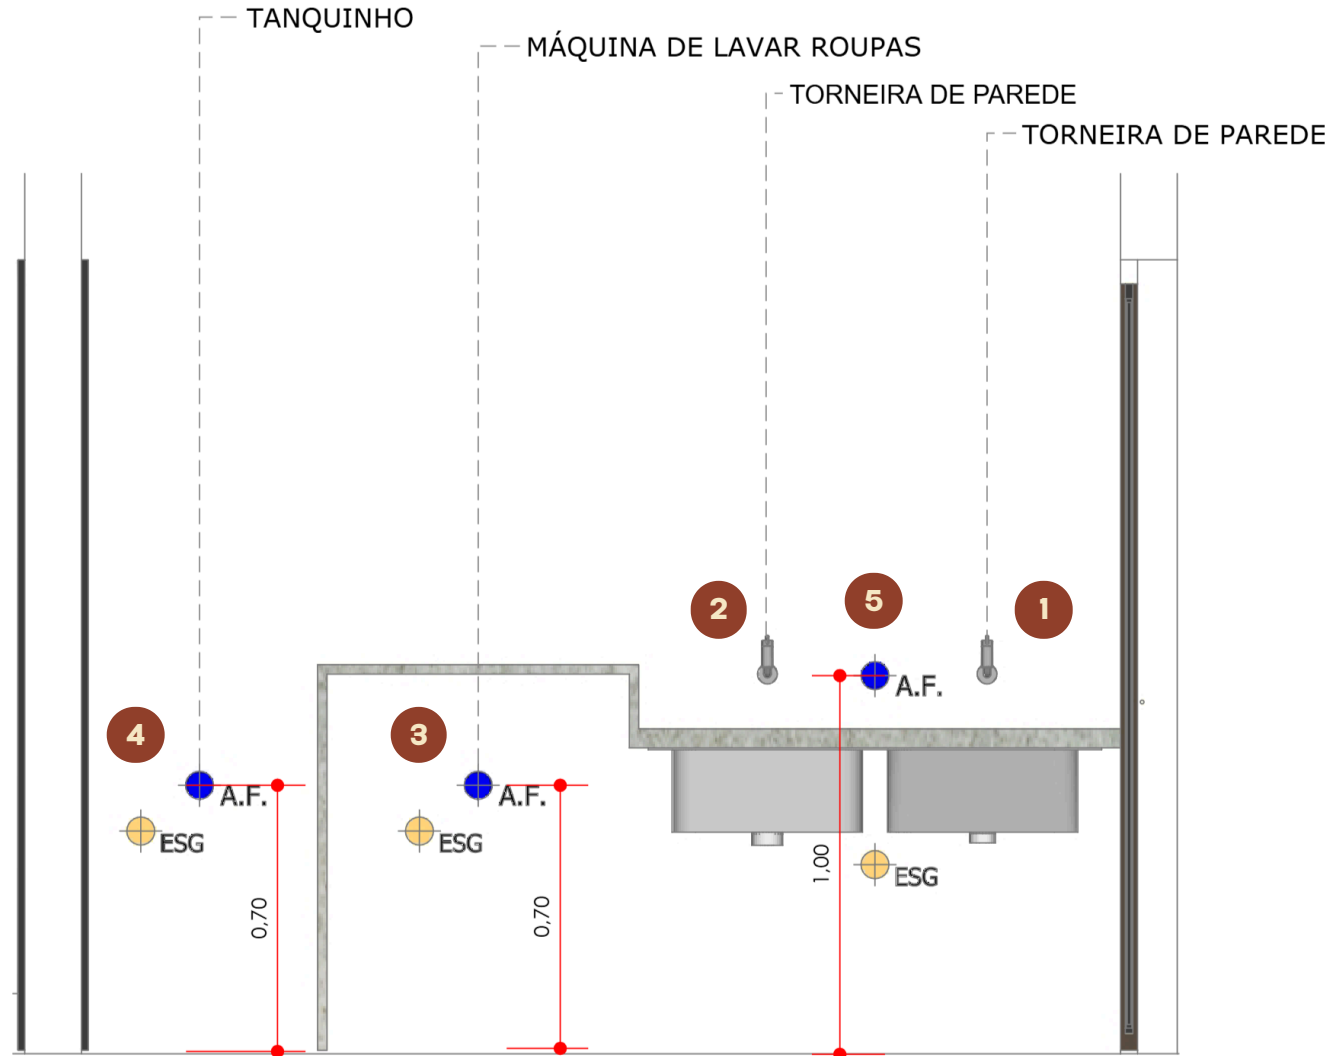

Legenda

- A.F. · Água fria
- A.Q. · Água quente
- ESG · Esgoto
- V.D. · Válvula de descarga
- R.G. · Registro geral
- 1 Selo do ponto / peça
- Cota da prancha original (m)

NÃO COTADO NA PRANCHA ORIGINAL / A CONFIRMAR: valor ausente no caderno original. Não executar sem confirmação da equipe.

Observações técnicas

- PENDÊNCIA** A planta indica dois eixos de torneira de parede (1 e 2), mas a Vista A mostra um único ponto de A.F., a 1,00 m, entre as duas torneiras (5). Reproduzido como no original. Confirmar alimentação e alturas com a equipe.
- OBSERVAÇÃO** Vista A em espelho em relação à planta: o tanquinho (4) fica à direita na planta e à esquerda na vista.
- COMPATIBILIZAÇÃO** Planta de tomadas: tomada baixa a 0,30 m e média a 1,15 m do piso acabado. Conferir afastamento em relação aos pontos de A.F., A.Q. e ESG sob a bancada antes de fechar as paredes.
- OBSERVAÇÃO** Cotas em metros, reproduzidas do caderno original sem alteração. Alturas medidas a partir do piso acabado.
- NORMAS** NBR 5626 (água fria), NBR 7198 (água quente) e NBR 8160 (esgoto sanitário).

Quadro de pontos


- Torneira de parede · tanque**
EIXO 0,40 da parede esquerda
A.F. NÃO COTADO NA PRANCHA ORIGINAL / A CONFIRMAR
- Torneira de parede · tanque**
EIXO 0,60 a partir do eixo 1
A.F. NÃO COTADO NA PRANCHA ORIGINAL / A CONFIRMAR
- Máquina de lavar roupas**
EIXO 0,80 a partir do eixo 2
A.F. 0,70
ESG NÃO COTADO NA PRANCHA ORIGINAL / A CONFIRMAR
- Tanquinho**
EIXO 0,75 a partir do eixo 3
A.F. 0,70
ESG NÃO COTADO NA PRANCHA ORIGINAL / A CONFIRMAR
- Ponto A.F. + ESG da bancada do tanque**
EIXO NÃO COTADO NA PRANCHA ORIGINAL / A CONFIRMAR
A.F. 1,00
ESG NÃO COTADO NA PRANCHA ORIGINAL / A CONFIRMAR

WC 01

Planta de eixos + Vista A


Planta de eixos hidráulicos

ESC 1/40

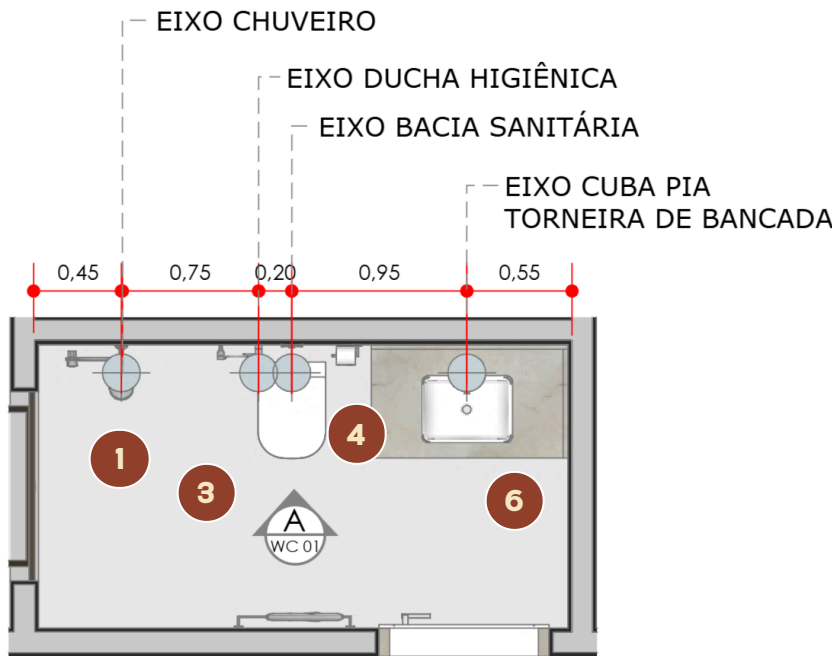

PAREDE DE REFERÊNCIA: parede esquerda, com cotas encadeadas (0,45 · 0,75 · 0,20 · 0,95 · 0,55 até a parede direita).

Vista A · WC 01

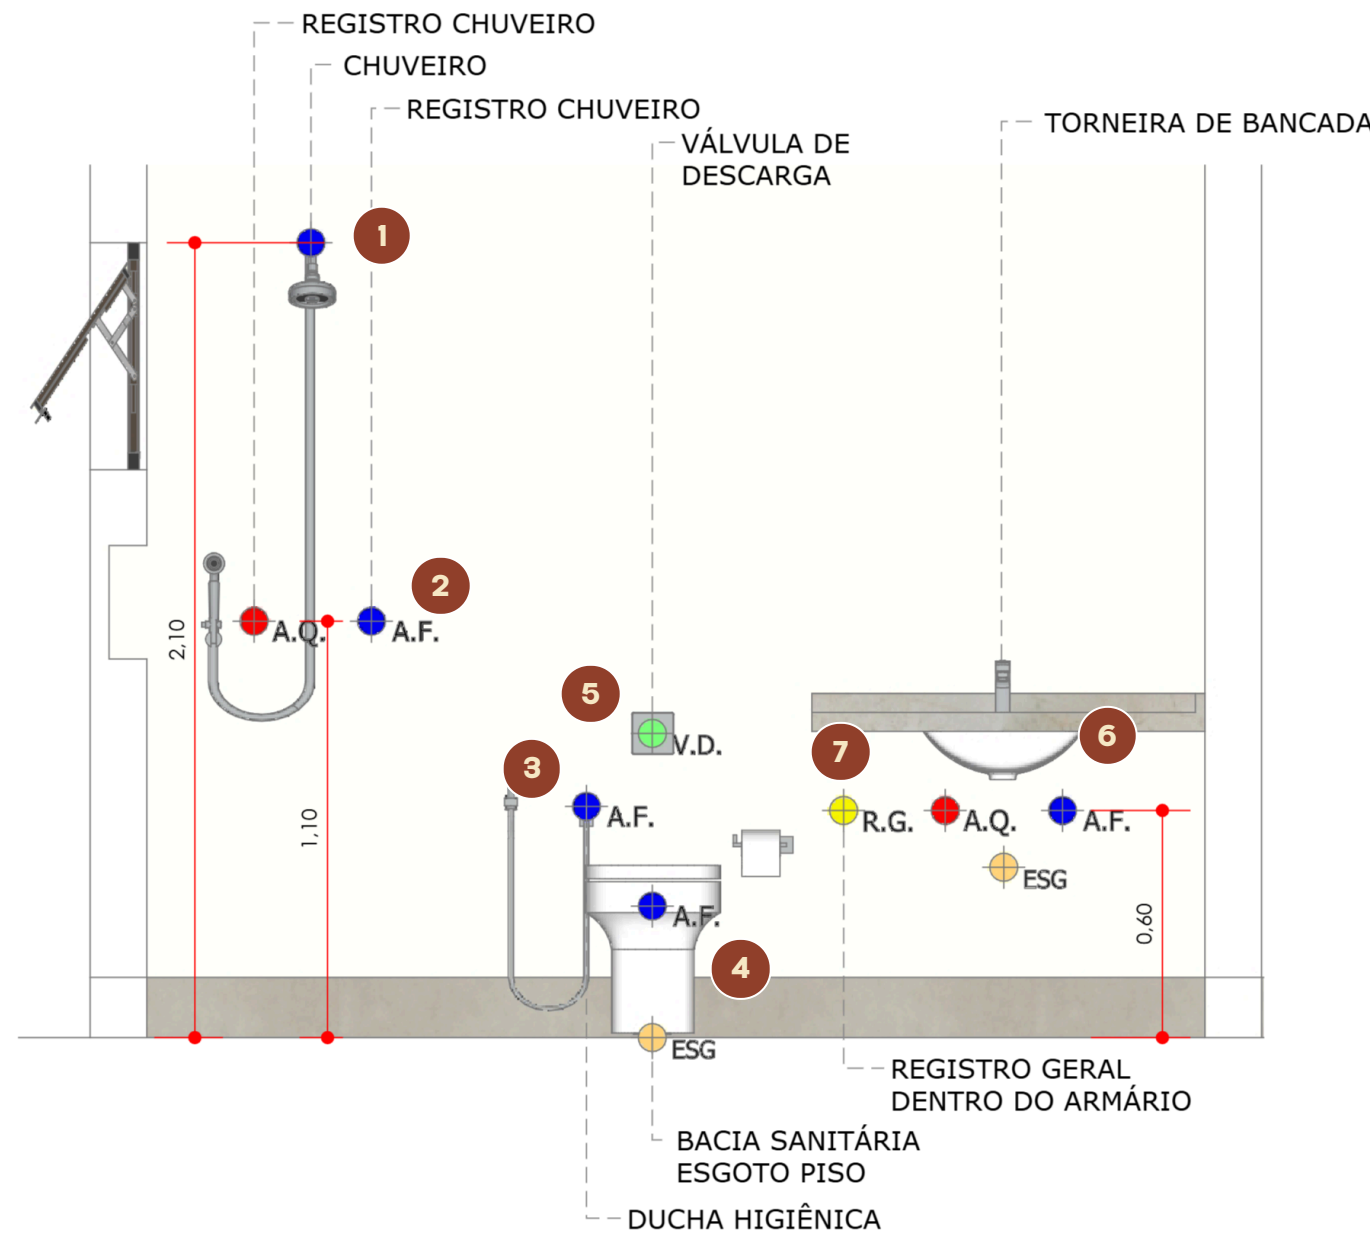

Legenda

- A.F. · Água fria
- A.Q. · Água quente
- ESG · Esgoto
- V.D. · Válvula de descarga
- R.G. · Registro geral
- 1 Selo do ponto / peça
- Cota da prancha original (m)

NÃO COTADO NA PRANCHA ORIGINAL / A CONFIRMAR: valor ausente no caderno original. Não executar sem confirmação da equipe.

Observações técnicas

- OBSERVAÇÃO** Válvula de descarga, ducha higiênica, alimentação da bacia e registro geral sem cota de altura. Eixo em planta de V.D. e R.G. também não cotado. Não executar sem confirmação.
- OBSERVAÇÃO** Cota única de 1,10 m para a linha dos registros do chuveiro (A.Q. e A.F.). Afastamento lateral entre eles não cotado. Conferir na folha original.
- OBSERVAÇÃO** Na Vista A, a cota de 0,60 m está ligada ao A.F. da bancada; A.Q. e R.G. estão na mesma linha, sem cota própria.
- COMPATIBILIZAÇÃO** A legenda da planta de tomadas prevê chuveiro elétrico; esta prancha indica A.Q. no chuveiro. Confirmar o sistema de aquecimento. Tomada média (1,15 m) próxima aos registros do chuveiro (1,10 m): verificar se estão na mesma parede.
- OBSERVAÇÃO** Cotas em metros, reproduzidas do caderno original sem alteração. Alturas medidas a partir do piso acabado.
- NORMAS** NBR 5626 (água fria), NBR 7198 (água quente) e NBR 8160 (esgoto sanitário).

Quadro de pontos

- Chuveiro**
EIXO 0,45 da parede esquerda
A.F. 2,10
- Registros do chuveiro**
EIXO no eixo do chuveiro; afastamento lateral de cada registro NÃO COTADO NA PRANCHA ORIGINAL / A CONFIRMAR
A.Q. 1,10 A.F. 1,10
- Ducha higiênica**
EIXO 0,75 a partir do eixo do chuveiro
A.F. NÃO COTADO NA PRANCHA ORIGINAL / A CONFIRMAR
- Bacia sanitária**
EIXO 0,20 a partir do eixo da ducha
A.F. NÃO COTADO NA PRANCHA ORIGINAL / A CONFIRMAR
ESG no piso
- Válvula de descarga**
EIXO NÃO COTADO NA PRANCHA ORIGINAL / A CONFIRMAR
V.D. NÃO COTADO NA PRANCHA ORIGINAL / A CONFIRMAR
- Cuba pia · torneira de bancada**
EIXO 0,95 a partir do eixo da bacia; 0,55 até a parede direita
A.F. 0,60
A.Q. NÃO COTADO NA PRANCHA ORIGINAL / A CONFIRMAR
ESG NÃO COTADO NA PRANCHA ORIGINAL / A CONFIRMAR
- Registro geral (dentro do armário)**
EIXO NÃO COTADO NA PRANCHA ORIGINAL / A CONFIRMAR
R.G. NÃO COTADO NA PRANCHA ORIGINAL / A CONFIRMAR

PROJETO
Residência IC · Design de interiores de casa unifamiliar térrea

CLIENTES

Ivan e Carol

ENDEREÇO

Nova Odessa, SP

TIPO DE PLANTA

Planta de eixos hidráulicos e Vista A · WC 01

RESPONSÁVEIS TÉCNICOS

Arq. Lidiane Barbosa · CAU A290220-6

Arq. Isadora Ferrari · CAU A269382-8

DATA

24/09/2026

ORIGEM

Folhas 09 e 10/16 · rev. 01

ESCALAS

1/40 planta · 1/20 vistas

Válidas em A2 a 100%


Conferir as medidas no local

WC 02

Planta de eixos + Vista A

Planta de eixos hidráulicos

ESC 1/40

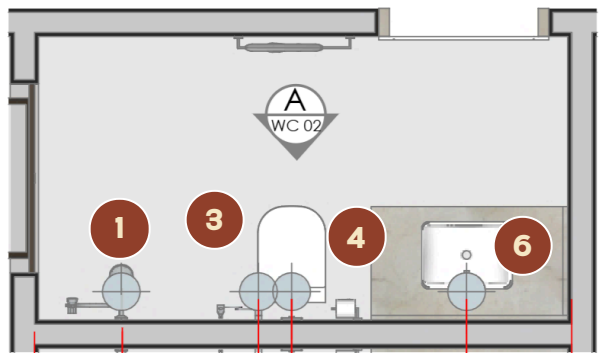EIXO CUBA PIA
TORNEIRA DE BANCADA

EIXO BACIA SANITÁRIA

EIXO DUCHA HIGIÊNICA


EIXO CHUVEIRO

0 1 2m

PAREDE DE REFERÊNCIA: parede esquerda, com cotas encadeadas (0,45 · 0,75 · 0,20 · 0,95 · 0,55 até a parede direita).

Vista A · WC 02

ESC 1/20

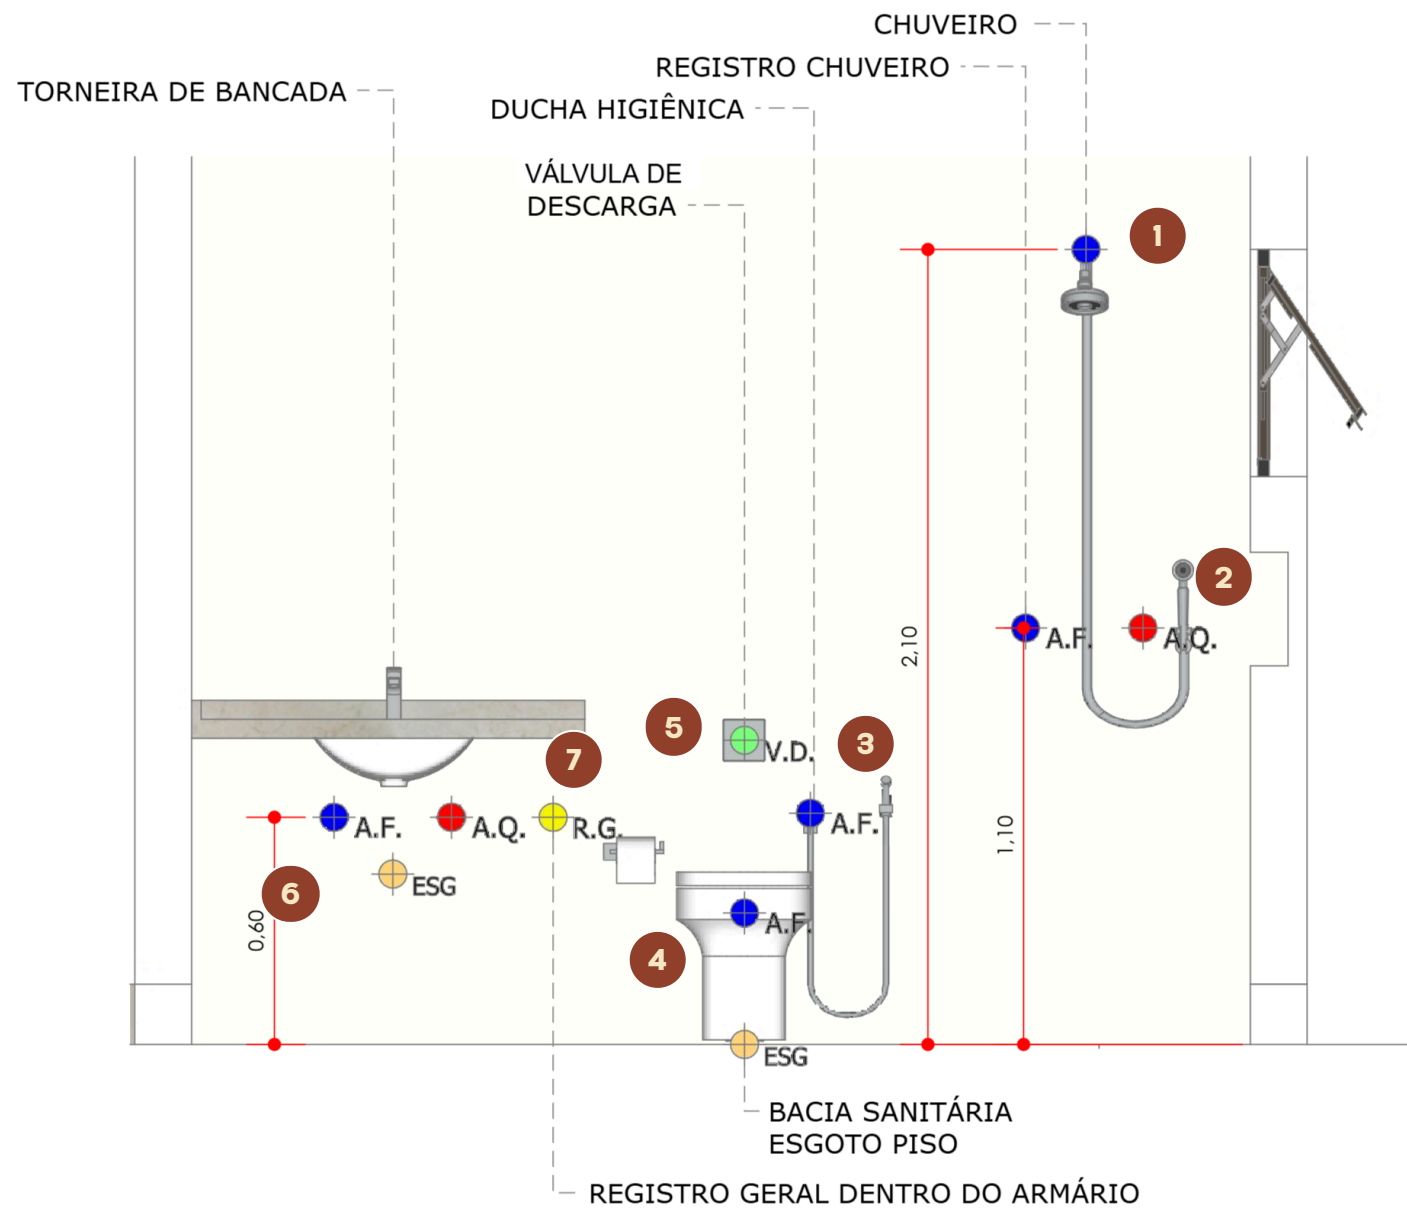

0 – 1 m

Legenda

- A.F. · Água fria
- A.Q. · Água quente
- ESG · Esgoto
- V.D. · Válvula de descarga
- R.G. · Registro geral
- 1 Selo do ponto / peça
- Cota da prancha original (m)

NÃO COTADO NA PRANCHA ORIGINAL / A CONFIRMAR: valor ausente no caderno original. Não executar sem confirmação da equipe.

Observações técnicas

- OBSERVAÇÃO** Válvula de descarga, ducha higiênica, alimentação da bacia e registro geral sem cota de altura. Eixo em planta de V.D. e R.G. também não cotado. Não executar sem confirmação.
- OBSERVAÇÃO** Cota única de 1,10 m para a linha dos registros do chuveiro (A.Q. e A.F.). Afastamento lateral entre eles não cotado. Conferir na folha original.
- OBSERVAÇÃO** Mesmas cotas do WC 01, com disposição espelhada: peças junto à parede inferior da planta. Vista A em espelho em relação à planta.
- COMPATIBILIZAÇÃO** A legenda da planta de tomadas prevê chuveiro elétrico; esta prancha indica A.Q. no chuveiro. Confirmar o sistema de aquecimento. Tomada média (1,15 m) próxima aos registros do chuveiro (1,10 m): verificar se estão na mesma parede.
- OBSERVAÇÃO** Cotas em metros, reproduzidas do caderno original sem alteração. Alturas medidas a partir do piso acabado.
- NORMAS** NBR 5626 (água fria), NBR 7198 (água quente) e NBR 8160 (esgoto sanitário).

Quadro de pontos

- Chuveiro**
EIXO 0,45 da parede esquerda
A.F. 2,10
- Registros do chuveiro**
EIXO no eixo do chuveiro; afastamento lateral de cada registro NÃO COTADO NA PRANCHA ORIGINAL / A CONFIRMAR
A.F. 1,10 A.Q. 1,10
- Ducha higiênica**
EIXO 0,75 a partir do eixo do chuveiro
A.F. NÃO COTADO NA PRANCHA ORIGINAL / A CONFIRMAR
- Bacia sanitária**
EIXO 0,20 a partir do eixo da ducha
A.F. NÃO COTADO NA PRANCHA ORIGINAL / A CONFIRMAR
ESG no piso
- Válvula de descarga**
EIXO NÃO COTADO NA PRANCHA ORIGINAL / A CONFIRMAR
V.D. NÃO COTADO NA PRANCHA ORIGINAL / A CONFIRMAR
- Cuba pia · torneira de bancada**
EIXO 0,95 a partir do eixo da bacia; 0,55 até a parede direita
A.F. 0,60
A.Q. NÃO COTADO NA PRANCHA ORIGINAL / A CONFIRMAR
ESG NÃO COTADO NA PRANCHA ORIGINAL / A CONFIRMAR
- Registro geral (dentro do armário)**
EIXO NÃO COTADO NA PRANCHA ORIGINAL / A CONFIRMAR
R.G. NÃO COTADO NA PRANCHA ORIGINAL / A CONFIRMAR

DUAS
duas
design
& arq

PRANCHA

05/07

REVISÃO 02

PROJETO
Residência IC · Design de interiores de casa unifamiliar térrea

CLIENTES
Ivan e Carol

ENDEREÇO
Nova Odessa, SP

TIPO DE PLANTA
Planta de eixos hidráulicos e Vista A · WC 02

RESPONSÁVEIS TÉCNICOS
Arq. Lidiane Barbosa · CAU A290220-6
Arq. Isadora Ferrari · CAU A269382-8

DATA
24/09/2026

ORIGEM
Folhas 11 e 12/16 · rev. 01

ESCALAS
1/40 planta · 1/20 vistas

Válidas em A2 a 100%

Conferir as medidas no local

WC Suíte Master

Planta de eixos + Vista A

Planta de eixos hidráulicos


ESC 1/40



PAREDE DE REFERÊNCIA: parede superior, com cotas encadeadas (0,25 · 0,20 · 1,15 · 1,25 · 0,55 até a parede inferior).

Vista A · WC Suíte Master

ESC 1/20

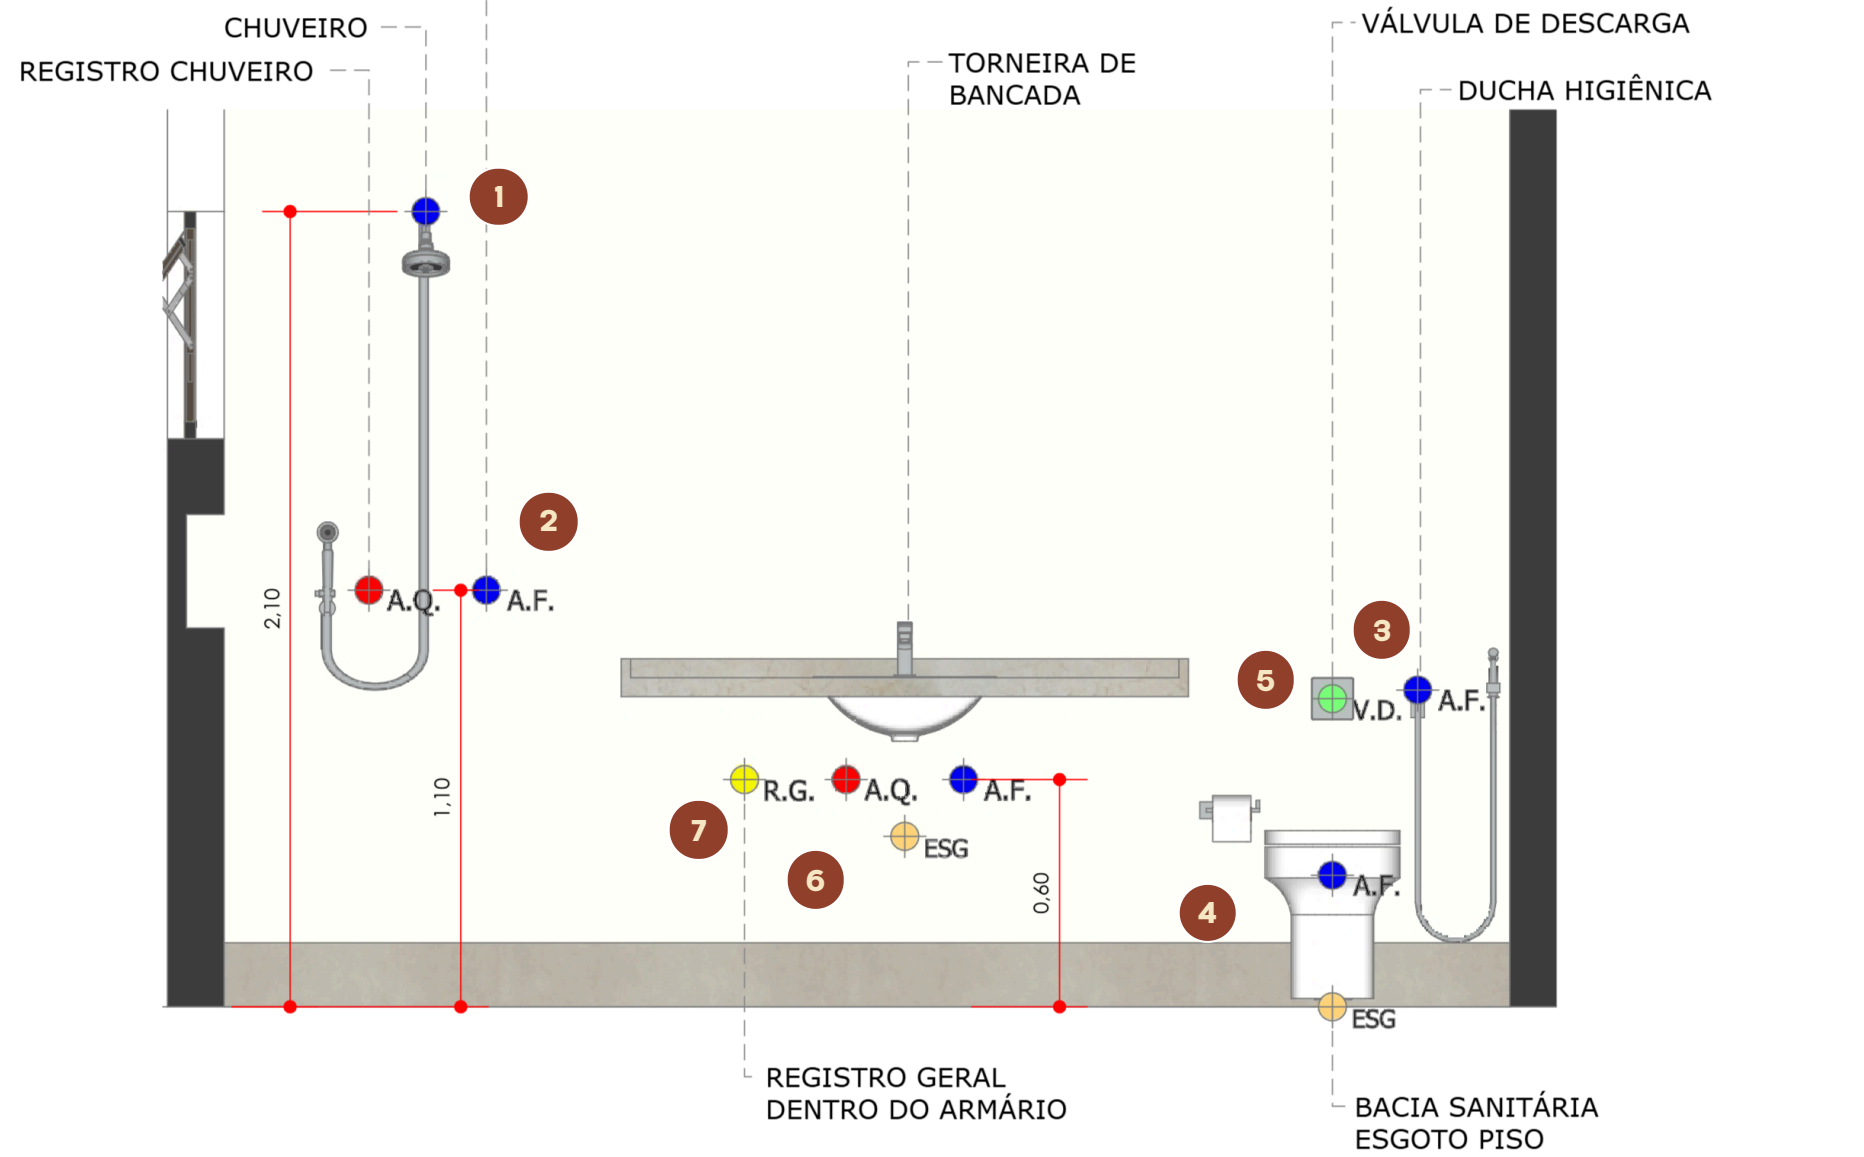

Legenda

- A.F. · Água fria
- A.Q. · Água quente
- ESG · Esgoto
- V.D. · Válvula de descarga
- R.G. · Registro geral
- 1 Selo do ponto / peça
- Cota da prancha original (m)

NÃO COTADO NA PRANCHA ORIGINAL / A CONFIRMAR: valor ausente no caderno original. Não executar sem confirmação da equipe.

Observações técnicas

- PENDÊNCIA** Nomenclatura: o caderno original chama este ambiente de "WC Casal", fora da numeração oficial de banheiros (WC 01, WC 02, WC Externo). Esta prancha adota "WC Suíte Master". Confirmar com a equipe.
- OBSERVAÇÃO** Válvula de descarga, ducha higiênica, alimentação da bacia e registro geral sem cota de altura. Eixo em planta de V.D. e R.G. também não cotado. Não executar sem confirmação.
- OBSERVAÇÃO** Cota única de 1,10 m para a linha dos registros do chuveiro (A.Q. e A.F.). Afastamento lateral entre eles não cotado. Conferir na folha original.
- COMPATIBILIZAÇÃO** A legenda da planta de tomadas prevê chuveiro elétrico; esta prancha indica A.Q. no chuveiro. Confirmar o sistema de aquecimento. Tomada média (1,15 m) próxima aos registros do chuveiro (1,10 m): verificar se estão na mesma parede.
- OBSERVAÇÃO** Cotas em metros, reproduzidas do caderno original sem alteração. Alturas medidas a partir do piso acabado.
- NORMAS** NBR 5626 (água fria), NBR 7198 (água quente) e NBR 8160 (esgoto sanitário).

Quadro de pontos

- Chuveiro**
EIXO 1,25 a partir do eixo da cuba; 0,55 até a parede inferior
A.F. 2,10
- Registros do chuveiro**
EIXO no eixo do chuveiro; afastamento lateral de cada registro NÃO COTADO NA PRANCHA ORIGINAL / A CONFIRMAR
A.Q. 1,10 A.F. 1,10
- Ducha higiênica**
EIXO 0,25 da parede superior
A.F. NÃO COTADO NA PRANCHA ORIGINAL / A CONFIRMAR
- Bacia sanitária**
EIXO 0,20 a partir do eixo da ducha
A.F. NÃO COTADO NA PRANCHA ORIGINAL / A CONFIRMAR
ESG no piso
- Válvula de descarga**
EIXO NÃO COTADO NA PRANCHA ORIGINAL / A CONFIRMAR
V.D. NÃO COTADO NA PRANCHA ORIGINAL / A CONFIRMAR
- Cuba pia · torneira de bancada**
EIXO 1,15 a partir do eixo da bacia
A.F. 0,60
A.Q. NÃO COTADO NA PRANCHA ORIGINAL / A CONFIRMAR
ESG NÃO COTADO NA PRANCHA ORIGINAL / A CONFIRMAR
- Registro geral (dentro do armário)**
EIXO NÃO COTADO NA PRANCHA ORIGINAL / A CONFIRMAR
R.G. NÃO COTADO NA PRANCHA ORIGINAL / A CONFIRMAR

PROJETO
Residência IC · Design de interiores de casa unifamiliar térrea

CLIENTES
Ivan e Carol

ENDEREÇO
Nova Odessa, SP

TIPO DE PLANTA
Planta de eixos hidráulicos e Vista A · WC Suíte Master (original: WC Casal)

RESPONSÁVEIS TÉCNICOS
Arq. Lidiane Barbosa · CAU A290220-6
Arq. Isadora Ferrari · CAU A269382-8

DATA
24/09/2026

ORIGEM
Folhas 13 e 14/16 · rev. 01

ESCALAS
1/40 planta · 1/20 vistas

Válidas em A2 a 100%

Conferir as medidas no local


WC Externo

Planta de eixos + Vista A

Planta de eixos hidráulicos

ESC 1/40

0 1 2 m

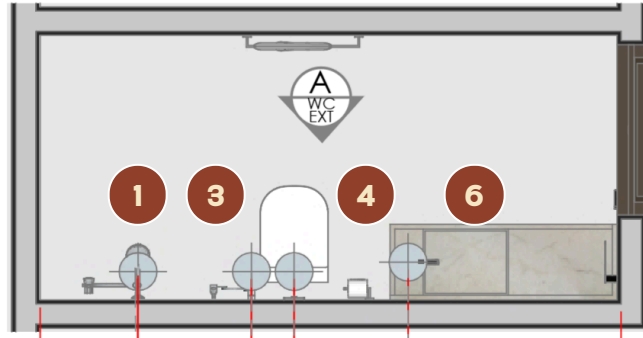

EIXO TORNEIRA DE BANCADA

EIXO BACIA SANITÁRIA

EIXO DUCHA HIGIÊNICA


EIXO CHUVEIRO

PAREDE DE REFERÊNCIA: parede esquerda, com cotas encadeadas (0,55 · 0,60 · 0,20 · 0,60 · 1,15 até a parede direita).

Vista A · WC Externo

ESC 1/20

0 – 1 m

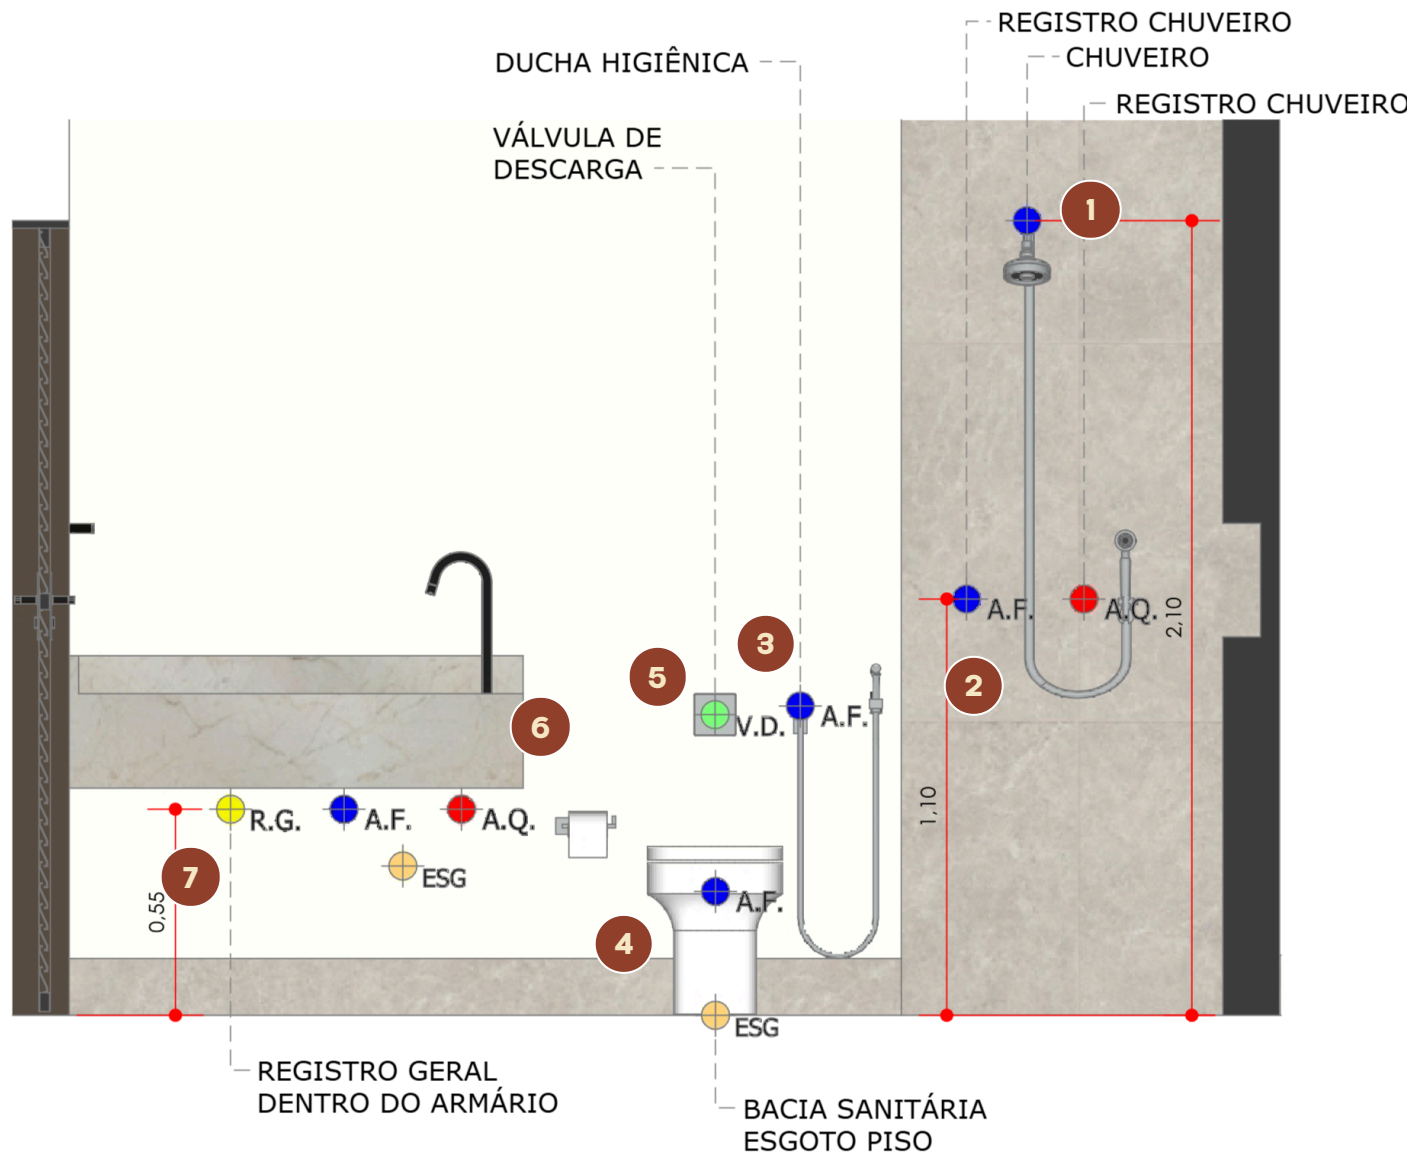

Legenda

- A.F. · Água fria
- A.Q. · Água quente
- ESG · Esgoto
- V.D. · Válvula de descarga
- R.G. · Registro geral
- 1 Selo do ponto / peça
- Cota da prancha original (m)

NÃO COTADO NA PRANCHA ORIGINAL / A CONFIRMAR: valor ausente no caderno original. Não executar sem confirmação da equipe.

Observações técnicas

- OBSERVAÇÃO** Na Vista A, a cota de 0,55 m está ligada ao R.G.; A.F. e A.Q. da bancada estão na mesma linha, sem cota própria. Valor diferente dos demais WCs (0,60 m), conforme original: conferir na folha 16/16.
- OBSERVAÇÃO** Válvula de descarga, ducha higiênica e alimentação da bacia sem cota de altura. Eixo em planta de V.D. e R.G. não cotado. Não executar sem confirmação.
- OBSERVAÇÃO** Cota única de 1,10 m para a linha dos registros do chuveiro (A.Q. e A.F.). Afastamento lateral entre eles não cotado.
- COMPATIBILIZAÇÃO** A legenda da planta de tomadas prevê chuveiro elétrico; esta prancha indica A.Q. no chuveiro. Confirmar o sistema de aquecimento. Tomada média (1,15 m) próxima aos registros do chuveiro (1,10 m): verificar se estão na mesma parede.
- OBSERVAÇÃO** Cotas em metros, reproduzidas do caderno original sem alteração. Alturas medidas a partir do piso acabado.
- NORMAS** NBR 5626 (água fria), NBR 7198 (água quente) e NBR 8160 (esgoto sanitário).

Quadro de pontos

- Chuveiro**
EIXO 0,55 da parede esquerda
A.F. 2,10
- Registros do chuveiro**
EIXO no eixo do chuveiro; afastamento lateral de cada registro NÃO COTADO NA PRANCHA ORIGINAL / A CONFIRMAR
A.F. 1,10 A.Q. 1,10
- Ducha higiênica**
EIXO 0,60 a partir do eixo do chuveiro
A.F. NÃO COTADO NA PRANCHA ORIGINAL / A CONFIRMAR
- Bacia sanitária**
EIXO 0,20 a partir do eixo da ducha
A.F. NÃO COTADO NA PRANCHA ORIGINAL / A CONFIRMAR
ESG no piso
- Válvula de descarga**
EIXO NÃO COTADO NA PRANCHA ORIGINAL / A CONFIRMAR
V.D. NÃO COTADO NA PRANCHA ORIGINAL / A CONFIRMAR
- Torneira de bancada**
EIXO 0,60 a partir do eixo da bacia; 1,15 até a parede direita
A.F. NÃO COTADO NA PRANCHA ORIGINAL / A CONFIRMAR
A.Q. NÃO COTADO NA PRANCHA ORIGINAL / A CONFIRMAR
ESG NÃO COTADO NA PRANCHA ORIGINAL / A CONFIRMAR
- Registro geral (dentro do armário)**
EIXO NÃO COTADO NA PRANCHA ORIGINAL / A CONFIRMAR
R.G. 0,55

PROJETO
Residência IC · Design de interiores de casa unifamiliar térrea

CLIENTES
Ivan e Carol

ENDEREÇO
Nova Odessa, SP

TIPO DE PLANTA
Planta de eixos hidráulicos e Vista A · WC Externo

RESPONSÁVEIS TÉCNICOS
Arq. Lidiane Barbosa · CAU A290220-6
Arq. Isadora Ferrari · CAU A269382-8

DATA
24/09/2026

ORIGEM
Folhas 15 e 16/16 · rev. 01

ESCALAS
1/40 planta · 1/20 vistas

Válidas em A2 a 100%

Conferir as medidas no local