


01 Planta de pontos hidráulicos

Escala 1:100 · plotagem em A2 · posições conforme Planta Pontos Hidráulicos (29/09/2026)

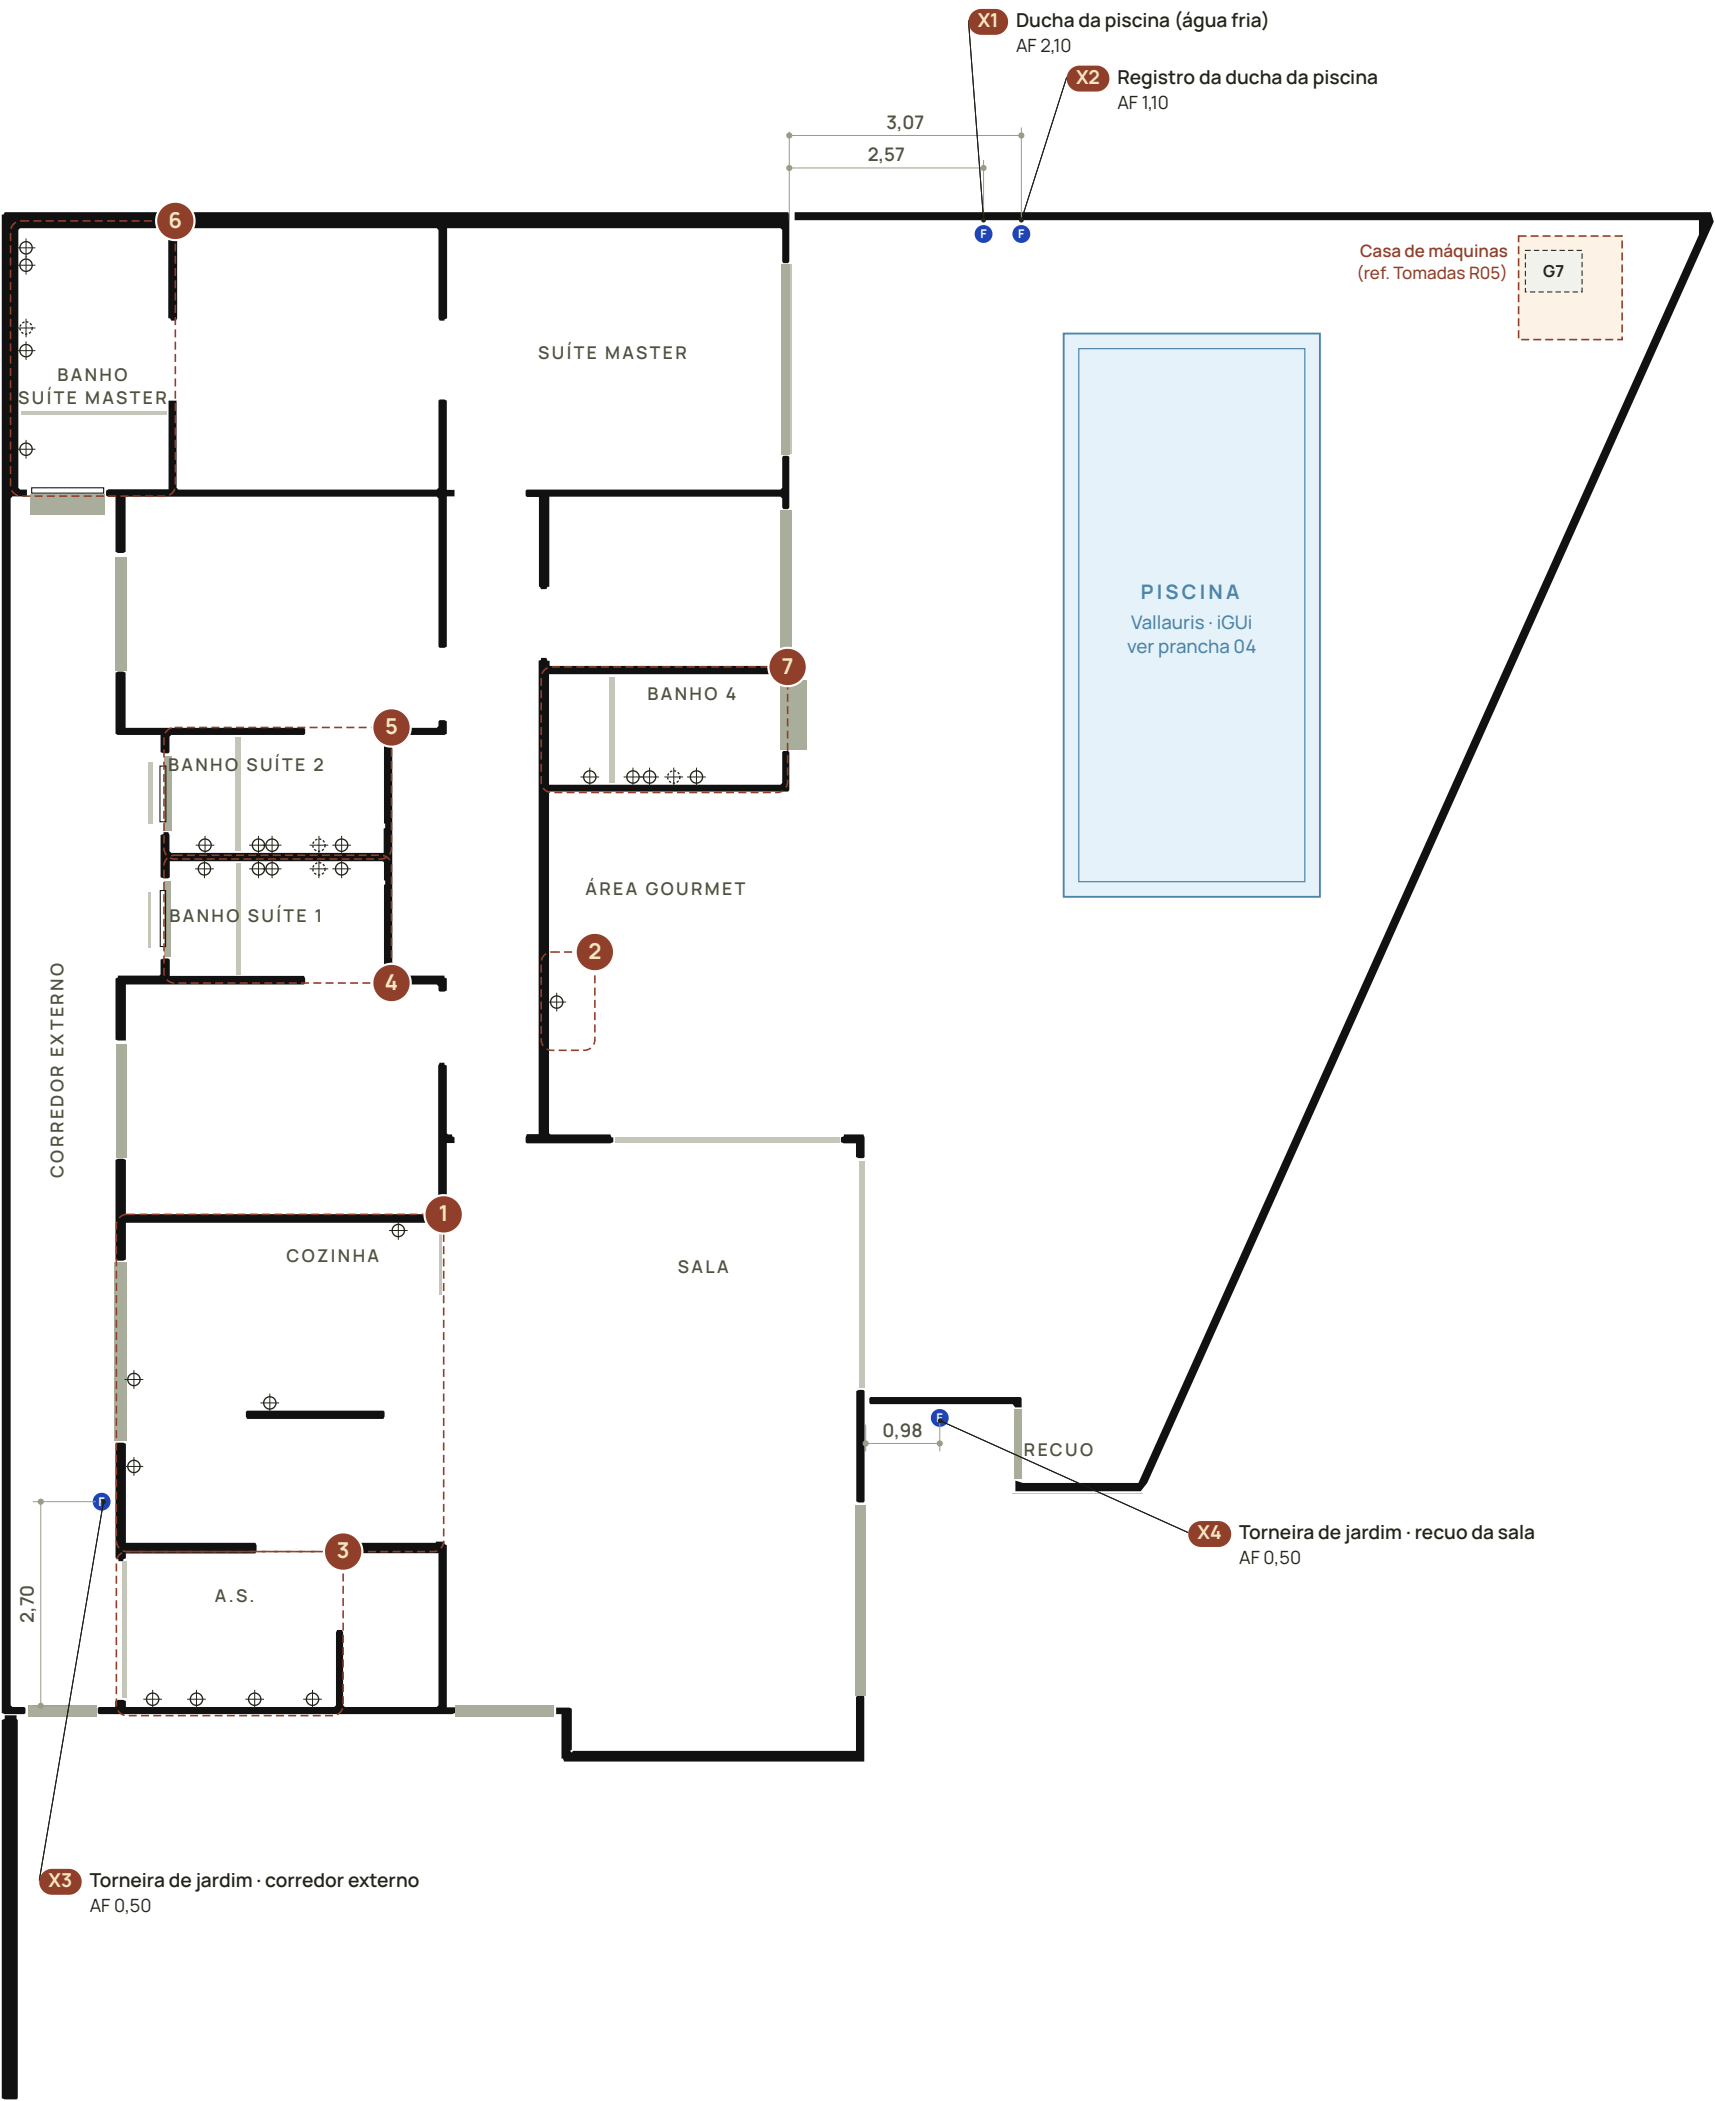

Pontos por ambiente

QUADRO 1

| Nº | AMBIENTE · PONTOS                                                                        | PRANCHA |
|----|------------------------------------------------------------------------------------------|---------|
| 1  | Cozinha<br>C1 a C4 · filtro, cuba, geladeira e lava-louças (mureta)                      | 02      |
| 2  | Área Gourmet<br>G1 · cuba com misturador                                                 | 02      |
| 3  | A.S. · Área de serviço<br>L1 a L5 · torneiras do tanque, lava e seca, máquina, tanquinho | 02      |
| 4  | Banho Suíte 1<br>B1.1 a B1.5 · chuveiro, ducha higiênica, bacia, cuba, registro          | 03      |
| 5  | Banho Suíte 2<br>B2.1 a B2.5 · espelhado em relação ao Banho Suíte 1                     | 03      |
| 6  | Banho Suíte Master<br>BM.1 a BM.5 · chuveiro, ducha higiênica, bacia, cuba, registro     | 03      |
| 7  | Banho 4<br>B4.1 a B4.5 · chuveiro, ducha higiênica, bacia, cuba de sobrepor, registro    | 03      |
| 8  | Piscina<br>Ducha e registro (X1, X2), skimmer, retorno, reposição, ladrão, dreno         | 04      |

Planta: selos em terracota indicam a ampliação de cada ambiente; o círculo com cruz marca o eixo de cada ponto. Pontos externos X1 a X4 cotados nesta prancha (Quadro 1A).

Pontos externos

QUADRO 1A

| Nº | PONTO · POSIÇÃO                                                                                             | ALTURA |
|----|---|--------|
| X1 | Ducha da piscina (água fria)<br>2,57 da face externa da parede da Suíte Master · no muro.                   | 2,10 m |
| X2 | Registro da ducha da piscina<br>3,07 da face externa da parede da Suíte Master · no muro.                   | 1,10 m |
| X3 | Torneira de jardim · corredor externo<br>2,70 do alinhamento do portão · face externa da parede da cozinha. | 0,50 m |
| X4 | Torneira de jardim · recuo da sala<br>0,98 da face externa da parede da sala.                               | 0,50 m |

Ducha de água fria junto à piscina (kit chuveirão só água fria): saída 2,10 e registro 1,10, confirmados em 02/10/2026.

Fontes das alturas

QUADRO 1B

- Caderno Hidráulica Detalhe · Rev. 02 · 24/09/2026
- Definição do cliente · 30/09 e 02/10/2026
- Padrão do escritório (R02) · confirmado em 30/09/2026

Cada altura nos quadros das pranchas 02 a 04 traz a letra da sua fonte. Posições: Planta Pontos Hidráulicos (29/09/2026).

R02 (02/10/2026): bacias Roca ONA com caixa acoplada (sem válvula de descarga); lavatórios e gourmet com misturador AF/AQ; lava-louças na face da mureta; nomes dos ambientes conforme a elétrica; CAU corrigido. R03 (02/10/2026): ponto L2 da A.S. eliminado.

Legenda

QUADRO 2

|                               |                              |
|-------------------------------|------------------------------|
| Água fria                     | Eixo de ponto (planta geral) |
| Água quente                   | Ponto com eixo sem cota      |
| Esgoto                        | Código do ponto              |
| Registro geral                | Ampliação (Quadro 1)         |
| Saída de chuveiro (misturada) | Cota em metros               |
|                               | Alvenaria                    |
|                               | Janela / vidro               |

Letra no círculo = serviço. Altura do piso acabado ao eixo do ponto.

Observações técnicas

QUADRO 3

1. Escopo

Prancha de localização de pontos. Não é projeto de dimensionamento: diâmetros, trajetões, declividades, ventilação, caixas e ramais seguem o projeto hidrossanitário do responsável técnico.

2. Posições

Cotas em metros, a partir da face da parede indicada em cada ponto. Os pontos dos ambientes estão cotados nas ampliações (pranchas 02 e 03); os externos, nesta prancha.

3. Alturas

Do piso acabado ao eixo do ponto. A fonte de cada valor está no Quadro 1B.

4. Chuveiros

Kit Deca Acqua Plus com misturador de duas alavancas (água quente e fria); registros já executados. Sem chuveiro elétrico.

5. Registro geral

Dentro do armário da bancada de cada banheiro, a 0,55 m. Eixo sem cota: definir com a marcenaria.

6. Compatibilização

Pontos elétricos conforme a prancha de Tomadas R05. Manter no mínimo 0,30 m entre tomadas e pontos de água e esgoto. Conferir as medidas no local antes de fechar as paredes.

7. Normas

NBR 5626 (água fria e água quente), NBR 8160 (esgoto sanitário) e NBR 10339 (piscinas).



CARIMBO

PROJETO  
Residência Ivan e Ana Neris  
Nova Odessa – SP

RESPONSÁVEIS TÉCNICAS  
Lidiane Barbosa · CAU A290220-6  
Isadora Ferrari · CAU A263982-8

PLANTA  
Pontos hidráulicos · geral

ESCALA  
1:100 · folha A2

DATA  
02/10/2026

PRANCHA  
01/04


REVISÃO  
R03

0 — 5 m

Conferir as medidas no local


1 Cozinha

Escala 1:25 · pontos C1 a C4

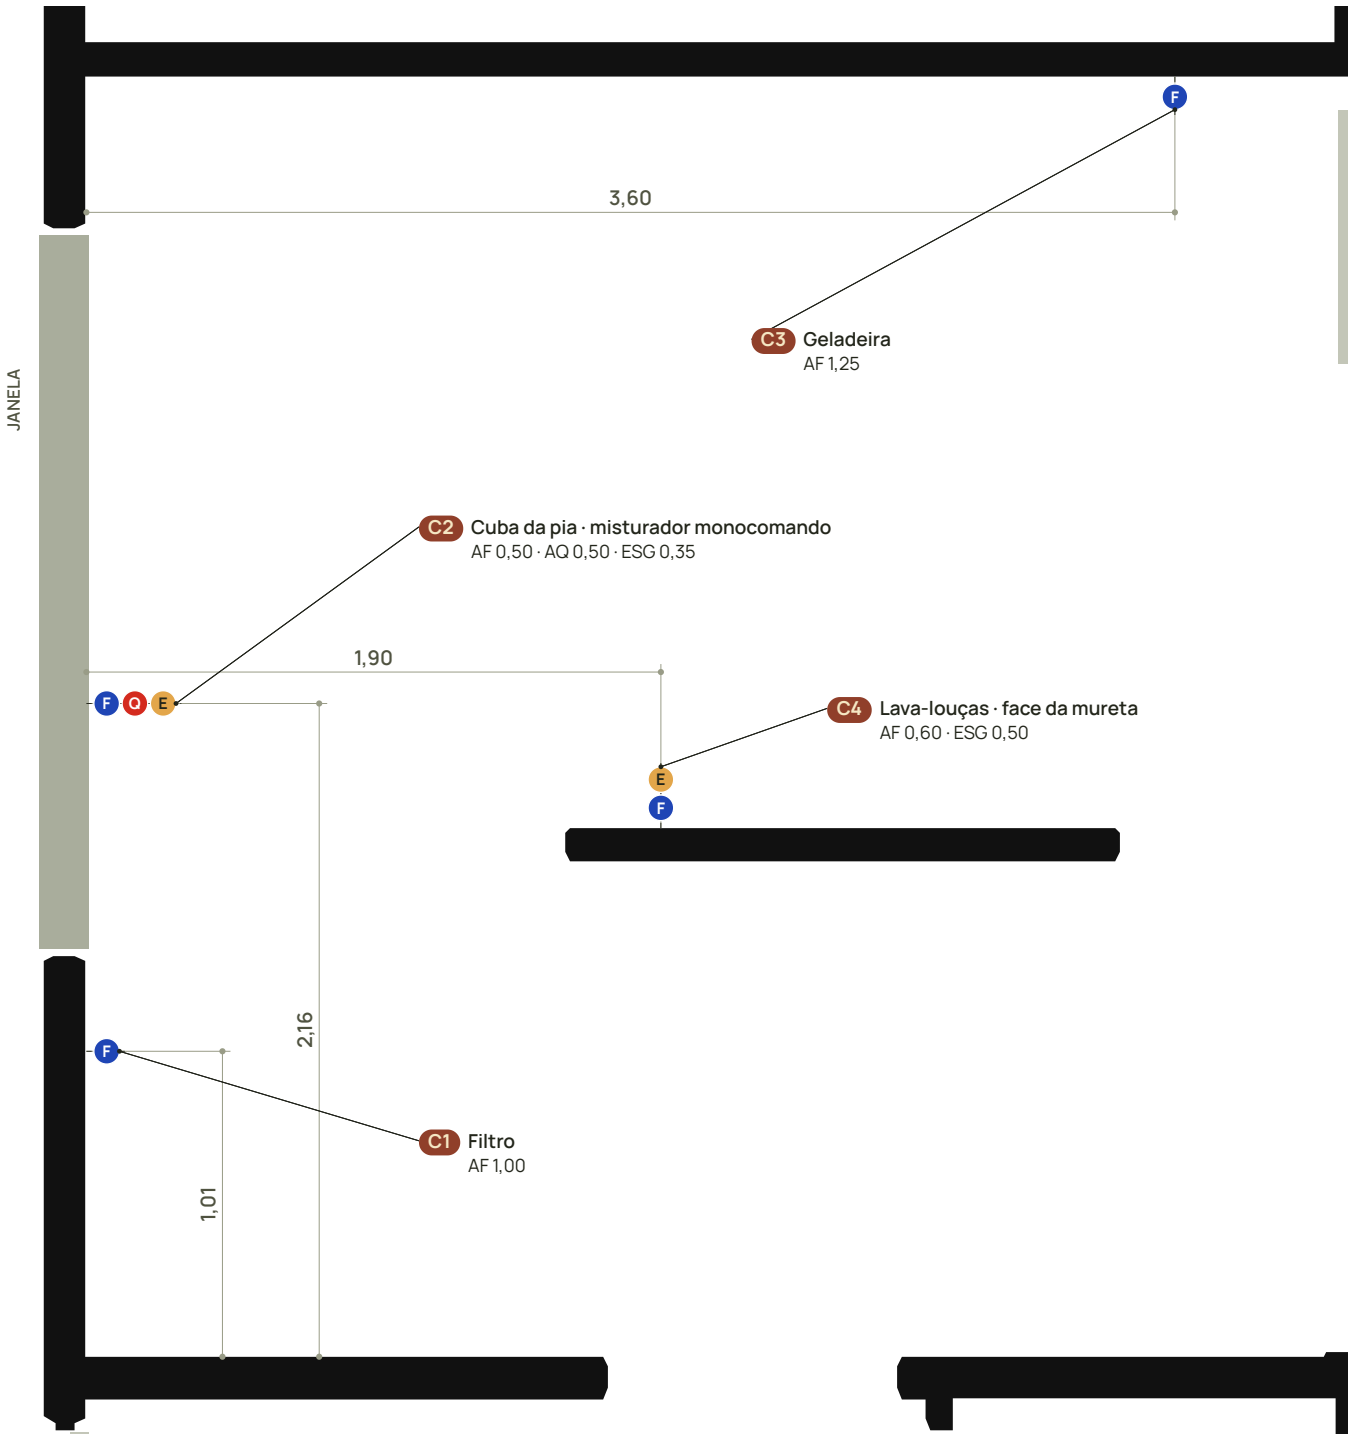


2 Área Gourmet

Escala 1:25 · ponto G1

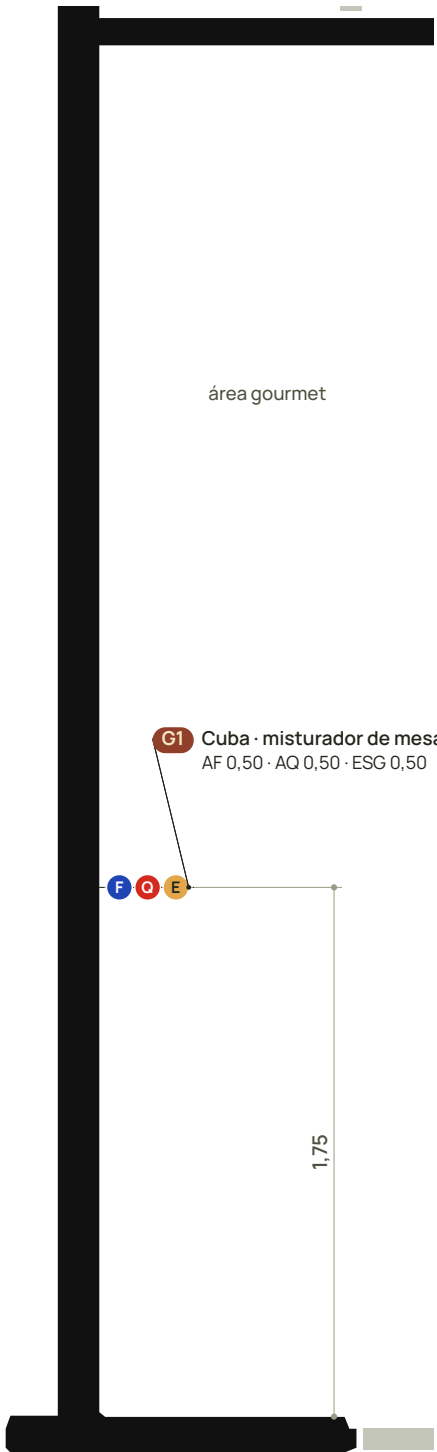


3 A.S. · Área de serviço

Escala 1:25 · pontos L1, L3, L4 e L5

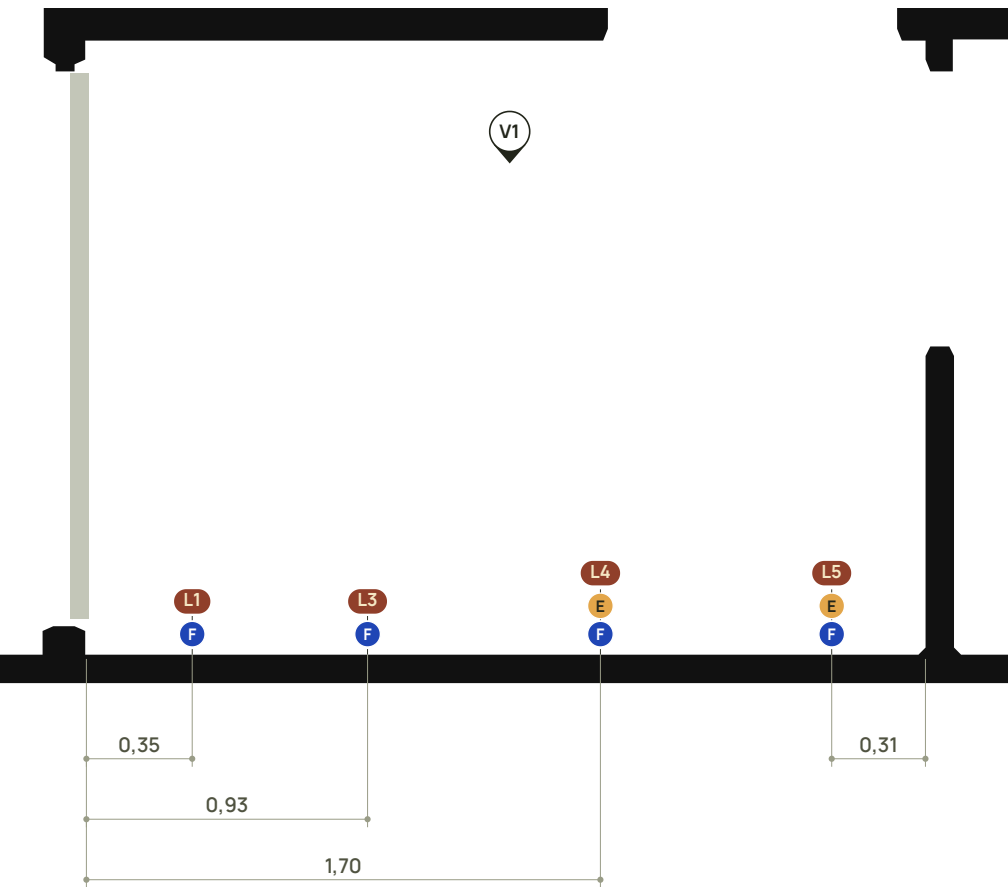

V1 Vista da parede do tanque

Escala 1:25 · do interior (espelhada em relação à planta)

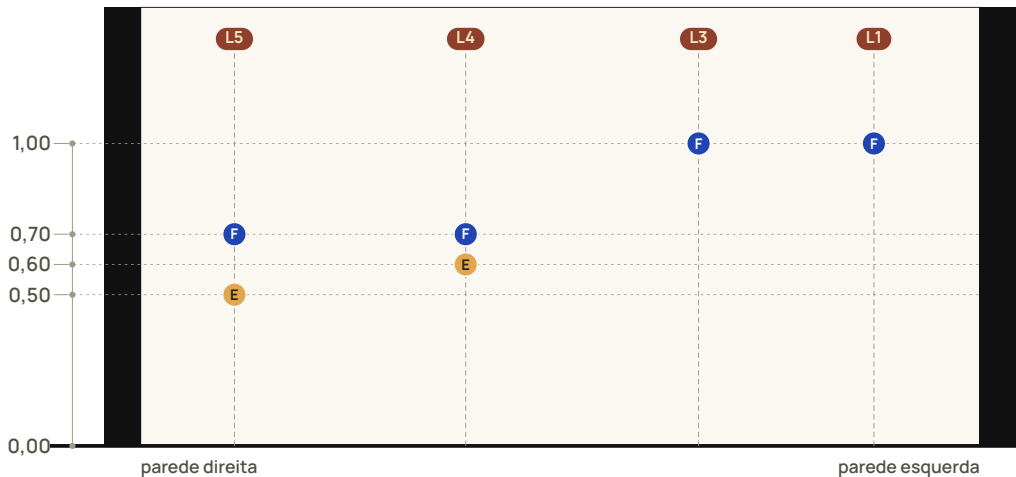

02 Ampliações · cozinha · gourmet · lavanderia

Escala 1:25 · plotagem em A2 · cotas em metros a partir da face da parede indicada



Pontos e alturas

QUADRO 1

CÓD. PEÇA · EIXO ALTURAS (m) · FONTE

COZINHA

- C1 Filtro**  
1,01 da parede inferior  
P 1,00<sup>C</sup>
- C2 Cuba da pia · misturador monocomando**  
2,16 da parede inferior  
P 0,50<sup>D</sup> Q 0,50<sup>C</sup> E 0,35<sup>C</sup>
- C3 Geladeira**  
3,60 da parede da janela (esquerda)  
P 1,25<sup>C</sup>
- C4 Lava-louças · face da mureta**  
1,90 da parede da janela · na face norte da mureta do balcão (≈0,32 da ponta)  
P 0,60<sup>C</sup> E 0,50<sup>P</sup>

ÁREA GOURMET

- G1 Cuba · misturador de mesa**  
1,75 da parede inferior (2,80 até a superior, conforme caderno)  
P 0,50<sup>D</sup> Q 0,50<sup>C</sup> E 0,50<sup>P</sup>

A. S. · ÁREA DE SERVIÇO

- L1 Torneira de parede · tanque**  
0,35 da parede esquerda  
P 1,00<sup>P</sup>
- L3 Torneira de parede · tanque**  
0,93 da parede esquerda  
P 1,00<sup>P</sup>
- L4 Máquina de lavar roupas**  
1,70 da parede esquerda  
P 0,70<sup>C</sup> E 0,60<sup>P</sup>
- L5 Tanquinho**  
0,31 da parede direita  
P 0,70<sup>C</sup> E 0,50<sup>P</sup>

Revisões sobre o caderno

QUADRO 1A

| PEÇA        | CADERNO               | PLANTA 29/09            |
|-------------|-----------------------|-------------------------|
| COZINHA     |                       |                         |
| Filtro      | 1,00                  | 1,01                    |
| Cuba        | 2,15                  | 2,16                    |
| Lava-louças | 0,40 da borda da ilha | 1,90 · 2,30 das paredes |

A. S.

|                   |             |             |
|-------------------|-------------|-------------|
| Torneira · tanque | 0,40        | 0,35        |
| Torneira · tanque | 1,00        | 0,93        |
| Máquina de lavar  | 1,80        | 1,70        |
| Tanquinho         | 2,55 (esq.) | 0,31 (dir.) |

Eixos em metros. Vale a Planta Pontos Hidráulicos (decisão do cliente, 30/09/2026).

Legenda

QUADRO 2

- F Água fria  
Q Água quente  
E Esgoto  
R Registro geral  
S Saída de chuveiro (misturada)
- R Ponto com eixo sem cota  
B1.3 Código do ponto  
4 Ampliação (Quadro 1)  
1,00 Cota em metros  
Alvenaria  
Janela / vidro

Letra no círculo = serviço. Altura do piso acabado ao eixo do ponto.

Observações técnicas

QUADRO 3

1. Cozinha

Filtro e cuba na parede da janela. Geladeira a 3,60 da parede da janela, na parede superior. Lava-louças: água e esgoto saem pela face norte da mureta do balcão (1,83 × 0,11 m), a 1,90 da parede da janela (R02).

2. Lava-louças

Tomada da face do balcão afastada no mínimo 0,30 m dos pontos de água e esgoto (Tomadas R05, item 13.5).

3. Área Gourmet

Cuba a 1,75 da parede inferior; fecha com os 2,80 até a parede superior do caderno. Misturador Deca Flex Plus (AF/AQ).

4. A.S.

Posições conforme a planta de 29/09. Tanque único l.Corso: L1 e L3 ficam por ora; uma será vedada depois. Ponto L2 (0,64) eliminado na R03. Tanquinho cotado pela parede direita.

5. Alturas

Do piso acabado ao eixo. A letra ao lado de cada altura indica a fonte (Quadro 1B da prancha 01).

6. Escopo

Localização de pontos. Diâmetros, trajetos e declividades: projeto hidrossanitário.



CARIMBO

PROJETO  
**Residência Ivan e Ana Neris**  
Nova Odessa – SP

RESPONSÁVEIS TÉCNICAS  
Lidiane Barbosa · CAU A290220-6  
Isadora Ferrari · CAU A263982-8

PLANTA  
Pontos hidráulicos · ampliações

ESCALA  
1:25 · folha A2

DATA  
02/10/2026

PRANCHA  
02/04


REVISÃO  
R03

0 – 2 m

Conferir as medidas no local


6 Banho Suíte Master

Escala 1:25 · pontos BM.1 a BM.5

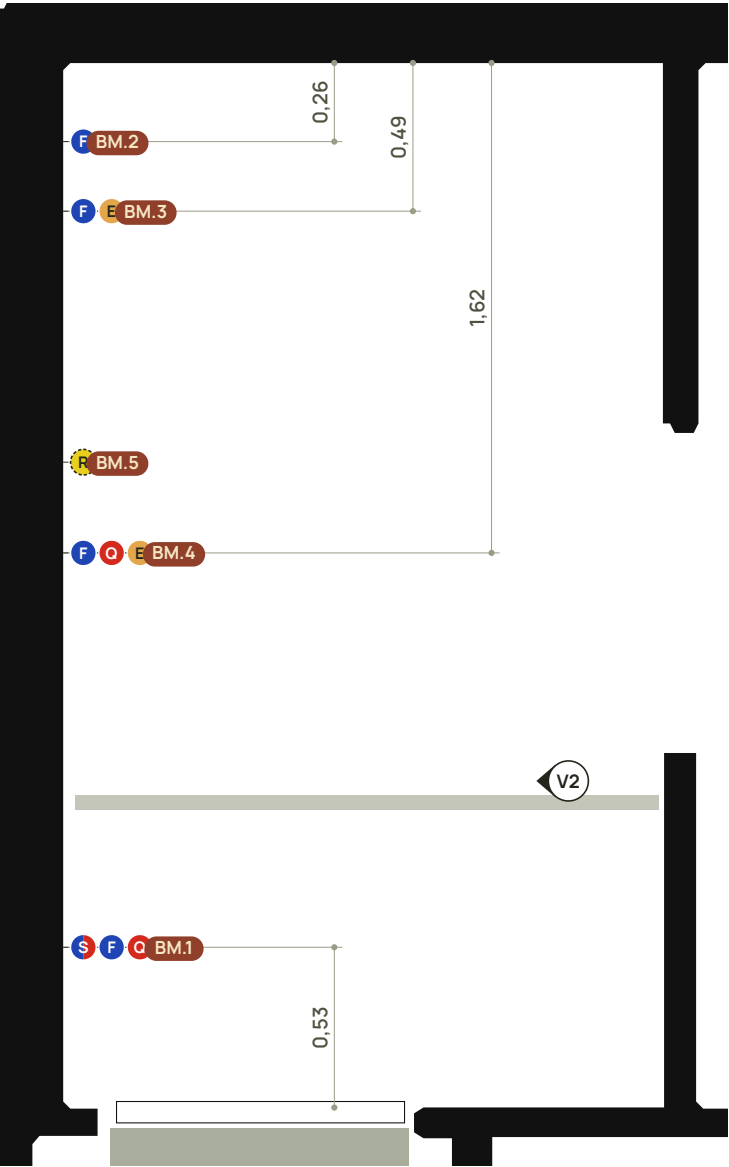


4 Banhos Suíte 1 e Suíte 2

Escala 1:25 · pontos B1.1 a B1.5 e B2.1 a B2.5 (espelhado)

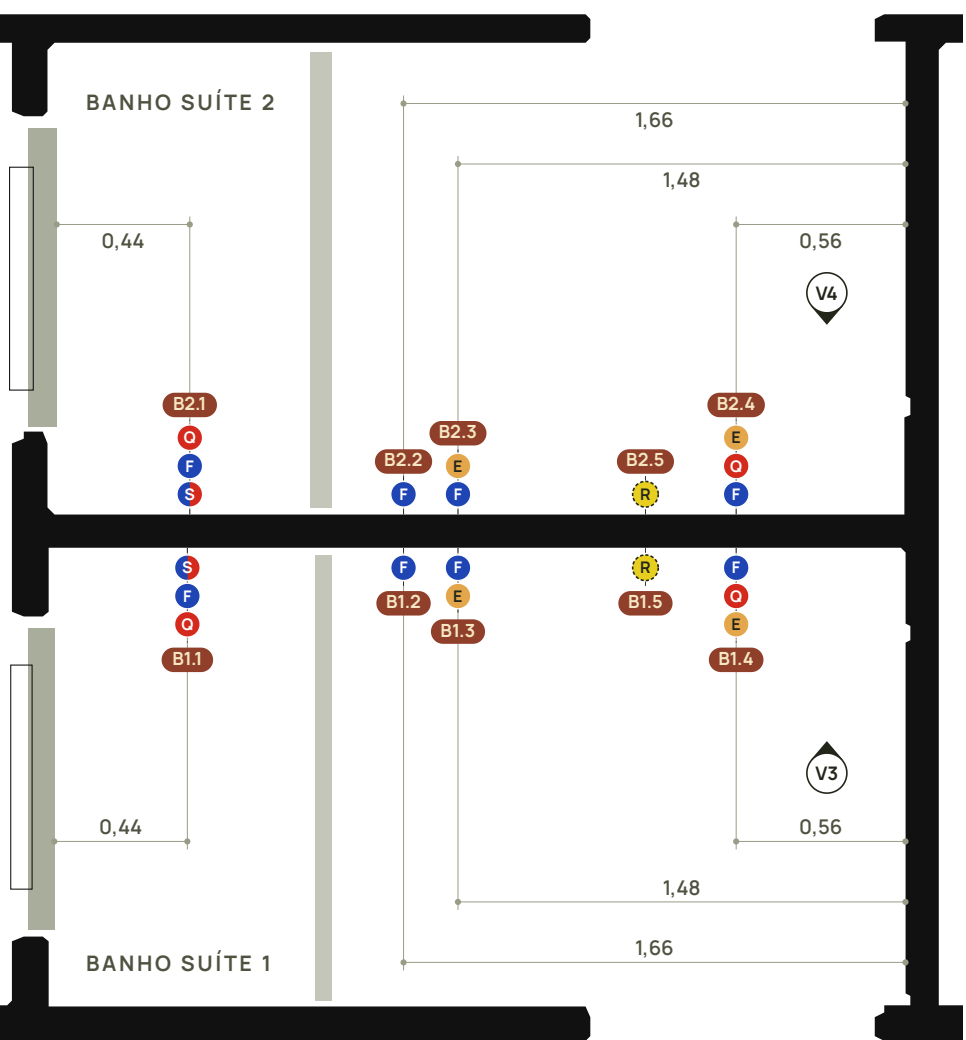


7 Banho 4

Escala 1:25 · pontos B4.1 a B4.5

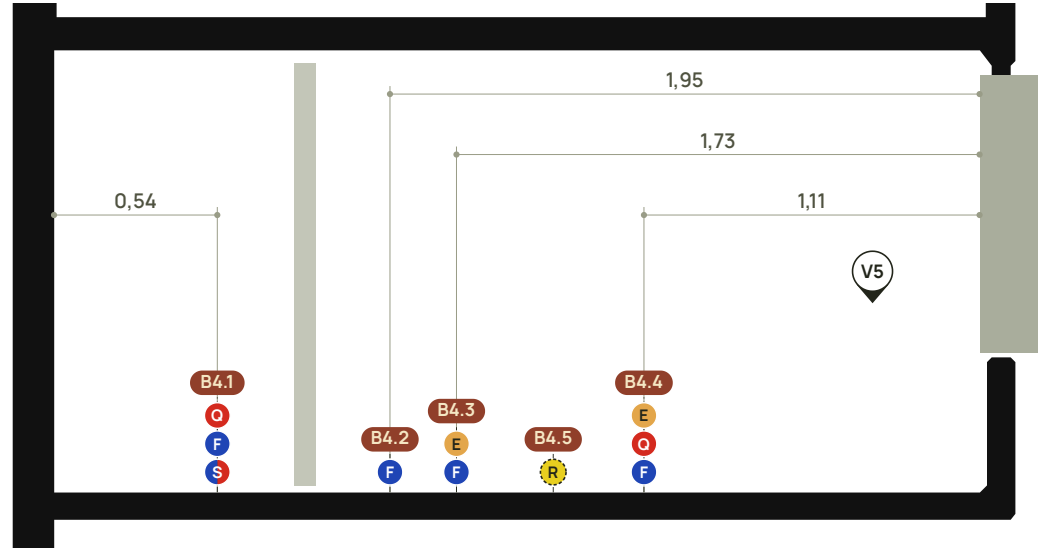

V2 Banho Suíte Master

Escala 1:50 · do interior · alturas do piso acabado

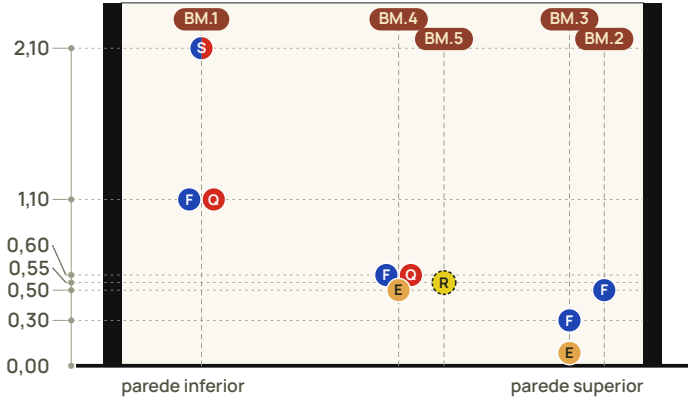


V3 Banho Suíte 1

Escala 1:50 · do interior · alturas do piso acabado




V4 Banho Suíte 2

Escala 1:50 · do interior · alturas do piso acabado

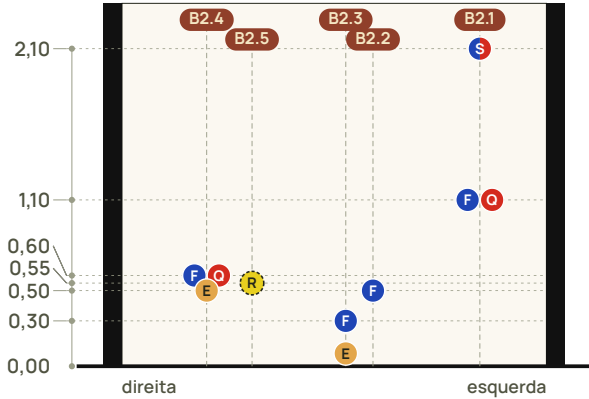

V5 Banho 4

Escala 1:50 · do interior · alturas do piso acabado

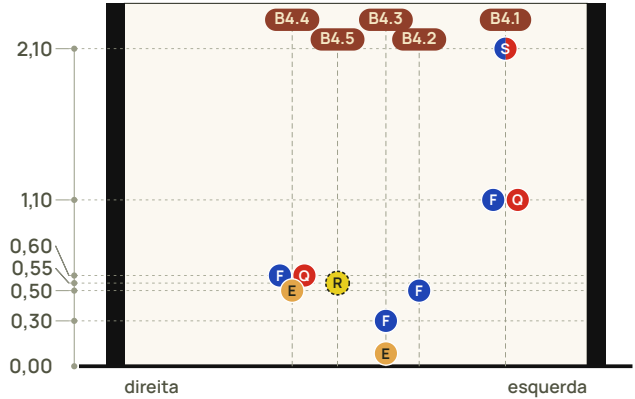

03 Ampliações · banheiros

Plantas 1:25 · vistas 1:50 · plotagem em A2 · cotas em metros a partir da face da parede indicada



Pontos e alturas

QUADRO 1

CÓD. PEÇA · EIXO ALTURAS (m) · FONTE

BANHO SUÍTE 1

- B1.1 Chuveiro  
0,44 da parede esquerda  
S 2,10 C F 1,10 C O 1,10 C
- B1.2 Ducha higiênica  
1,66 da parede direita  
P 0,50 P
- B1.3 Bacia sanitária  
1,48 da parede direita  
P 0,30 P E piso C
- B1.4 Cuba · misturador de mesa  
0,56 da parede direita  
P 0,60 C O 0,60 D E 0,50 P
- B1.5 Registro geral  
sem cota · dentro do armário  
R 0,55 P

BANHO SUÍTE 2 (ESPELHADO)

- B2.1 Chuveiro  
0,44 da parede esquerda  
S 2,10 C F 1,10 C O 1,10 C
- B2.2 Ducha higiênica  
1,66 da parede direita  
P 0,50 P
- B2.3 Bacia sanitária  
1,48 da parede direita  
P 0,30 P E piso C
- B2.4 Cuba · misturador de mesa  
0,56 da parede direita  
P 0,60 C O 0,60 D E 0,50 P
- B2.5 Registro geral  
sem cota · dentro do armário  
R 0,55 P

BANHO SUÍTE MASTER

- BM.1 Chuveiro  
0,53 da parede inferior  
S 2,10 C F 1,10 C O 1,10 C
- BM.2 Ducha higiênica  
0,26 da parede superior  
P 0,50 P
- BM.3 Bacia sanitária  
0,49 da parede superior  
P 0,30 P E piso C
- BM.4 Cuba · misturador de mesa  
1,62 da parede superior  
P 0,60 C O 0,60 D E 0,50 P
- BM.5 Registro geral  
sem cota · dentro do armário  
R 0,55 P

BANHO 4

- B4.1 Chuveiro  
0,54 da parede esquerda  
S 2,10 C P 1,10 C O 1,10 C
- B4.2 Ducha higiênica  
1,95 da parede direita  
P 0,50 P
- B4.3 Bacia sanitária  
1,73 da parede direita  
P 0,30 P E piso C
- B4.4 Cuba de sobrepor · misturador bica alta  
1,11 da parede direita  
P 0,60 D O 0,60 D E 0,50 P
- B4.5 Registro geral  
sem cota · dentro do armário  
R 0,55 C

Legenda

QUADRO 2

- F Água fria  
O Água quente  
E Esgoto  
R Registro geral  
S Saída de chuveiro (misturada)
- R Ponto com eixo sem cota  
B1.3 Código do ponto  
4 Ampliação (Quadro 1)  
1,00 Cota em metros  
Alvenaria  
Janela / vidro

Letra no círculo = serviço. Altura do piso acabado ao eixo do ponto.

Observações técnicas

QUADRO 3

1. Chuveiro

Kit Acqua Plus: saída a 2,10; misturador de duas alavancas (AF/AQ) a 1,10, já executado: afastamento a medir em obra.

2. Bacia

Roca ONA com caixa acoplada: alimentação a 0,30 (conferir na ficha da Roca) e esgoto no piso. Sem válvula de descarga.

3. Registro geral

A 0,55, dentro do armário da bancada. Eixo sem cota (marcador tracejado): definir com a marcenaria.

4. Referências

Banhos Suíte 1, Suíte 2 e Banho 4: chuveiro pela parede esquerda, demais peças pela direita. Banho Suite Master: peças pela parede superior, chuveiro pela inferior. Vistas esquemáticas: eixos e alturas, sem louças.

Revisões sobre o caderno

QUADRO 3 A

| PEÇA                      | CADERNO     | PLANTA      |
|---------------------------|-------------|-------------|
| <b>Banhos Suíte 1 e 2</b> |             |             |
| Ducha higiênica           | 1,20 (esq.) | 1,66 (dir.) |
| Bacia                     | 1,40 (esq.) | 1,48 (dir.) |
| Cuba                      | 2,35 (esq.) | 0,56 (dir.) |
| Chuveiro                  | 0,45        | 0,44        |
| <b>Banho Suíte Master</b> |             |             |
| Ducha higiênica           | 0,25        | 0,26        |
| Bacia                     | 0,45        | 0,49        |
| Cuba                      | 1,60        | 1,62        |
| Chuveiro (da inferior)    | 0,55        | 0,53        |
| <b>Banho 4</b>            |             |             |
| Chuveiro                  | 0,55        | 0,54        |
| Bacia (da dir.)           | 1,75        | 1,73        |
| Torneira (da dir.)        | 1,15        | 1,11        |

Vale a planta de 29/09. Nos Banhos Suíte 1/2 a soma das cotas do caderno (2,90) excedia a largura do ambiente.



CARIMBO

PROJETO  
**Residência Ivan e Ana Neris**  
Nova Odessa - SP

RESPONSÁVEIS TÉCNICAS  
Lidiane Barbosa · CAU A290220-6  
Isadora Ferrari · CAU A263982-8

PLANTA  
Pontos hidráulicos · banheiros

ESCALA  
1:25 e 1:50 · folha A2

DATA  
02/10/2026

PRANCHA  
03/04

REVISÃO  
R03

0 — 2 m (1:25)

Conferir as medidas no local

