


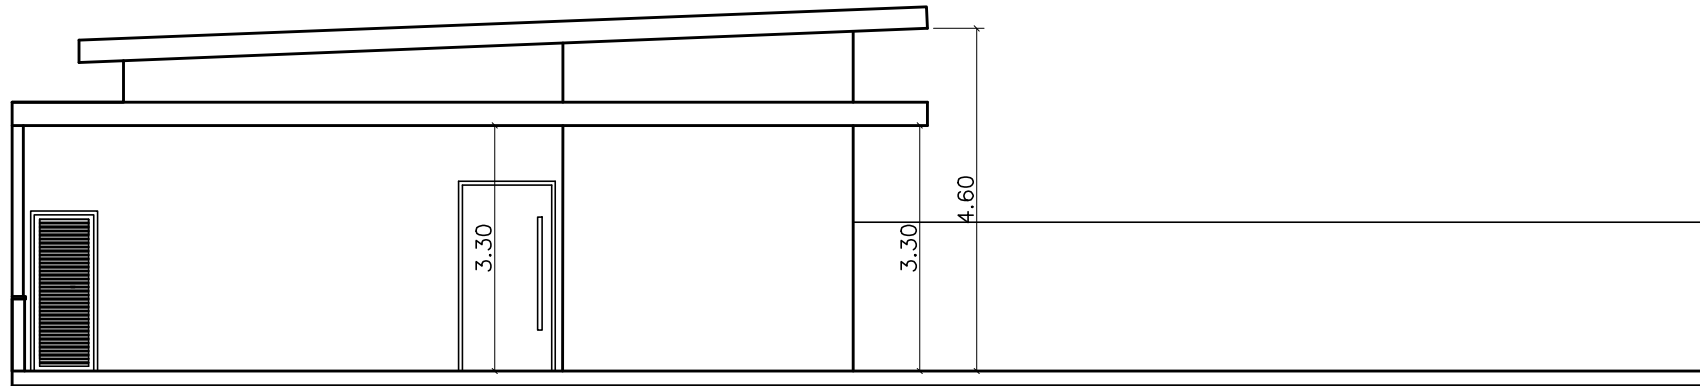


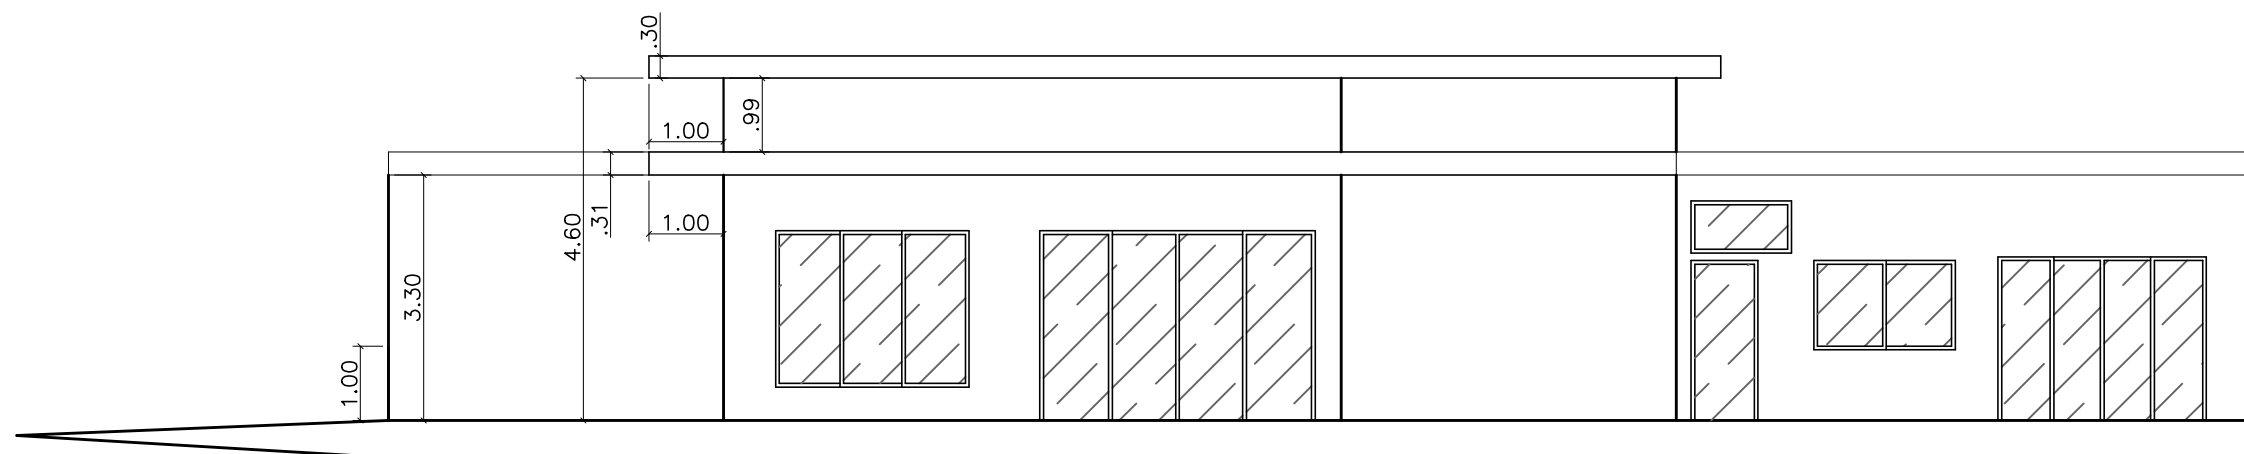


FACHADA RUA APARECIDA DE FREITAS PINTO
ESCALA 1:100

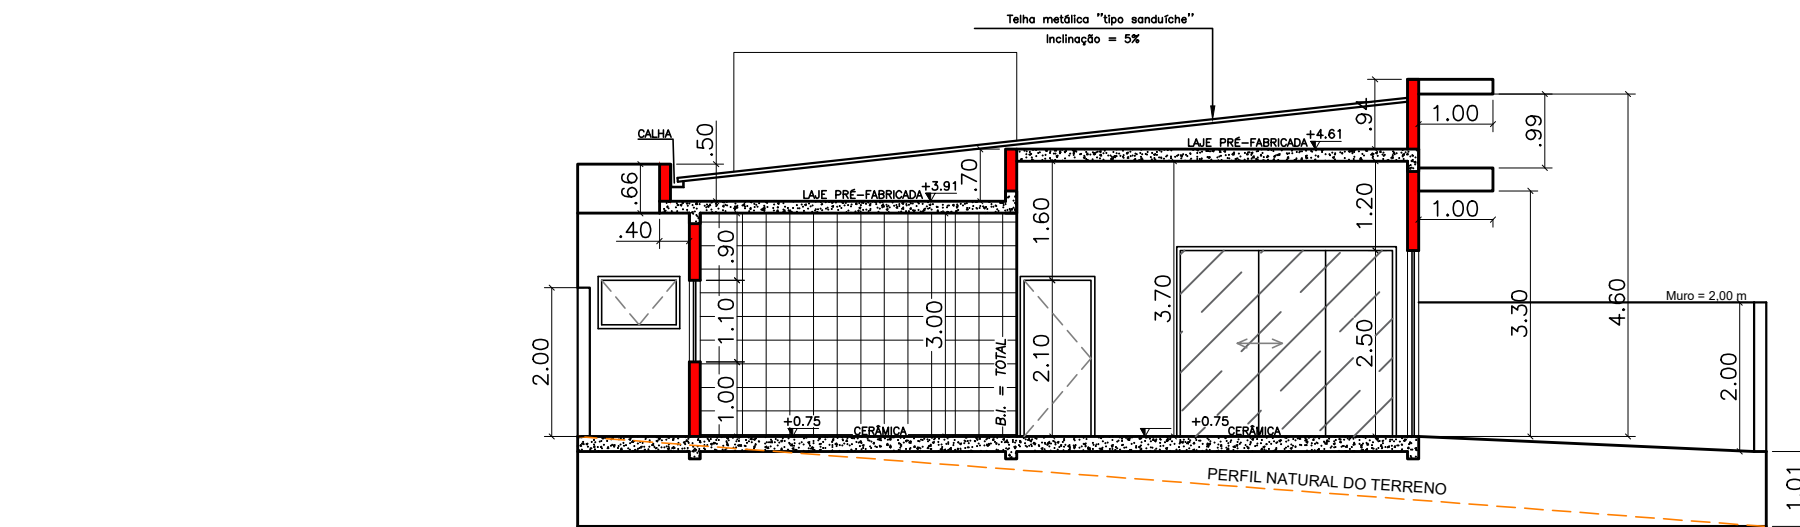

FACHADA AV. 03 - TR. 02
ESCALA 1:100

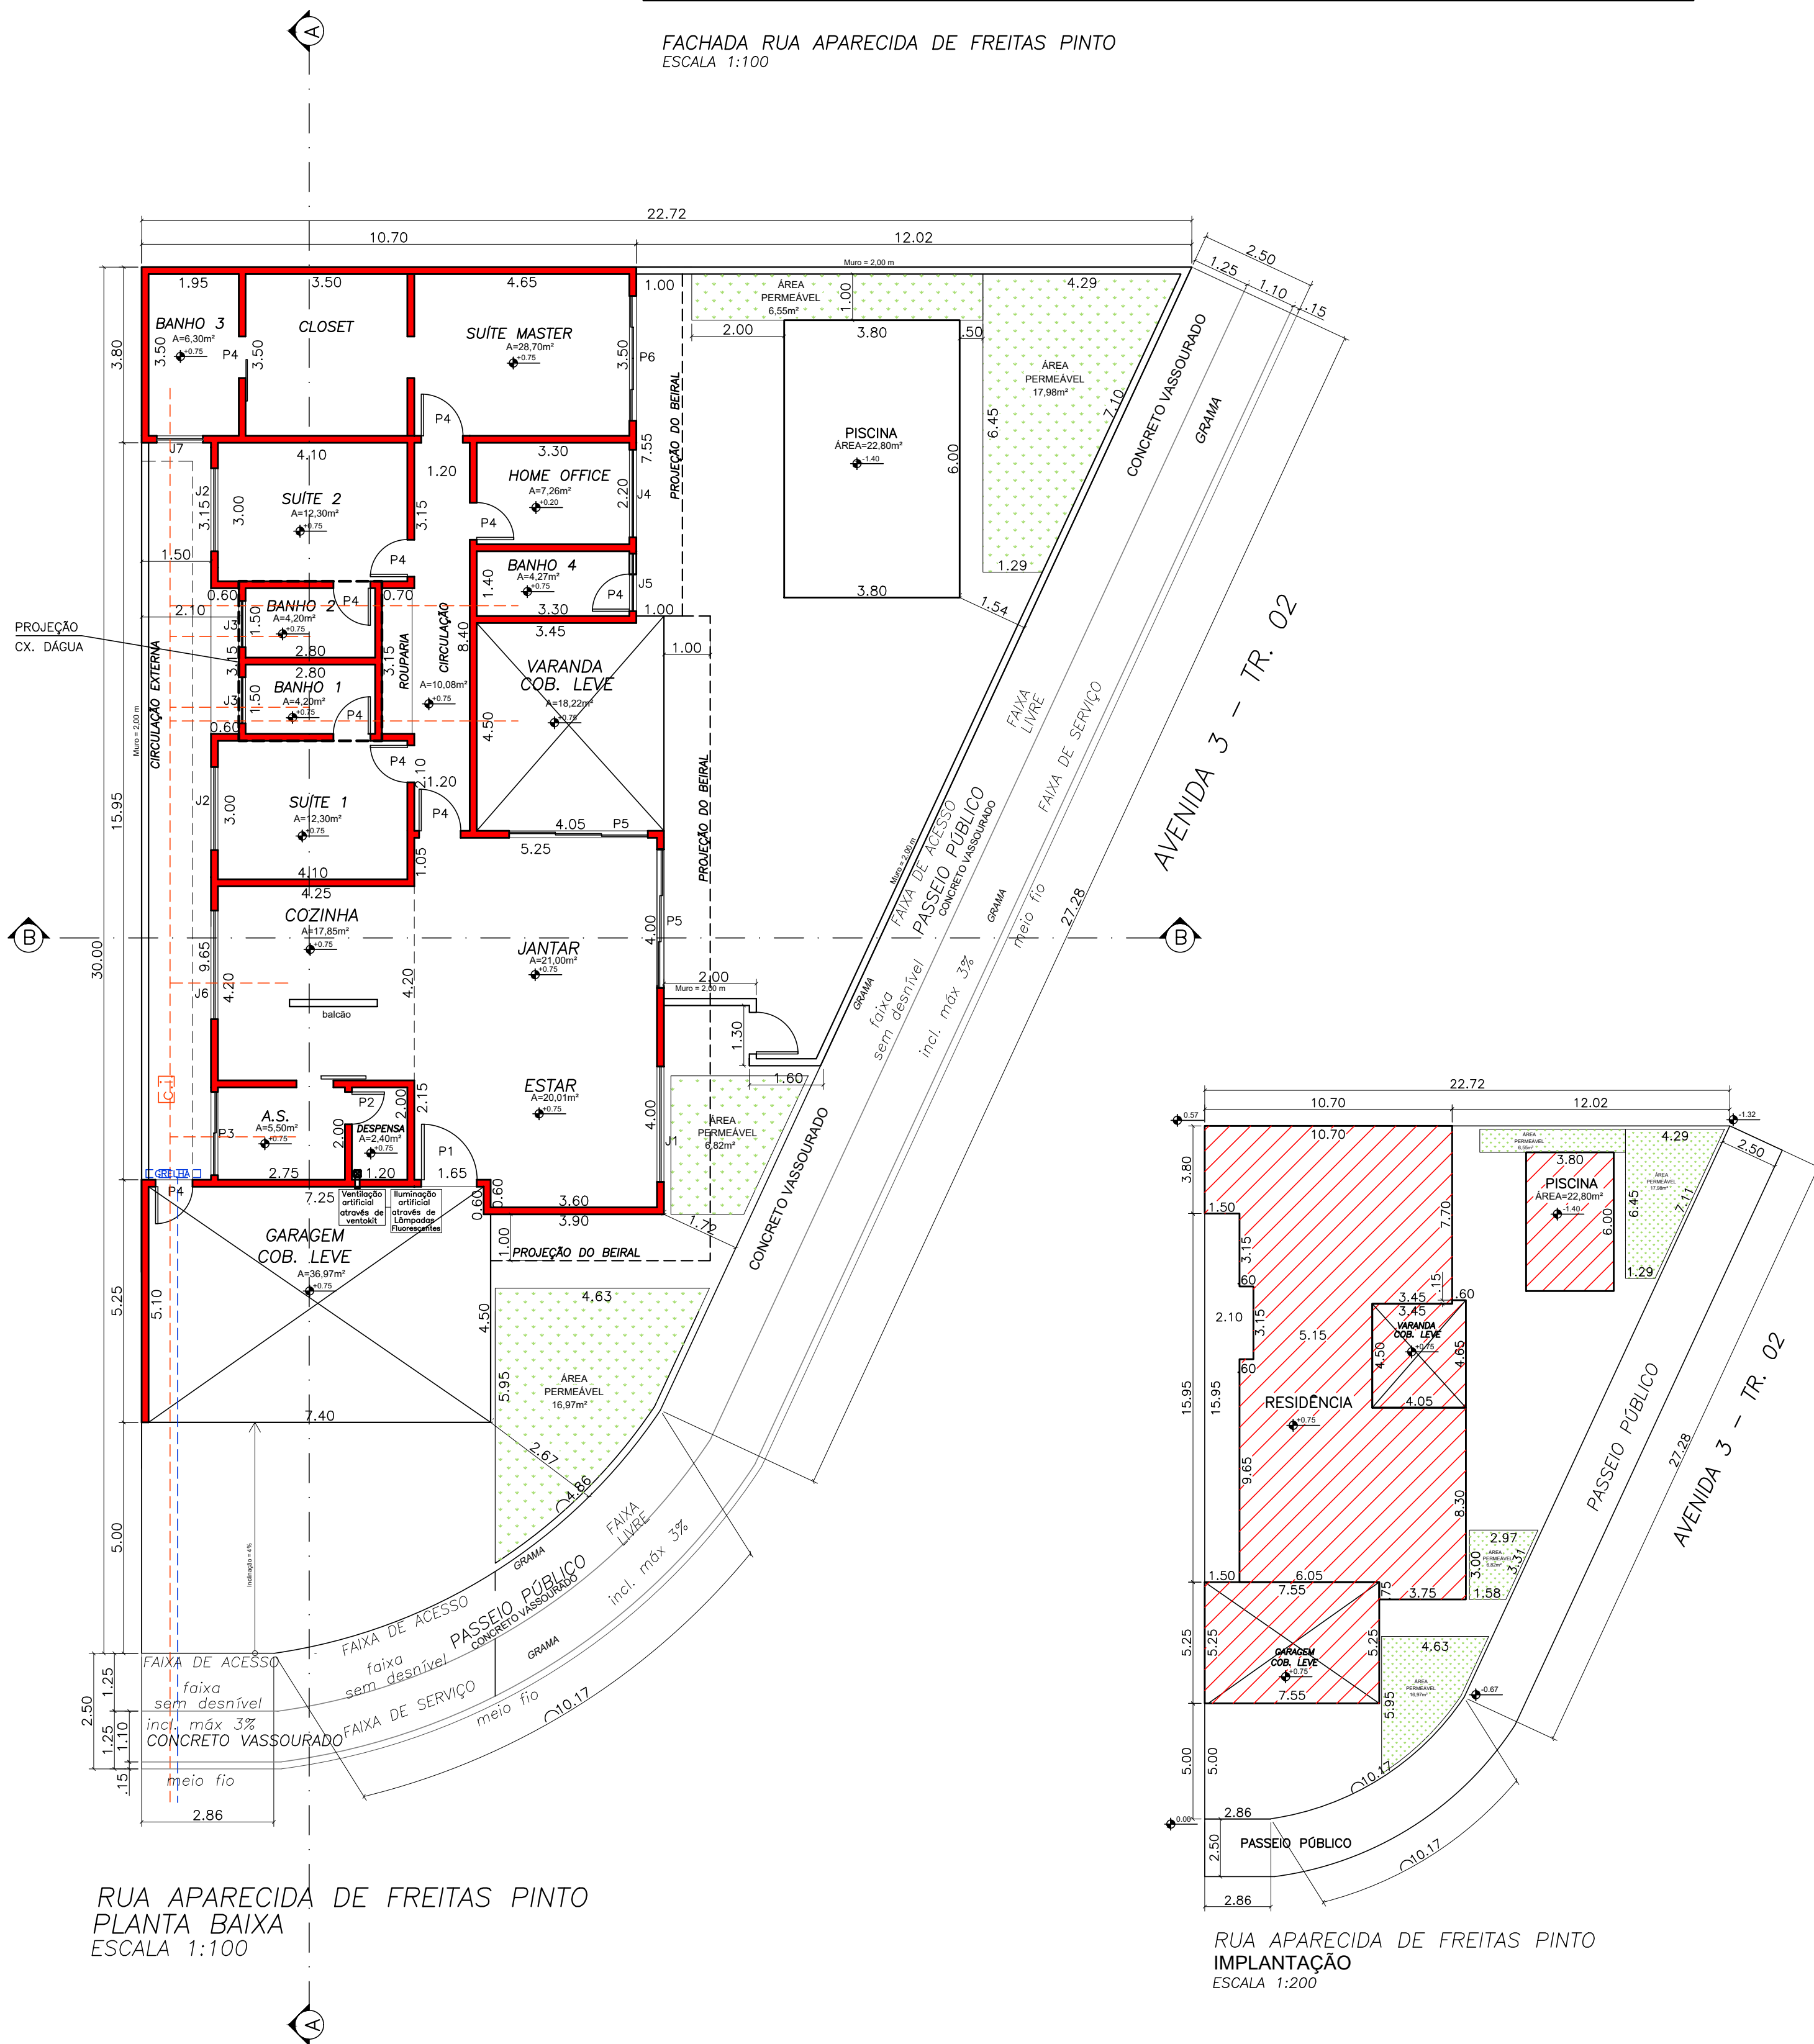

CORTE BB
ESCALA 1:100

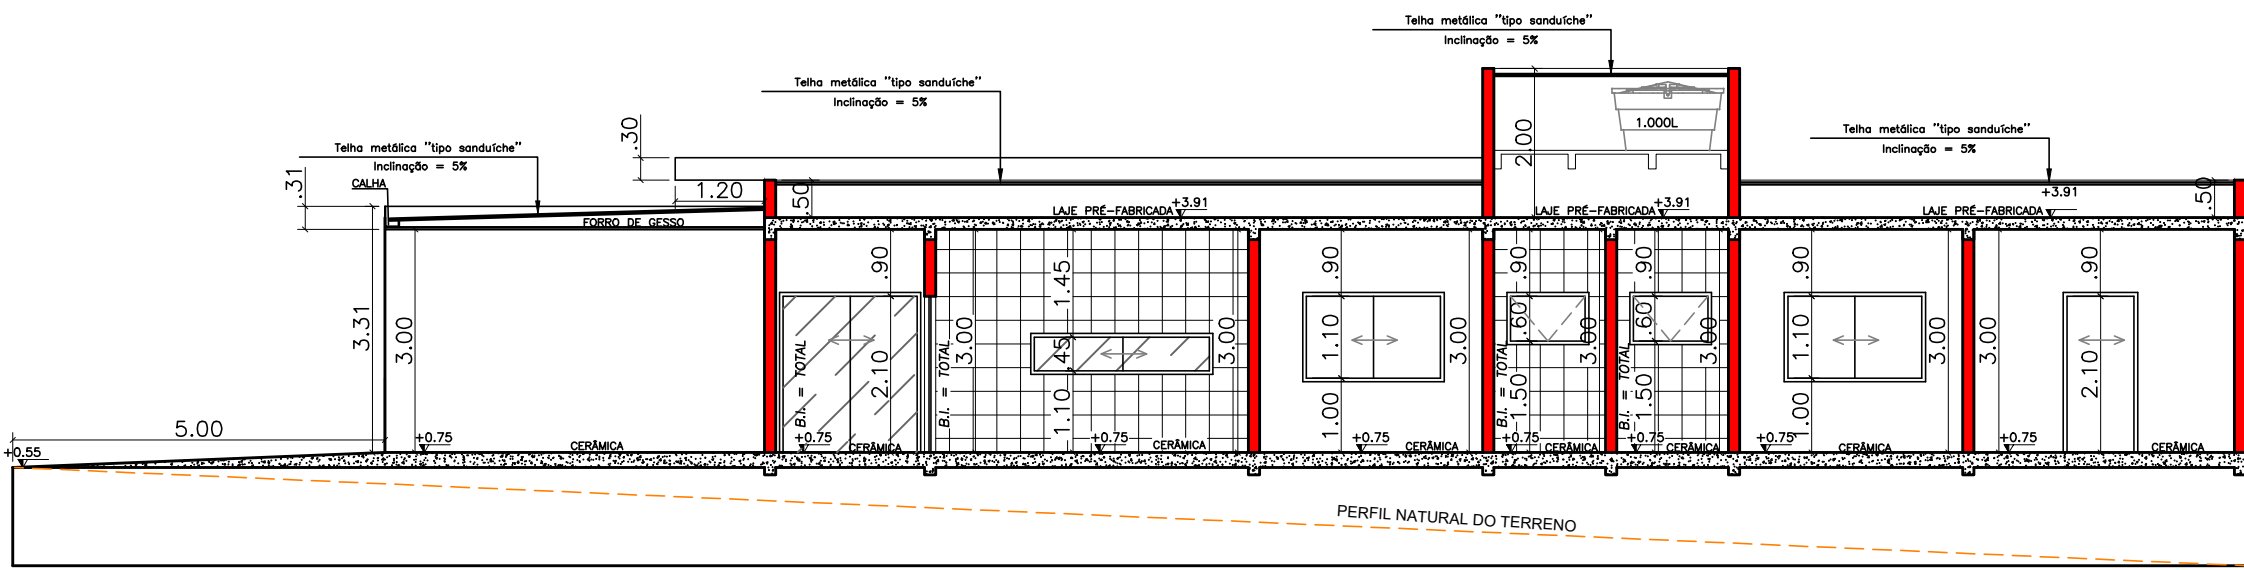

CORTE AA
ESCALA 1:100

LEGENDA	
	A CONSTRUIR
	A CONSTRUIR COB. LEVE
	ESGOTO
	ÁGUAS PLUVIAIS
	ÁREA PERMEÁVEL

NÃO SERÁ PERMITIDO DRENAGEM
PLUVIAL PELA RÊDE DE ESGOTO.
CONFORME ART. 28 DA LEI 553

TABELA DE PORTAS	
P1=	1.20 X 2.50
P2=	0.70 X 2.10
P3=	1.80 X 2.10
P4=	0.80 X 2.10
P5=	2.85 X 2.50
P6=	2.70 X 2.10

TABELA DE JANELAS	
J1=	2.50 x 2.00 x 0.50
J2=	1.80 x 1.10 x 1.00
J3=	1.00 x 0.60 x 1.50
J4=	1.90 x 1.10 x 1.00
J5=	1.25 x 0.50 x 2.20
J6=	2.35 x 0.45 x 1.10
J7=	1.00 x 0.80 x 1.20

PROJETO COMPLETO		F.U.
OBRA- CONSTRUÇÃO RESIDENCIAL		
LOCAL- RUA APARECIDA DE FREITAS PINTO, ESQ. AV. TRÊS (3) - TR 02 - LOTE: 10 - QUADRA: 23		
LOTEAMENTO PARQUE VILA AMERICA - NOVA ODESSA-SP		
PROPRIETÁRIO - IVAN FERNANDES NERIS		
ZONA- ZER-15	CATEGORIA DE USO: HU	
ESCALAS- 1:100 1:200	CADASTRO- 01626.0230.00	
SITUAÇÃO SEM ESCALA		DECLARAÇÃO:
		Declaro que a aprovação do projeto não implica no reconhecimento por parte da Prefeitura do direito de propriedade do terreno.
RUA APARECIDA DE FREITAS PINTO		PROP.: IVAN FERNANDES NERIS
		CPF.: 275.016.428-18
		RG.: 33.289.925-1 SSP-SP
ÁREAS		
TERRENO	M2	%
A CONSTRUIR ALVENARIA	463,87	100,00
A CONSTRUIR COB. LEVE GAR / VAR	177,33	
A CONSTRUIR PISCINA	57,95	
TOTAL A CONSTRUIR	22,80	
Ocupação	258,08	55,64
ÁREA PERMEÁVEL	258,08	
COEFICIENTE DE APROVEITAMENTO	48,32	10,42
0,55		
AUTOR DO PROJETO E RESP. PELA ORIENTAÇÃO TÉCNICA		
HAMILTON VIANNA		
ENGENHEIRO CIVIL		
CREA.: 5069507279-SP		
ART.: 2620251953875		
RUA SÃO JORGE, 799 - JARDIM SÃO CAMILO - S.B.D'OESTE (SP)		
CEP: 13.455-806 - FONE: 19 - 98309-6228		
EMAIL: hamilton_vianno@hotmail.com		
ANOTAÇÕES E APROVAÇÕES		
SECRETARIA DE OBRAS, PROJETOS E PLANEJAMENTO URBANO		
DIRETORIA DE OBRAS E PROJETOS		
PREFEITURA MUNICIPAL DE NOVA ODESSA		
ESTADO DE SÃO PAULO		
PARA RECEBER "HABITE-SE" DEVERÁ:		
POSSUIR RESERVATÓRIO DE ÁGUA COM CAPACIDADE MÍNIMA DE 1000 LITROS		
POSSUIR CAIXA RECEPTORA DE CORREIO CONFORME A LEI 1509/96		
APRESENTAR DOF (DOCUMENTO DE ORIGEM FLORESTAL), CONFORME A LEI 2441/10		
PROTÓCOLO Nº		
APROVADA EM		
INSCRIÇÃO CADASTRAL		
SETOR	QUADRA	LOTE
SUB-LOTE	ANTERIOR	