


01 Planta de pontos hidráulicos

Escala 1:100 · plotagem em A2 · posições conforme Planta Pontos Hidráulicos (29/09/2026)

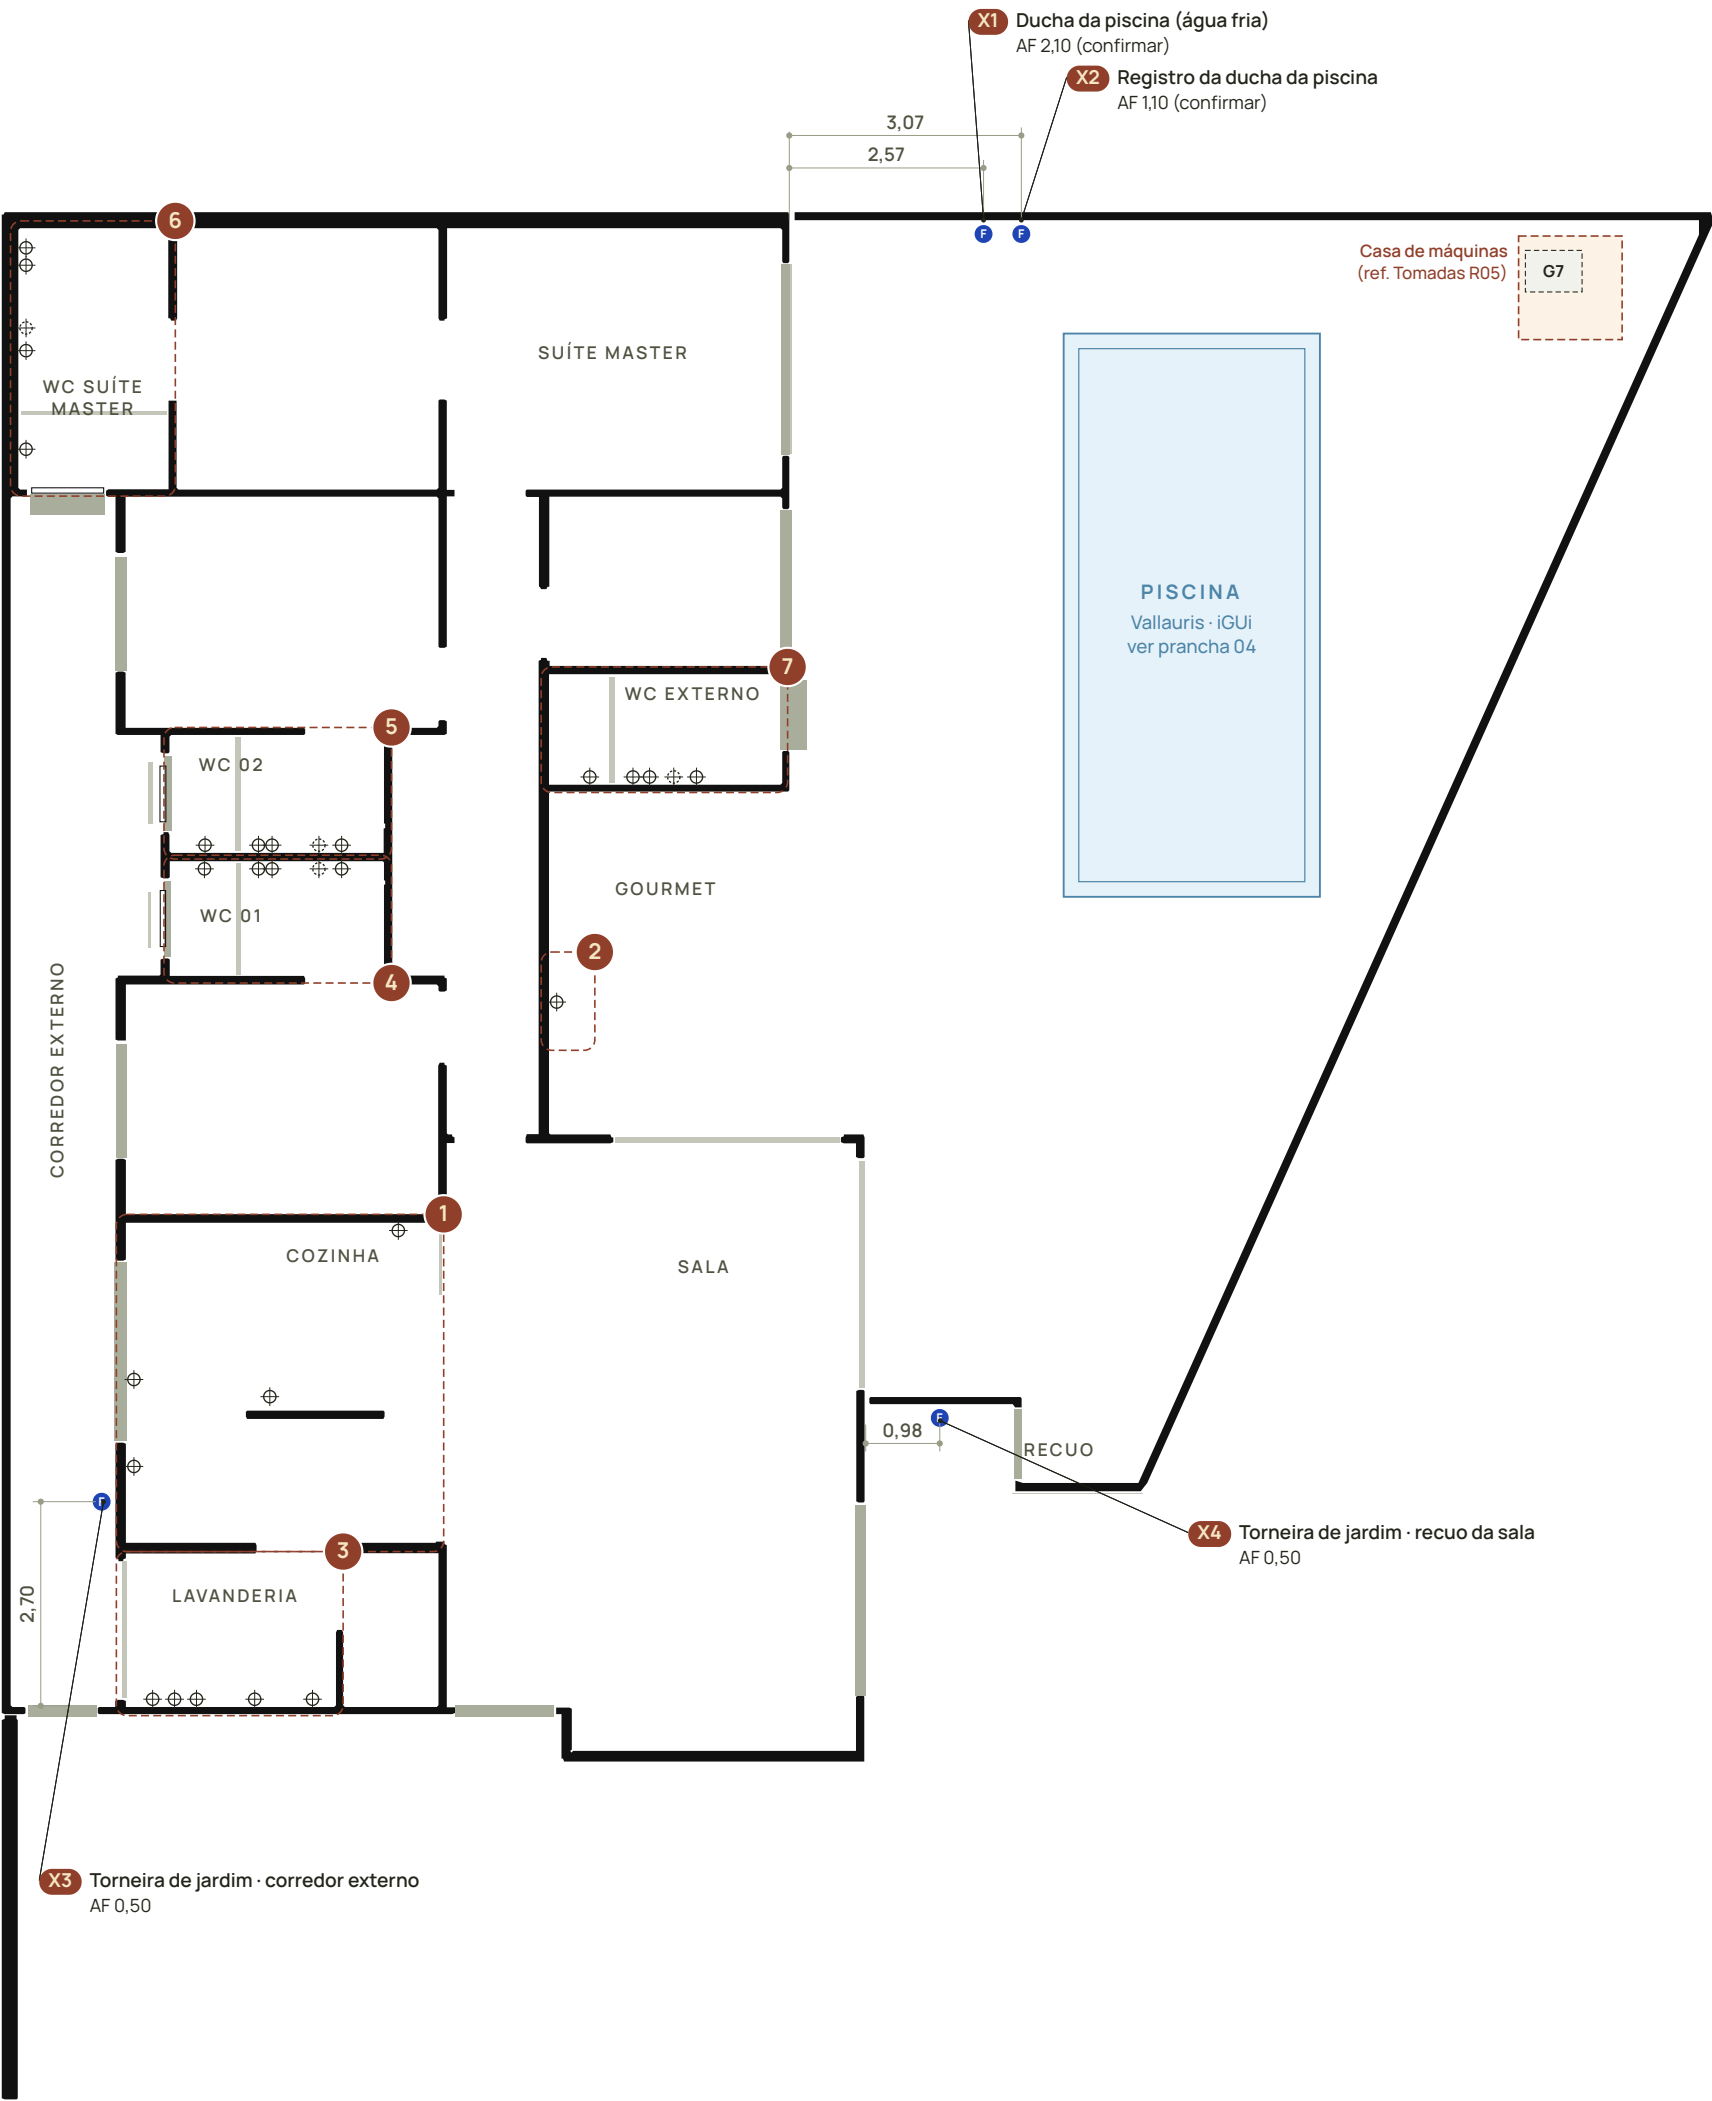

Pontos por ambiente

QUADRO 1

Nº	AMBIENTE · PONTOS	PRANCHA
1	Cozinha C1 a C4 · filtro, cuba, geladeira e lava-louças (ilha)	02
2	Gourmet G1 · cuba · torneira de bancada	02
3	Lavanderia L1 a L5 · torneiras e bancada do tanque, máquina, tanquinho	02
4	WC 01 W1.1 a W1.5 · chuveiro, ducha higiênica, bacia, cuba, registro	03
5	WC 02 W2.1 a W2.5 · espelhado em relação ao WC 01	03
6	WC Suíte Master WS.1 a WS.5 · chuveiro, ducha higiênica, bacia, cuba, registro	03
7	WC Externo WE.1 a WE.5 · chuveiro, ducha higiênica, bacia, torneira, registro	03
8	Piscina Ducha e registro (X1, X2), skimmer, retorno, reposição, ladrão, dreno	04

Planta: selos em terracota indicam a ampliação de cada ambiente; o círculo com cruz marca o eixo de cada ponto. Pontos externos X1 a X4 cotados nesta prancha (Quadro 1A).

Pontos externos

QUADRO 1A

Nº	PONTO · POSIÇÃO	ALTURA
X1	Ducha da piscina (água fria) 2,57 da face externa da parede da Suíte Master · no muro.	2,10 m*
X2	Registro da ducha da piscina 3,07 da face externa da parede da Suíte Master · no muro.	1,10 m*
X3	Torneira de jardim · corredor externo 2,70 do alinhamento do portão · face externa da parede da cozinha.	0,50 m
X4	Torneira de jardim · recuo da sala 0,98 da face externa da parede da sala.	0,50 m

* Ducha de água fria junto à piscina: alturas adotadas do padrão do chuveiro (saída 2,10 · registro 1,10). Confirmar antes da execução.

Fontes das alturas

QUADRO 1B

- C Caderno Hidráulica Detalhe · Rev. 02 · 24/09/2026
- D Definição do cliente · 30/09/2026
- P Padrão do escritório (R02) · confirmado em 30/09/2026
- A Adotado do padrão do chuveiro · confirmar

Cada altura nos quadros das pranchas 02 a 04 traz a letra da sua fonte. Posições em planta: Planta Pontos Hidráulicos (29/09/2026), que prevalece sobre o caderno nas divergências (decisão de 30/09/2026).

Legenda

QUADRO 2

F	Água fria	⊕	Eixo de ponto (planta geral)
O	Água quente	R	Ponto com eixo sem cota
E	Esgoto	W1.3	Código do ponto
V	Válvula de descarga	4	Ampliação (Quadro 1)
R	Registro geral	1.00	Cota em metros
S	Saída de chuveiro (misturada)		Alvenaria
			Janela / vidro

Letra no círculo = serviço. Altura do piso acabado ao eixo do ponto.

Observações técnicas

QUADRO 3

- Escopo**
Prancha de localização de pontos. Não é projeto de dimensionamento: diâmetros, trajetos, declividades, ventilação, caixas e ramais seguem o projeto hidrossanitário do responsável técnico.
- Posições**
Cotas em metros, a partir da face da parede indicada em cada ponto. Os pontos dos ambientes estão cotados nas ampliações (pranchas 02 e 03); os externos, nesta prancha.
- Alturas**
Do piso acabado ao eixo do ponto. A fonte de cada valor está no Quadro 1B.
- Chuveiros**
Saída de chuveiro com registro misturador (água quente e fria). Sem chuveiro elétrico (Tomadas R05, item 12).
- Registro geral**
Dentro do armário da bancada de cada banheiro, a 0,55 m. Eixo sem cota: definir com a marcenaria.
- Compatibilização**
Pontos elétricos conforme a prancha de Tomadas R05. Manter no mínimo 0,30 m entre tomadas e pontos de água e esgoto. Conferir as medidas no local antes de fechar as paredes.
- Normas**
NBR 5626 (água fria e água quente), NBR 8160 (esgoto sanitário) e NBR 10339 (piscinas).



CARIMBO

PROJETO
Residência Ivan e Ana Neris
Nova Odessa - SP

RESPONSÁVEIS TÉCNICAS
Lidiane Barbosa · CAU A290220-6
Isadora Ferrari · CAU A269382-8

PLANTA
Pontos hidráulicos · geral

ESCALA
1:100 · folha A2

DATA
30/09/2026


PRANCHA
01/04

REVISÃO
R01


0 — 5 m

Conferir as medidas no local


1 Cozinha
Escala 1:25 · pontos C1 a C4

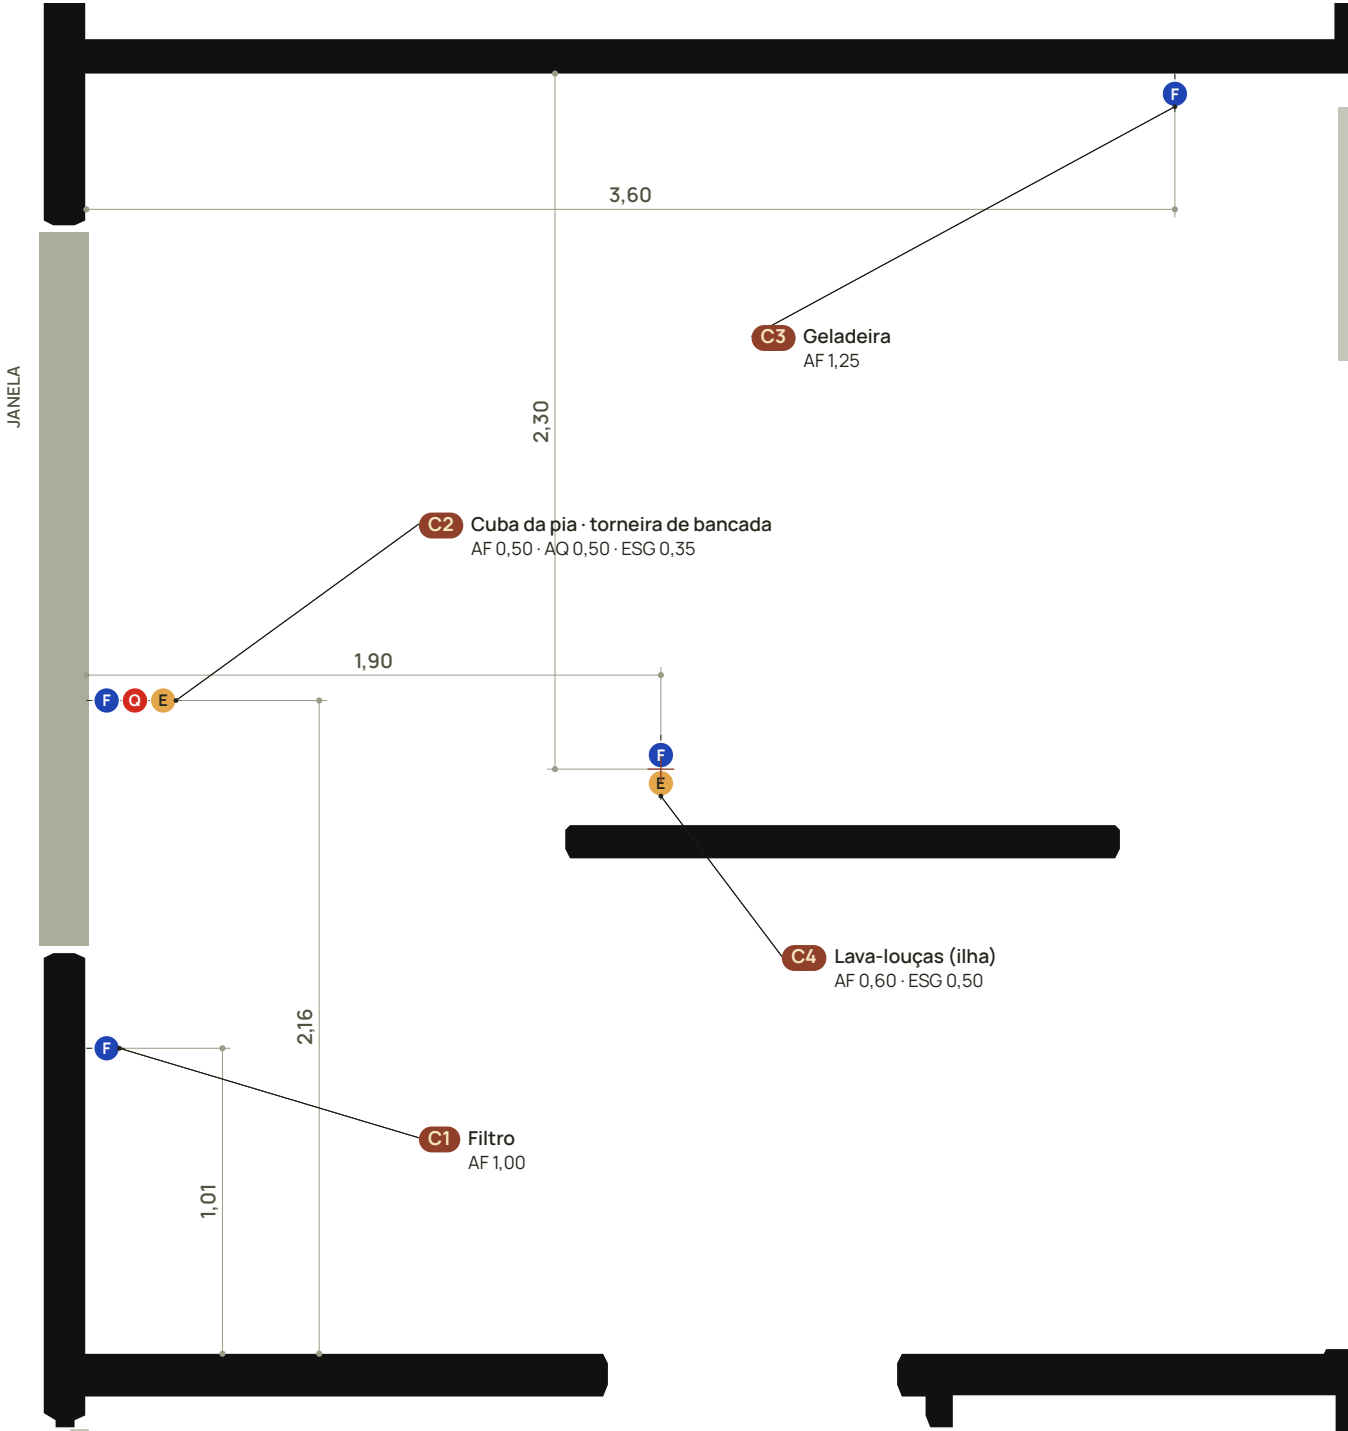


2 Gourmet
Escala 1:25 · ponto G1

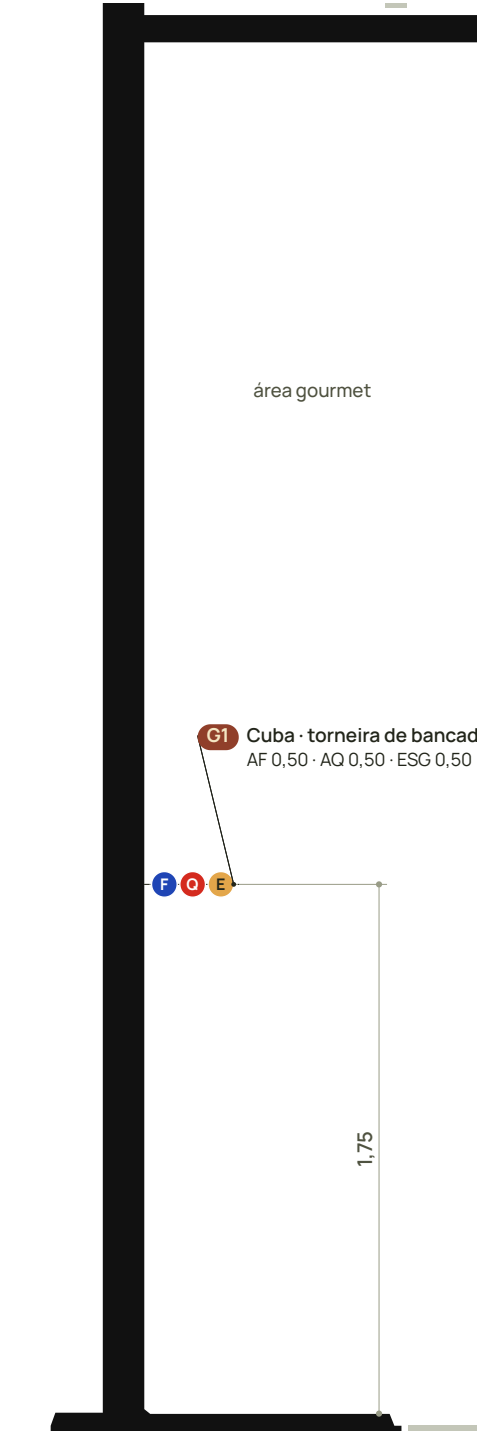

3 Lavanderia
Escala 1:25 · pontos L1 a L5

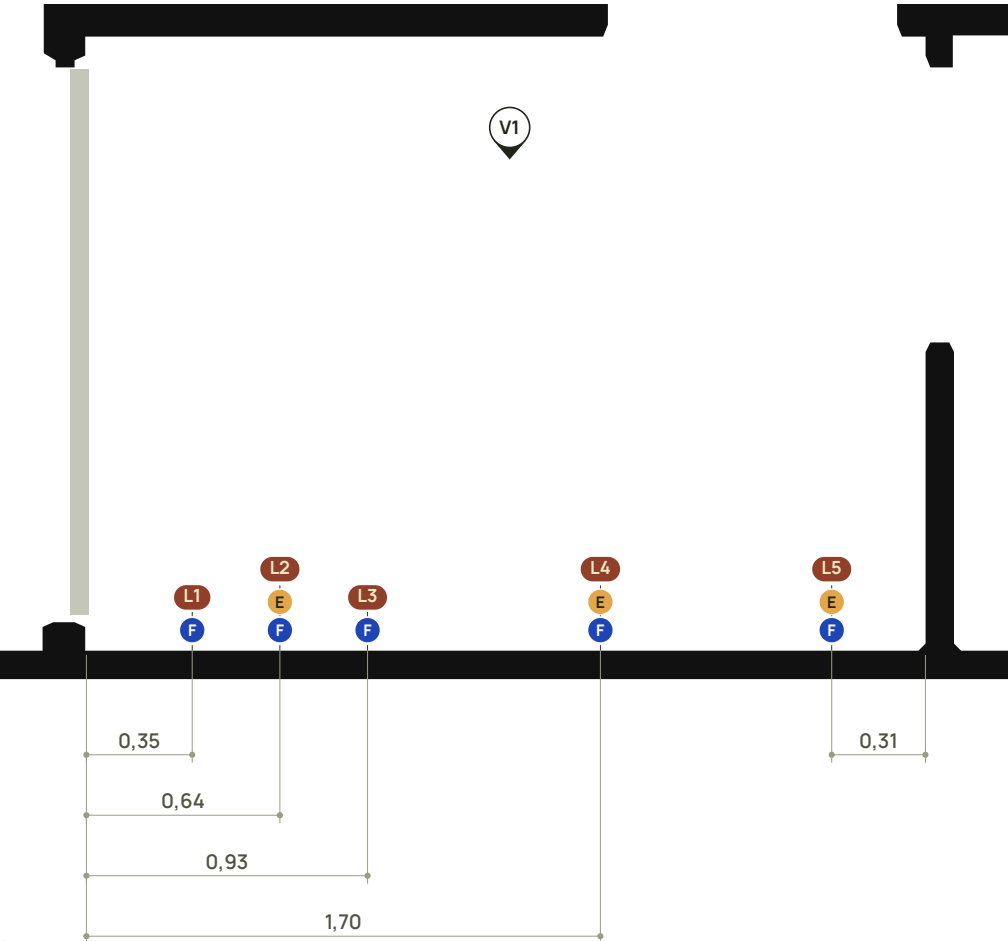

V1 Vista da parede do tanque
Escala 1:25 · do interior (espelhada em relação à planta)

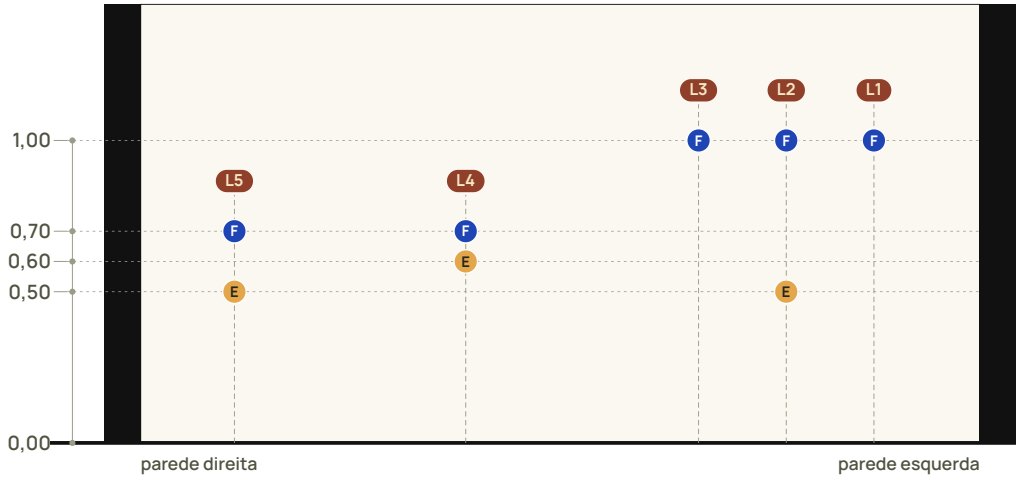

02 Ampliações · cozinha · gourmet · lavanderia
Escala 1:25 · plotagem em A2 · cotas em metros a partir da face da parede indicada



Pontos e alturas

QUADRO 1

CÓD. PEÇA · EIXO ALTURAS (m) · FONTE

COZINHA

- C1 Filtro
1,01 da parede inferior
P 1,00^C
- C2 Cuba da pia · torneira de bancada
2,16 da parede inferior
P 0,50^D Q 0,50^C E 0,35^C
- C3 Geladeira
3,60 da parede da janela (esquerda)
P 1,25^C
- C4 Lava-louças (ilha)
1,90 da parede da janela · 2,30 da parede superior
P 0,60^C E 0,50^P

GOURMET

- G1 Cuba · torneira de bancada
1,75 da parede inferior (2,80 até a superior, conforme caderno)
P 0,50^D Q 0,50^C E 0,50^P

LAVANDERIA

- L1 Torneira de parede · tanque
0,35 da parede esquerda
P 1,00^P
- L2 Ponto da bancada do tanque
0,64 da parede esquerda (meio das torneiras)
P 1,00^C E 0,50^P
- L3 Torneira de parede · tanque
0,93 da parede esquerda
P 1,00^P
- L4 Máquina de lavar roupas
1,70 da parede esquerda
P 0,70^C E 0,60^P
- L5 Tanquinho
0,31 da parede direita
P 0,70^C E 0,50^P

Revisões sobre o caderno

QUADRO 1A

PEÇA	CADERNO	PLANTA 29/09
COZINHA		
Filtro	1,00	1,01
Cuba	2,15	2,16
Lava-louças	0,40 da borda da ilha	1,90 · 2,30 das paredes

LAVANDERIA

Torneira · tanque	0,40	0,35
Torneira · tanque	1,00	0,93
Máquina de lavar	1,80	1,70
Tanquinho	2,55 (esq.)	0,31 (dir.)

Eixos em metros. Vale a Planta Pontos Hidráulicos (decisão do cliente, 30/09/2026).

Legenda

QUADRO 2

- F Água fria
Q Água quente
E Esgoto
V Válvula de descarga
R Registro geral
S Saída de chuveiro (misturada)
- Ponto com eixo sem cota
W1.3 Código do ponto
4 Ampliação (Quadro 1)
1,00 Cota em metros
Alvenaria
Janela / vidro

Letra no círculo = serviço. Altura do piso acabado ao eixo do ponto.

Observações técnicas

QUADRO 3

1. Cozinha
Filtro e cuba na parede da janela. Geladeira a 3,60 da parede da janela, na parede superior. Lava-louças na ilha: eixo cotado a partir das paredes (1,90 · 2,30); confere com os 0,40 da borda da ilha do caderno.
2. Lava-louças
Tomada da face do balcão afastada no mínimo 0,30 m dos pontos de água e esgoto (Tomadas R05, item 13.5).
3. Gourmet
Cuba a 1,75 da parede inferior; fecha com os 2,80 até a parede superior do caderno. Sem outros pontos de água.
4. Lavanderia
Posições conforme a planta de 29/09, que prevalece sobre o caderno. Tanquinho cotado pela parede direita. Ponto L2 (bancada do tanque) no meio das duas torneiras. Secadora elétrica: sem ponto.
5. Alturas
Do piso acabado ao eixo. A letra ao lado de cada altura indica a fonte (Quadro 1B da prancha 01).
6. Escopo
Localização de pontos. Diâmetros, trajetos e declividades: projeto hidrossanitário.



CARIMBO

PROJETO
Residência Ivan e Ana Neris
Nova Odessa – SP

RESPONSÁVEIS TÉCNICAS
Lidiane Barbosa · CAU A290220-6
Isadora Ferrari · CAU A269382-8

PLANTA
Pontos hidráulicos · ampliações
ESCALA
1:25 · folha A2

DATA
30/09/2026

PRANCHA
02/04


REVISÃO
R01

0 – 2 m

Conferir as medidas no local


6 WC Suíte Master

Escala 1:25 · pontos WS.1 a WS.5

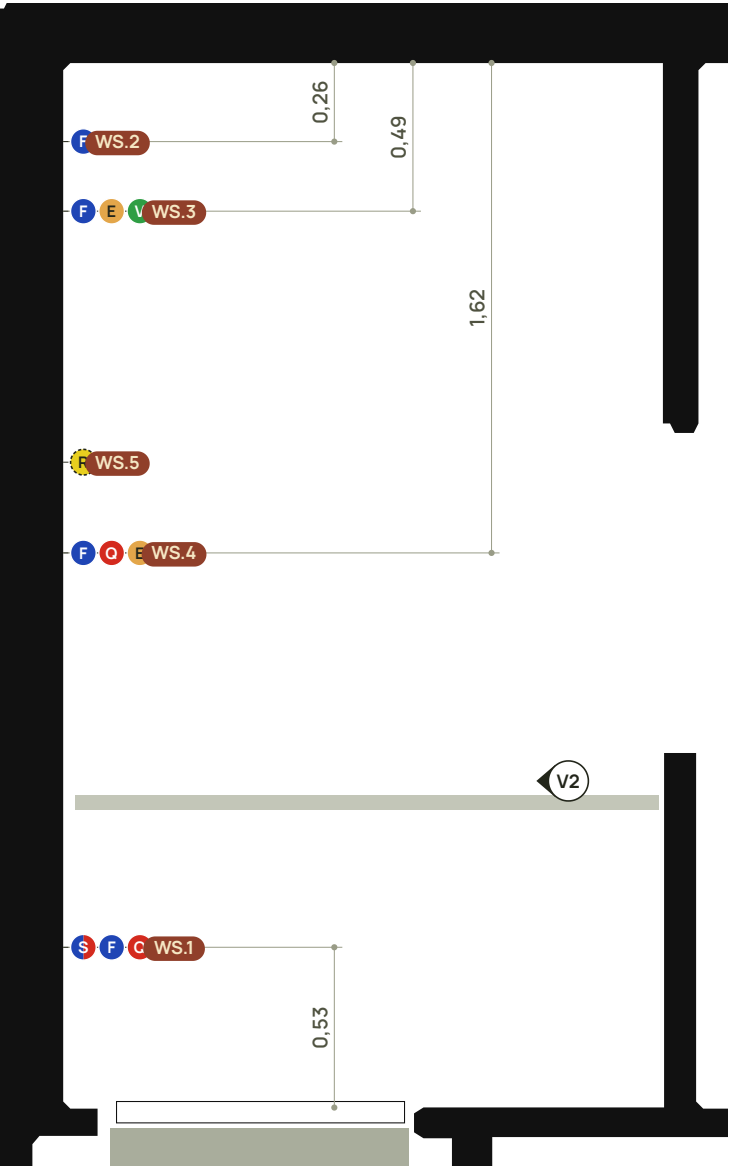


4 WC 01 e WC 02

Escala 1:25 · pontos W1.1 a W1.5 e W2.1 a W2.5 (espelhado)

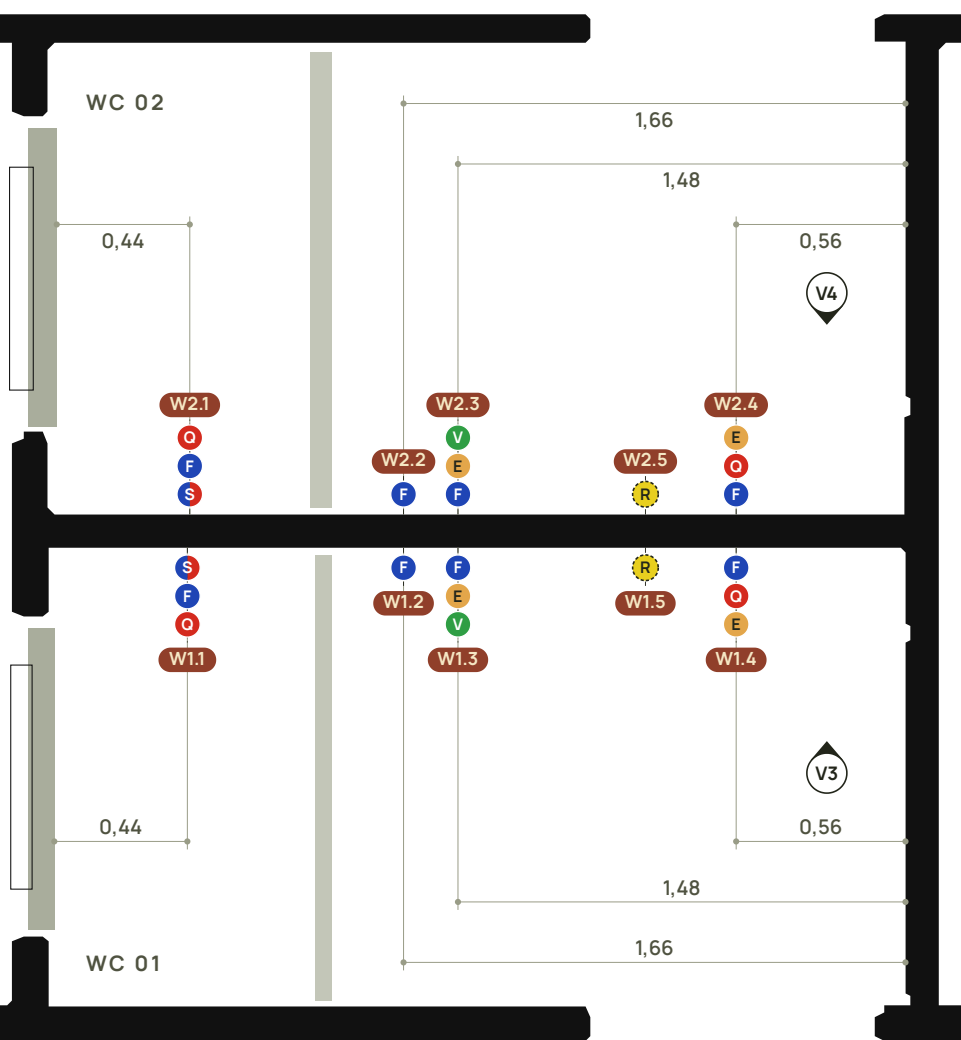


7 WC Externo

Escala 1:25 · pontos WE.1 a WE.5

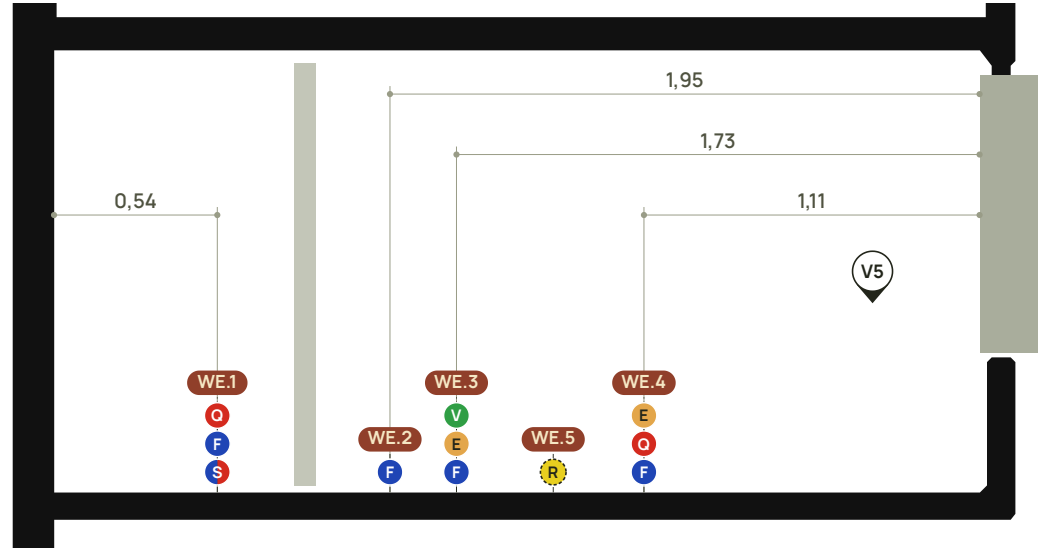

V2 WC Suíte Master

Escala 1:50 · do interior · alturas do piso acabado

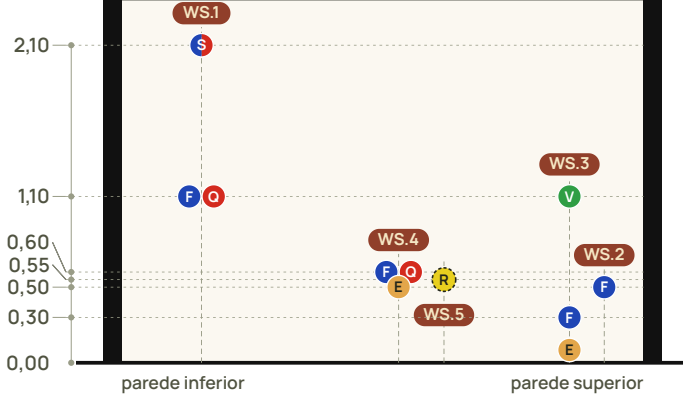


V3 WC 01

Escala 1:50 · do interior · alturas do piso acabado




V4 WC 02

Escala 1:50 · do interior · alturas do piso acabado

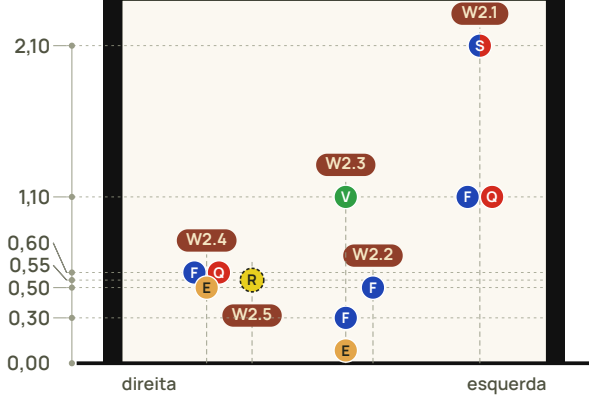

V5 WC Externo

Escala 1:50 · do interior · alturas do piso acabado

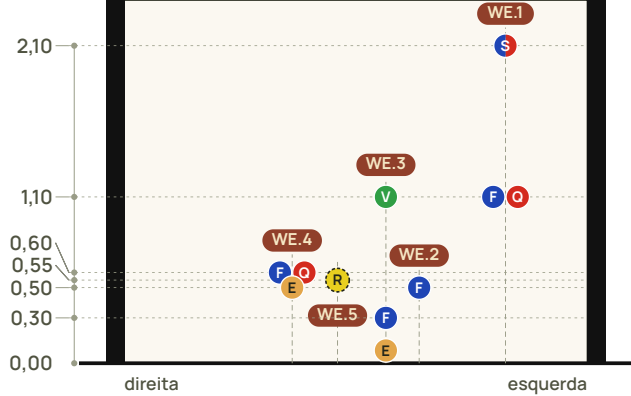

03 Ampliações · banheiros

Plantas 1:25 · vistas 1:50 · plotagem em A2 · cotas em metros a partir da face da parede indicada



Pontos e alturas

QUADRO 1

CÓD.	PEÇA · EIXO	ALTURAS (m) · FONTE
WC 01		
W1.1	Chuveiro 0,44 da parede esquerda S 2,10 ^C F 1,10 ^C O 1,10 ^C	
W1.2	Ducha higiênica 1,66 da parede direita F 0,50 ^P	
W1.3	Bacia sanitária 1,48 da parede direita F 0,30 ^P E piso ^C V 1,10 ^P	
W1.4	Cuba · torneira de bancada 0,56 da parede direita F 0,60 ^C O 0,60 ^D E 0,50 ^P	
W1.5	Registro geral sem cota · dentro do armário R 0,55 ^P	
WC 02 (ESPELHADO)		
W2.1	Chuveiro 0,44 da parede esquerda S 2,10 ^C F 1,10 ^C O 1,10 ^C	
W2.2	Ducha higiênica 1,66 da parede direita F 0,50 ^P	
W2.3	Bacia sanitária 1,48 da parede direita F 0,30 ^P E piso ^C V 1,10 ^P	
W2.4	Cuba · torneira de bancada 0,56 da parede direita F 0,60 ^C O 0,60 ^D E 0,50 ^P	
W2.5	Registro geral sem cota · dentro do armário R 0,55 ^P	
WC SUÍTE MASTER		
WS.1	Chuveiro 0,53 da parede inferior S 2,10 ^C F 1,10 ^C O 1,10 ^C	
WS.2	Ducha higiênica 0,26 da parede superior F 0,50 ^P	
WS.3	Bacia sanitária 0,49 da parede superior F 0,30 ^P E piso ^C V 1,10 ^P	
WS.4	Cuba · torneira de bancada 1,62 da parede superior F 0,60 ^C O 0,60 ^D E 0,50 ^P	
WS.5	Registro geral sem cota · dentro do armário R 0,55 ^P	
WC EXTERNO		
WE.1	Chuveiro 0,54 da parede esquerda S 2,10 ^C F 1,10 ^C O 1,10 ^C	
WE.2	Ducha higiênica 1,95 da parede direita F 0,50 ^P	
WE.3	Bacia sanitária 1,73 da parede direita F 0,30 ^P E piso ^C V 1,10 ^P	
WE.4	Torneira de bancada 1,11 da parede direita F 0,60 ^D O 0,60 ^D E 0,50 ^P	
WE.5	Registro geral sem cota · dentro do armário R 0,55 ^C	

Legenda

QUADRO 2

F	Água fria	R	Ponto com eixo sem cota
O	Água quente	W1.3	Código do ponto
E	Esgoto	4	Ampliação (Quadro 1)
V	Válvula de descarga	1,00	Cota em metros
R	Registro geral		Alvenaria
S	Saída de chuveiro (misturada)		Janela / vidro

Letra no círculo = serviço. Altura do piso acabado ao eixo do ponto.

Observações técnicas

QUADRO 3

- Chuveiro**
Saída de chuveiro a 2,10 e registro misturador (AF/AQ) a 1,10, no mesmo eixo. Sem chuveiro elétrico.
- Bacia**
Alimentação a 0,30, esgoto no piso e válvula de descarga a 1,10 no eixo da bacia.
- Registro geral**
A 0,55, dentro do armário da bancada. Eixo sem cota (marcador tracejado): definir com a marcenaria.
- Referências**
WC 01, WC 02 e WC Externo: chuveiro pela parede esquerda, demais peças pela direita. WC Suíte Master: peças pela parede superior, chuveiro pela inferior. Vistas esquemáticas: eixos e alturas, sem louças.

Revisões sobre o caderno

QUADRO 3 A

PEÇA	CADERNO	PLANTA
WC 01 e WC 02		
Ducha higiênica	1,20 (esq.)	1,66 (dir.)
Bacia	1,40 (esq.)	1,48 (dir.)
Cuba	2,35 (esq.)	0,56 (dir.)
Chuveiro	0,45	0,44
WC Suíte Master		
Ducha higiênica	0,25	0,26
Bacia	0,45	0,49
Cuba	1,60	1,62
Chuveiro (da inferior)	0,55	0,53
WC Externo		
Chuveiro	0,55	0,54
Bacia (da dir.)	1,75	1,73
Torneira (da dir.)	1,15	1,11

Vale a planta de 29/09. No WC 01/02 a soma das cotas do caderno (2,90) excedia a largura do ambiente.



CARIMBO

PROJETO
Residência Ivan e Ana Neris
Nova Odessa - SP

RESPONSÁVEIS TÉCNICAS
Lidiane Barbosa · CAU A290220-6
Isadora Ferrari · CAU A269382-8

PLANTA
Pontos hidráulicos · banheiros

ESCALA
1:25 e 1:50 · folha A2

DATA
30/09/2026

PRANCHA
03/04

REVISÃO
R01


0 — 2 m (1:25)

Conferir as medidas no local

1

Implantação da piscina


Escala 1:100 · * cotas medidas na planta de layout (01/05/2026) · a conferir

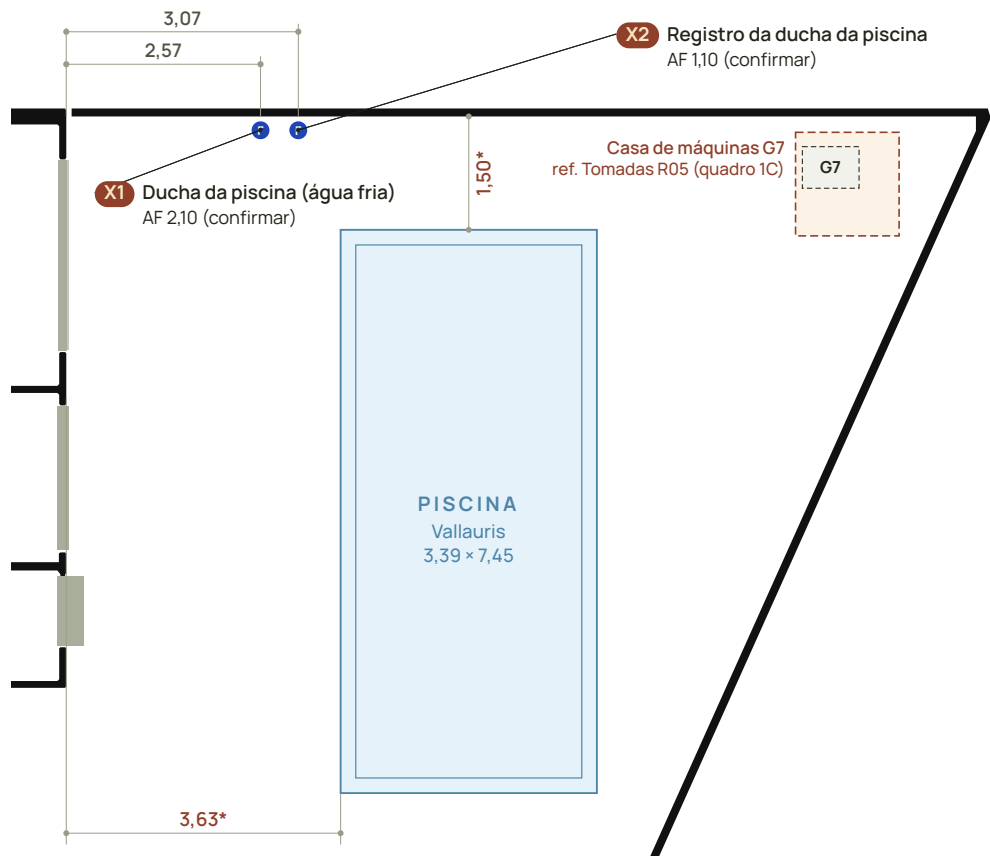

3

Modelo Vallauris · planta


Escala 1:50 · redesenhado do desenho técnico iGui (01/01)

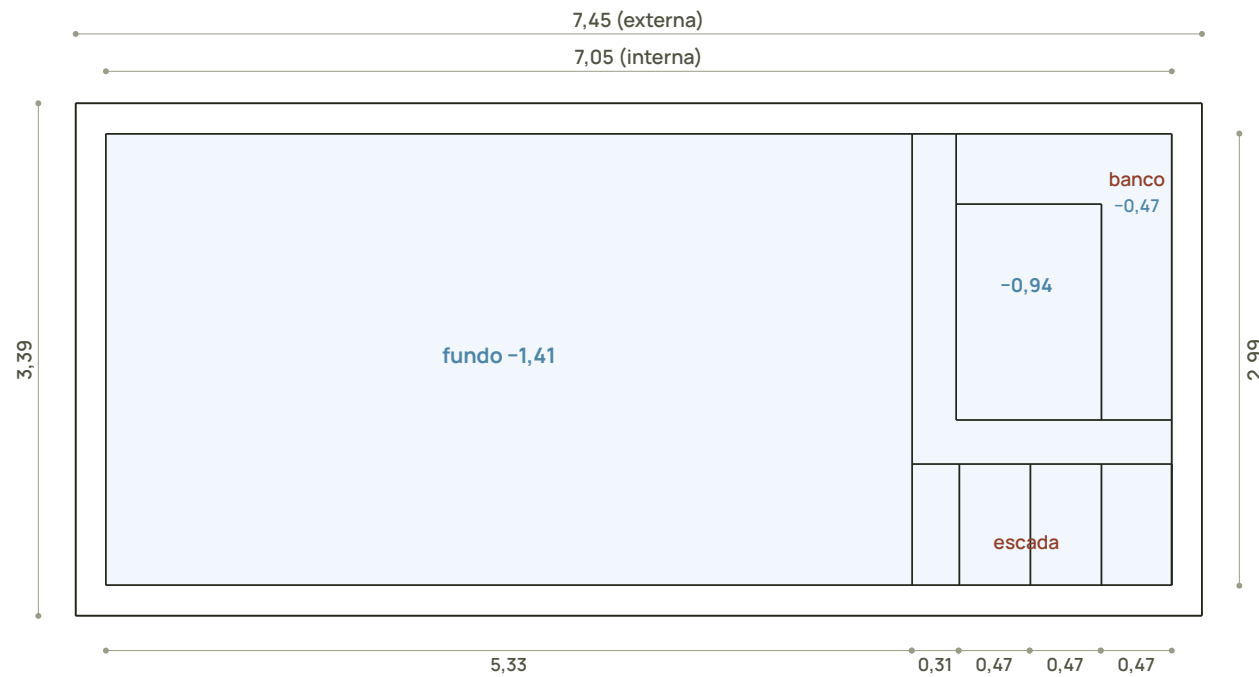

4

Corte longitudinal


Escala 1:50 · iGui

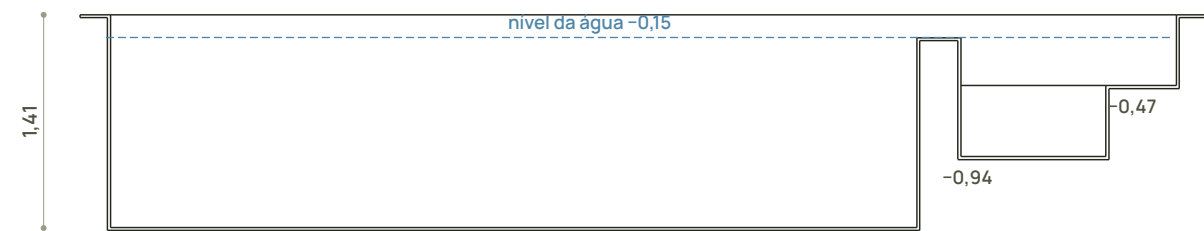

5

Corte transversal

Escala 1:50 · iGui

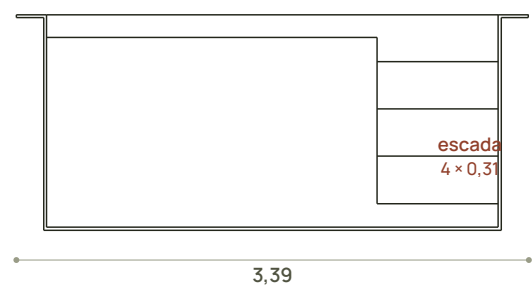

04

Piscina Vallauris · pontos hidráulicos


Implantação 1:100 · modelo e cortes 1:50 · plotagem em A2



2

Esquema dos pontos

Sem escala · funcional · não indica trajeto nem diâmetro

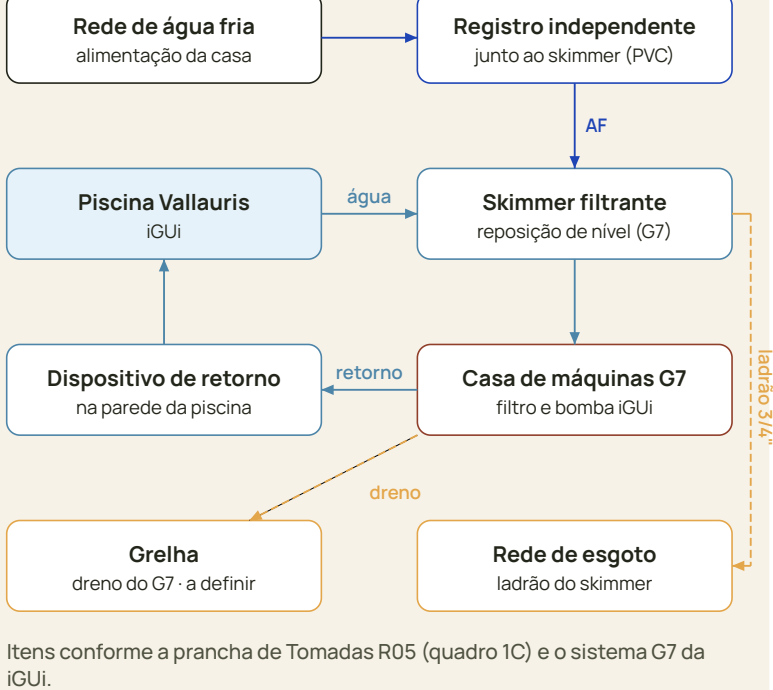

Itens conforme a prancha de Tomadas R05 (quadro 1C) e o sistema G7 da iGui.

Pontos da piscina

QUADRO 1

Nº	ITEM · ORIGEM DA INFORMAÇÃO	POSIÇÃO
X1	Ducha de água fria Saída a 2,10 m* · 2,57 da face externa da Suíte Master, no muro. Planta de pontos (29/09).	cotada
X2	Registro da ducha A 1,10 m* · 3,07 da mesma face, no muro. Planta de pontos (29/09).	cotada
P1	Reposição de água (AF) Registro independente junto ao skimmer, em PVC (Tomadas R05, quadro 1C).	iGui
P2	Skimmer filtrante Sistema G7 da iGui.	iGui
P3	Dispositivo de retorno Sistema G7 da iGui; ligação à casa de máquinas.	iGui
P4	Ladrão 3/4" do skimmer Para a rede de esgoto (Tomadas R05, quadro 1C).	iGui
P5	Dreno do G7 Para a grelha (Tomadas R05, quadro 1C). Grelha não localizada nos arquivos.	a definir
G7	Casa de máquinas Canto superior do lote, junto ao muro, como na prancha de Tomadas R05.	ref. elétrica

* Alturas da ducha adotadas do padrão do chuveiro: confirmar. Pontos P1 a P5 sem cota: posição, trajeto e diâmetro conforme a instaladora iGui e o projeto hidrossanitário.

Modelo Vallauris

QUADRO 1A

Fabricante	iGui · desenho técnico Vallauris 01/01
Medidas externas	7,45 × 3,39 m (borda de 0,20)
Medidas internas	7,05 × 2,99 m
Profundidade	1,41 m no fundo
Plataforma	0,96 m a -0,94 m
Banco	0,47 m a -0,47 m
Escada	4 degraus de 0,31 m · largura 0,80 m
Nível da água	0,15 m abaixo da borda
Estrutura	Mão francesa ao longo da borda e reforços a cada 45 cm, em média (iGui)
Implantação	Borda externa a 3,63 m da fachada da Suíte Master e a 1,50 m do muro, medidas na planta de layout (01/05/2026) · a conferir
Orientação	Lado da escada e do banco a definir com a iGui

Legenda

QUADRO 2

Água fria	Ponto com eixo sem cota
Água quente	Código do ponto
Esgoto	Ampliação (Quadro 1)
Válvula de descarga	Cota em metros
Registro geral	Alvenaria
Saída de chuveiro (misturada)	Janela / vidro

Letra no círculo = serviço. Altura do piso acabado ao eixo do ponto.

Observações técnicas

QUADRO 3

- Escopo**
Localização dos pontos hidráulicos ligados à piscina. Instalação, tubulação e equipamentos conforme o manual da iGui e o projeto hidrossanitário.
- Implantação**
Posição da piscina medida graficamente na planta de layout (Rev. 01). Conferir no local e com o projeto de implantação antes da escavação.
- Ducha**
Ducha de água fria com registro próprio, no muro, entre a casa e a piscina.
- Elétrica**
Q.C. MAX, conduites e trocador de calor conforme a prancha de Tomadas R05 (quadro 1C). Equipotencialização da piscina conforme NBR 5410.
- Normas**
NBR 10339 (piscinas) e NBR 5626 (água fria e água quente).

DUAS

duas design & arq

CARIMBO

PROJETO

Residência Ivan e Ana Neris

Nova Odessa - SP

RESPONSÁVEIS TÉCNICAS

Lidiane Barbosa · CAU A290220-6

Isadora Ferrari · CAU A269382-8

PLANTA

Pontos hidráulicos · piscina

ESCALA

1:100 e 1:50 · folha A2

DATA

30/09/2026

PRANCHA

04/04

REVISÃO

R01

0 — 4 m (1:50)

Conferir as medidas no local