


01 **Planta de tomadas**
Escala 1:100 · plotagem em A2

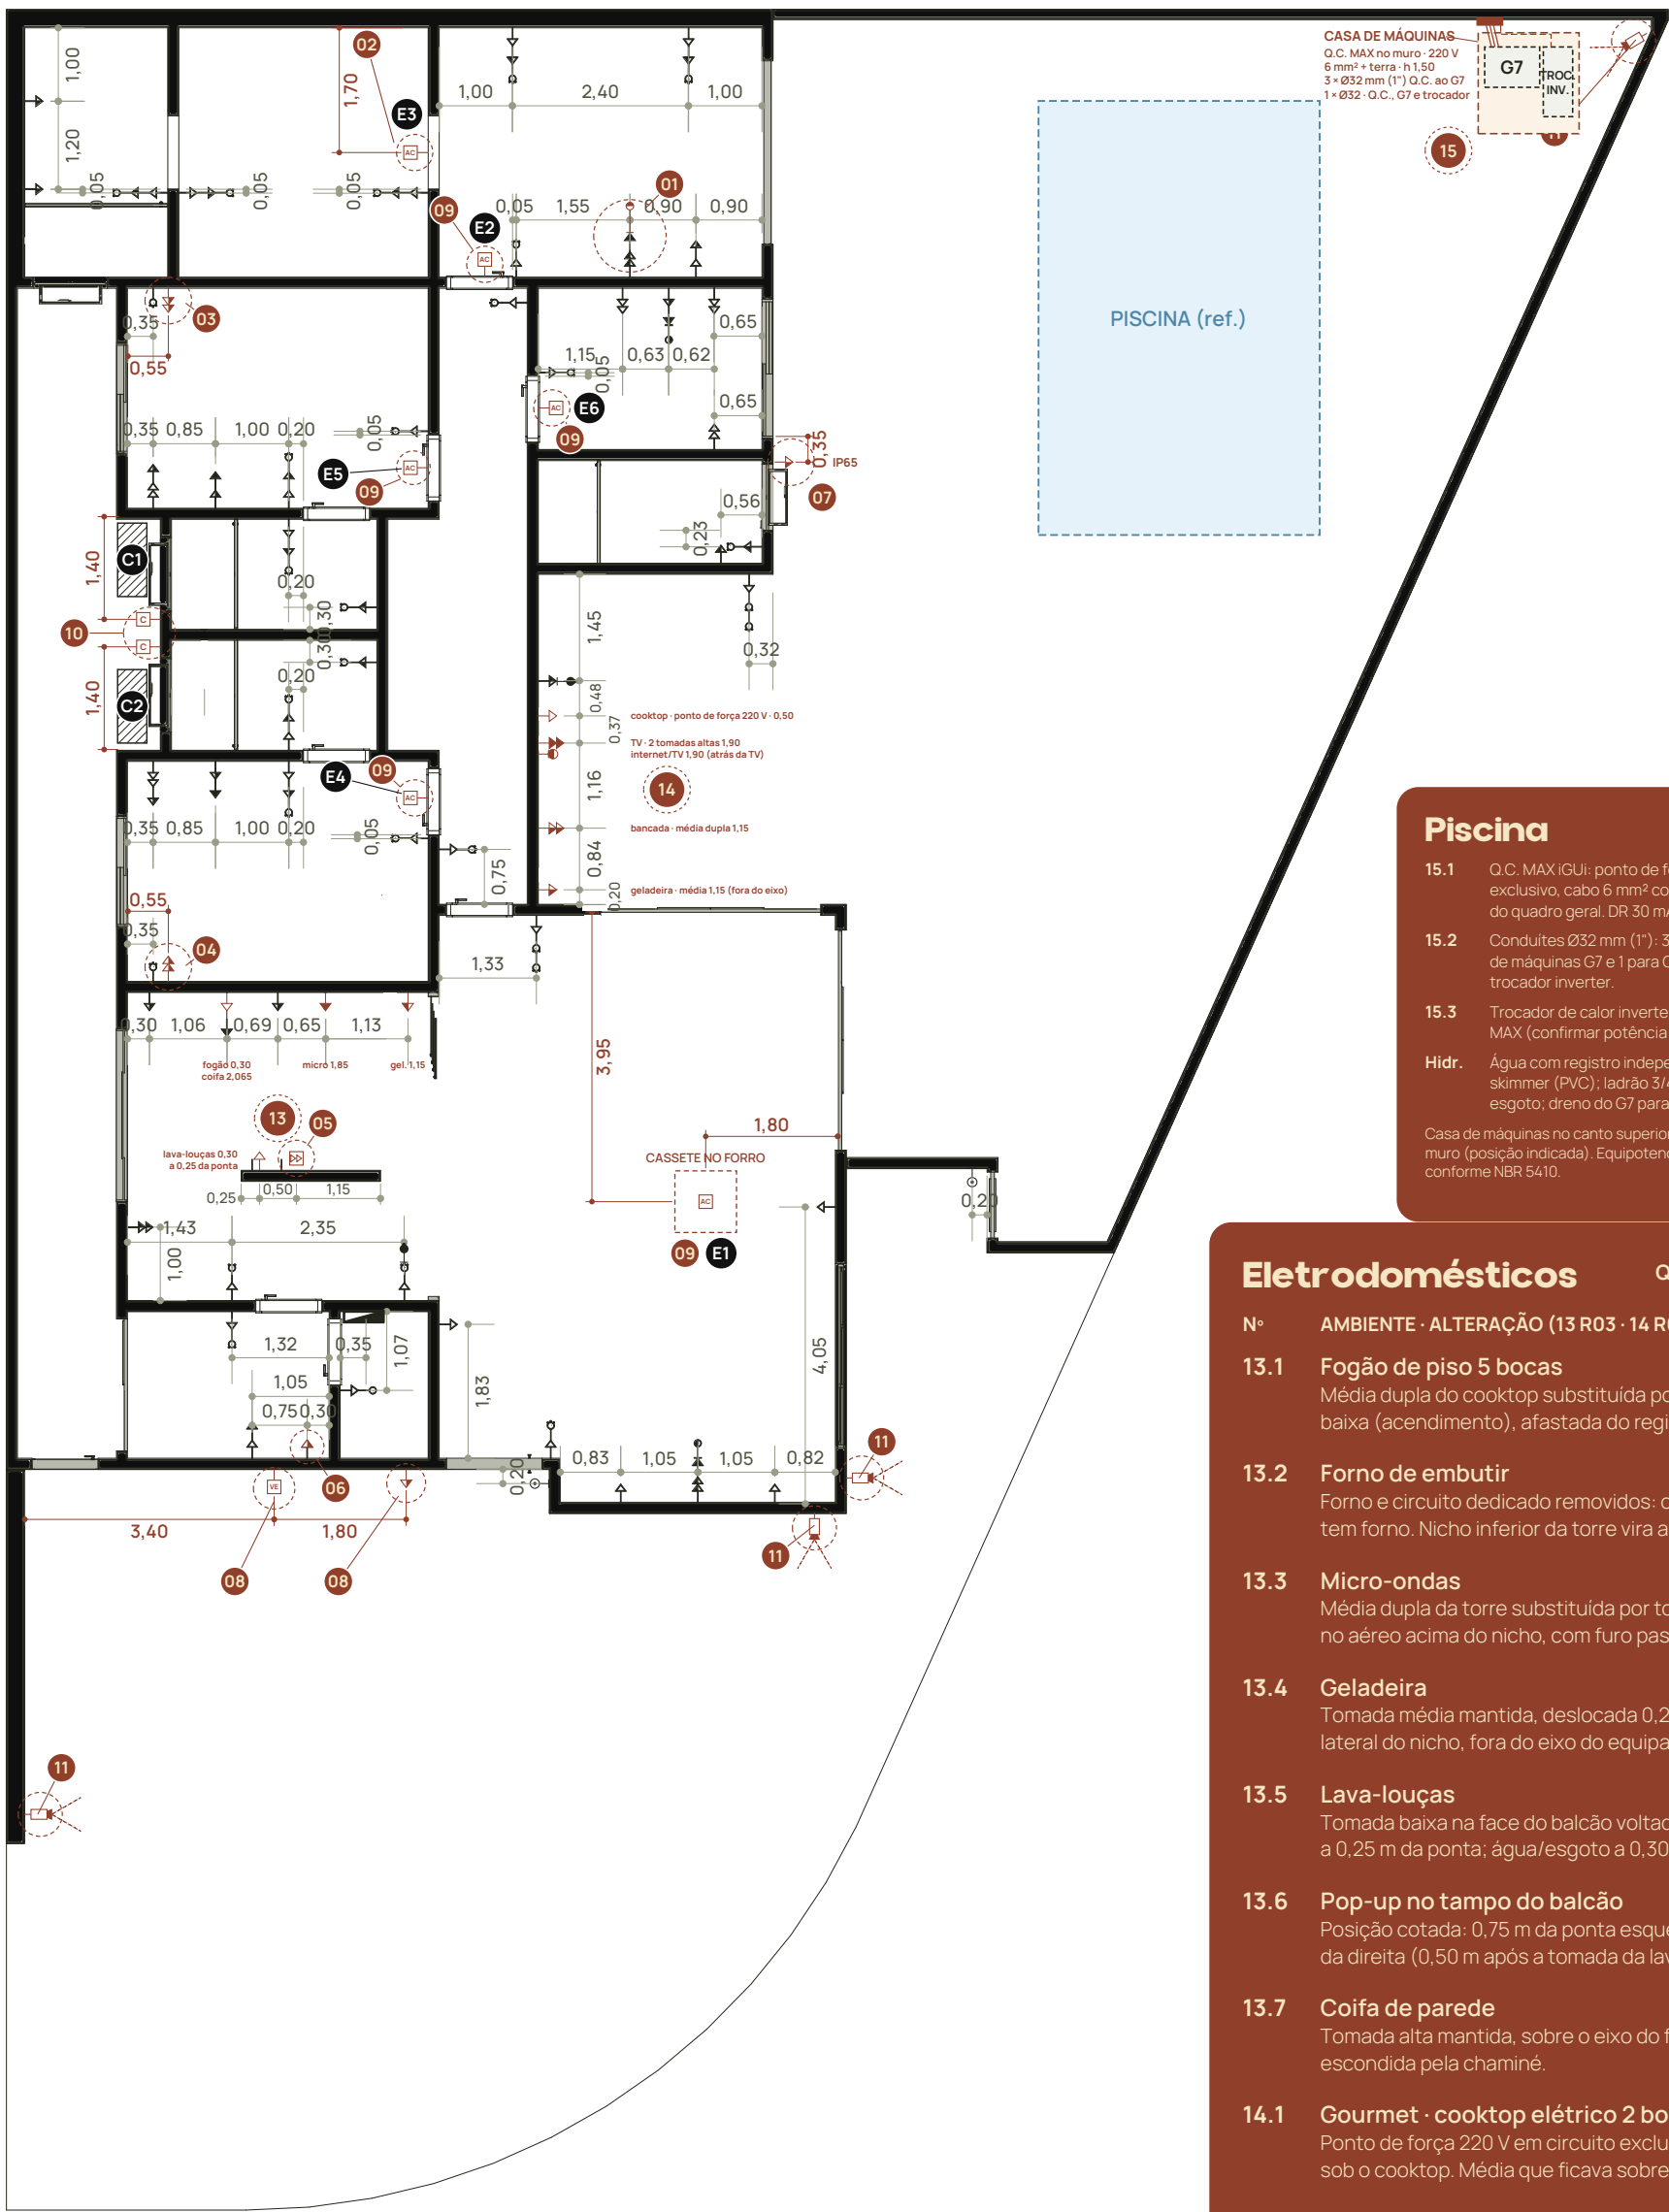

Eletrodomésticos			QUADRO 1B
Nº	AMBIENTE · ALTERAÇÃO (13 R03 · 14 R04)	ALTURA	
13.1	Fogão de piso 5 bocas	0,30 m	
Média dupla do cooktop substituída por tomada baixa (acendimento), afastada do registro de gás.			
13.2	Forno de embutir	REMOÇÃO	
Forno e circuito dedicado removidos: o fogão já tem forno. Nicho inferior da torre vira armário.			
13.3	Micro-ondas	1,85 m	
Média dupla da torre substituída por tomada alta no aéreo acima do nicho, com furo passa-cabo.			
13.4	Geladeira	1,15 m	
Tomada média mantida, deslocada 0,25 m para a lateral do nicho, fora do eixo do equipamento.			
13.5	Lava-louças	0,30 m	
Tomada baixa na face do balcão voltada à cozinha, a 0,25 m da ponta; água/esgoto a 0,30 m no mínimo.			
13.6	Pop-up no tampo do balcão	TAMPO	
Posição cotada: 0,75 m da ponta esquerda e 1,15 m da direita (0,50 m após a tomada da lava-louças).			
13.7	Coifa de parede	2,065 m	
Tomada alta mantida, sobre o eixo do fogão, escondida pela chaminé.			
14.1	Gourmet · cooktop elétrico 2 bocas	0,50 m	
Ponto de força 220 V em circuito exclusivo, no gabinete sob o cooktop. Média que ficava sobre ele removida.			
14.2	Gourmet · TV alta	1,90 m	
2 tomadas altas + internet/TV atrás da TV, centro a 2,20 m da parede da geladeira.			
14.3	Gourmet · bancada	1,15 m	
Média dupla movida de junto da cuba (2,30 m) para 3,46 m, entre a cuba e a geladeira.			
14.4	Gourmet · geladeira	1,15 m	
Tomada média deslocada 0,22 m, fora do eixo do equipamento. Churrasqueira a carvão: sem ponto.			
Cozinha conforme elevação; área gourmet conforme croqui. Alturas a partir do piso acabado. Conferir no manual de cada equipamento. Pendente: voltagens (127/220 V). R04: cassete E1 do estar reposicionado (1,80 × 3,95 m).			

Pontos revisados			QUADRO 1
Nº	AMBIENTE · ALTERAÇÃO	TIPO	
01	Suíte Master Ponto de internet I TV junto ao ponto da TV.	ACRÉSCIMO	
02	Closet Tomada alta sobre a porta convertida em ponto da evaporadora E3, a 2,50 m (a 2,00 m ficava na altura do vão da porta).	ALTERAÇÃO	
03	Suíte 2 Tomada média dupla junto à cama, a 0,55 m da parede.	ACRÉSCIMO	
04	Suíte 1 Tomada média dupla junto à cama, a 0,55 m da parede.	ACRÉSCIMO	
05	Cozinha Tomadas baixas da base da ilha substituídas por tomada pop-up dupla no tampo.	ALTERAÇÃO	
06	Área de serviço Tomada da lavadora alterada de baixa para média, em circuito dedicado.	ALTERAÇÃO	
07	Área externa Tomada média externa IP65 com tampa, na fachada lado piscina.	ACRÉSCIMO	
08	Garagem Tomada média de uso geral e carregador de veículo elétrico (1,30 m, 220 V).	ACRÉSCIMO	
09	Ar-condicionado Pontos das evaporadoras E1, E2, E4, E5 e E6 (Quadro 1A).	ACRÉSCIMO	
10	Corredor externo Pontos de força das condensadoras C1 e C2, no recuo junto aos banhos (Quadro 1A).	ACRÉSCIMO	
11	Área externa e garagem Quatro pontos de câmera (CFTV) nas posições indicadas.	ACRÉSCIMO	
12	Banhos	REMOÇÃO	
Planta: itens em terracota, numerados conforme este quadro (o item 12 é remoção, sem marcação). Demais pontos conforme a Revisão 01.			

Ar-condicionado			QUADRO 1A
Pontos conforme a planta de ar condicionado R01. Condensadoras no recuo do corredor externo.			
Nº	AMBIENTE · EQUIPAMENTO	ALTURA	
E1	01 Estar/Jantar Cassete de forro · reposicionado na R04	Forro	
E2	02 Suíte Master Hi-Wall · acima da porta	2,50 m	
E3	03 Closet Hi-Wall · acima da porta	2,50 m	
E4	04 Suíte 1 Hi-Wall · acima da porta	2,50 m	
E5	05 Suíte 2 Hi-Wall · acima da porta	2,50 m	
E6	06 Home Office Hi-Wall · acima da porta	2,50 m	
C1	Condensadora · ala das suítes E2 + E4 + E5 · circuito dedicado	1,50 m	
C2	Condensadora · closet, office e social E1 + E3 + E6 · circuito dedicado	1,50 m	

Legenda			QUADRO 2
	Quadro de distribuição		Tomada pop-up no tampo
	Interfone		Carregador VE · 130 cm
	Botão de campainha		Ponto de câmera (CFTV)
	Interruptor 1 tecla		Evaporadora hi-wall · 250 cm
	Interruptor 2 teclas		Evaporadora cassete · forro
	Interruptor 3 teclas		Ponto condensadora · 150 cm
	Internet I TV · 30 cm		Condensadora (equip.)
	Tomada baixa · 30 cm		Evaporadora (Quadro 1A)
	Tomada baixa dupla · 30 cm		Item revisado (Quadro 1)
	Tomada média · 115 cm		Alvenaria
	Tomada média dupla · 115 cm		Cota em metros
	Tomada média dupla · 115 cm		
	Tomada alta · 200 cm		

Observações técnicas			QUADRO 3
1. Pontos de câmera Quatro pontos de CFTV conforme planta (item 11). Altura, modelo e cabeamento A DEFINIR com o fornecedor do sistema.			
2. Alturas Alturas de instalação indicadas na legenda, a partir do piso acabado. Alguns pontos terão ajuste de altura de acordo com a finalidade do eletrônico ou eletrodoméstico que ficará próximo.			
3. Circuitos dedicados Circuito exclusivo para lavadora, carregador de veículo elétrico (220 V) e condensadoras C1 e C2, com disjuntor dimensionado conforme o equipamento (NBR 5410). Chuveiros com água quente e fria: sem ponto de chuveiro elétrico.			
4. Proteção Tomadas de áreas molhadas e externas protegidas por dispositivo DR (NBR 5410). Tomada externa com grau de proteção IP65 e tampa.			
5. Ar-condicionado Multi-split: as evaporadoras normalmente são alimentadas pela condensadora, por cabo de interligação — confirmar no manual Gree do modelo. Hi-wall acima da porta de cada ambiente: conferir a altura livre entre porta e teto. Condensadoras no recuo do corredor externo, respeitando os afastamentos do manual Gree. Tubulação frigorígena e dreno conforme a planta de ar condicionado.			
6. Compatibilização Conferir as medidas no local. Compatibilizar os pontos com a marcenaria antes da execução.			
7. Normas e referências NBR 5410 (instalações elétricas de baixa tensão) e NBR 14136 (plugues e tomadas para uso doméstico).			

PROJETO
Residência Ivan e Ana Neris
Nova Odessa – SP

RESPONSÁVEIS TÉCNICAS
Lidiane Barbosa · CAU A290220-6
Isadora Ferrari · CAU A263982-8

PLANTA
Tomadas

ESCALA
1:100 · folha A2

DATA
30/09/2026

PRANCHA
01/04

REVISÃO
R05