



1 Planta de localização

Escala 1:100 · abrigo de GLP e ponto do fogão

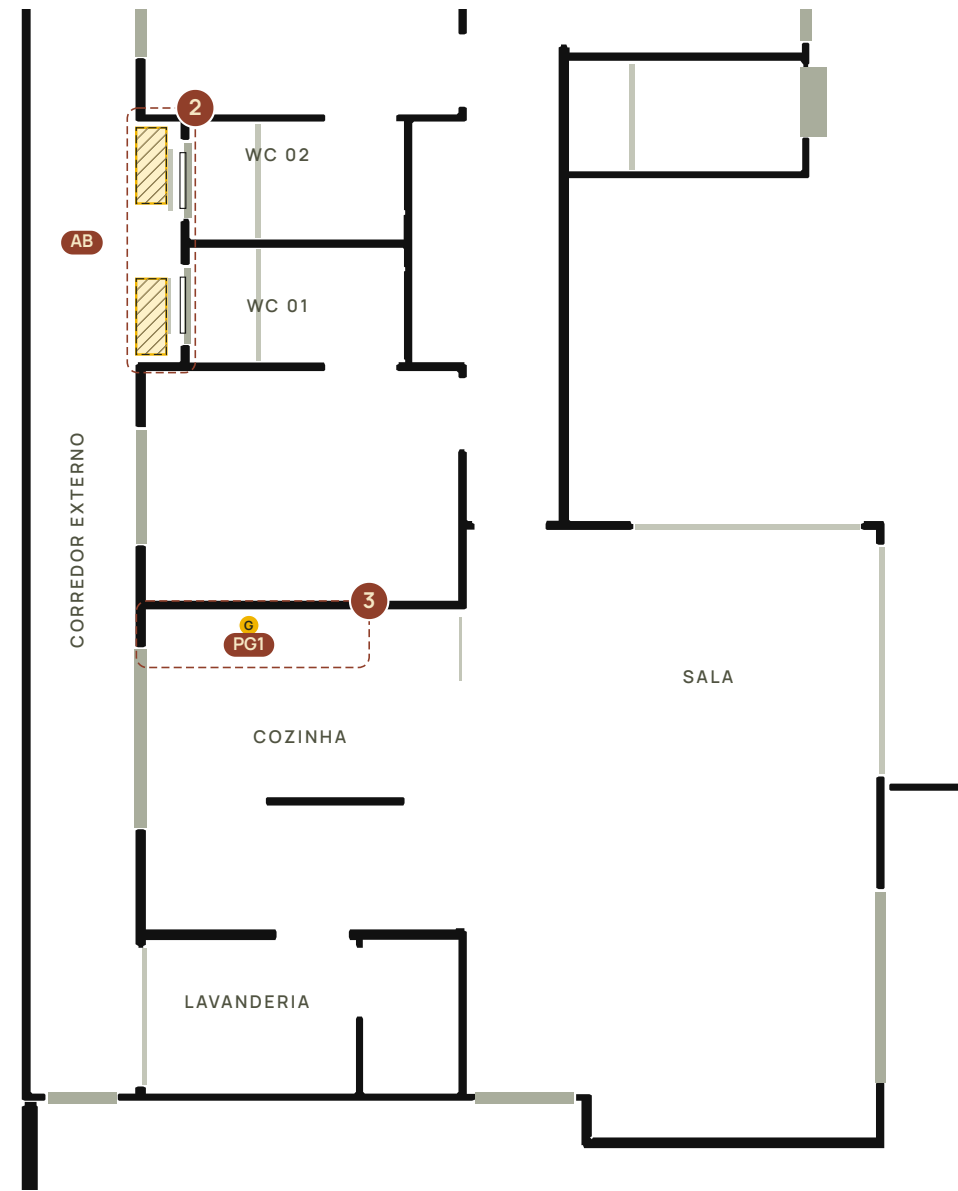

3 Cozinha · parede do fogão

Escala 1:25 · ponto PG1

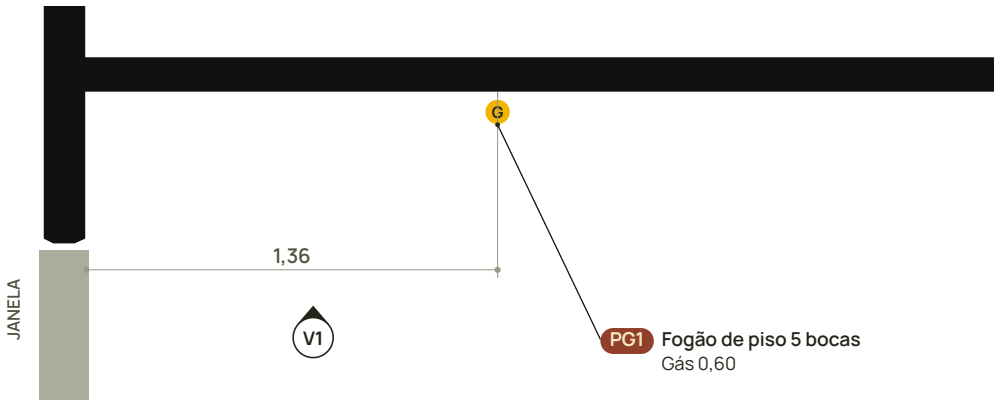


01 Pontos de gás · GLP

Plotagem em A2 · cotas em metros a partir da face da parede indicada



2 Abrigo de GLP · corredor externo

Escala 1:25 · sob as condensadoras C1 e C2

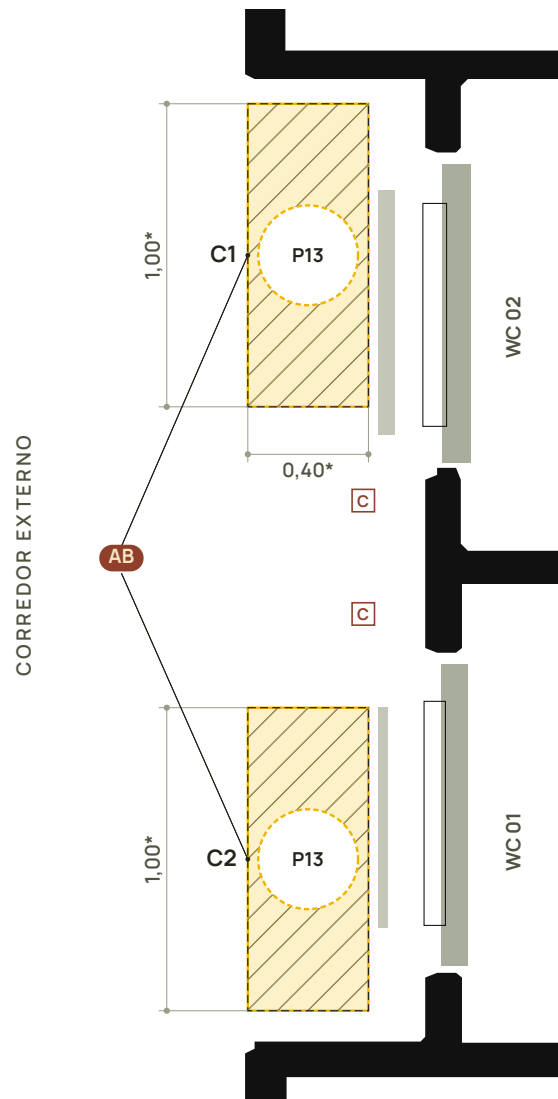

* Projeção das condensadoras na prancha de Tomadas R05 (1,00 x 0,40 cada). Dimensões finais do abrigo, porta e ventilação a definir. Tomadas C a 1,50 m, acima do abrigo (Tomadas R05, item 10).

VI Vista da parede do fogão

Escala 1:25 · do interior · alturas do piso acabado



Pontos de gás

QUADRO 1

CÓD.	ITEM · POSIÇÃO	ALTURA
AB	Abrigo de GLP · 2 botijões P13 No recuo do corredor externo, sob as condensadoras C1 e C2, na projeção de cada uma (1,00 x 0,40, conforme a prancha de Tomadas R05). Disposição dos botijões esquemática. Dimensões finais, porta, ventilação e fixação a definir com o fornecedor e o responsável técnico.	piso
PG1	Fogão de piso 5 bocas · cozinha 1,36 da parede da janela, na parede superior da cozinha: mesmo eixo do fogão e da coifa na prancha de Tomadas R05. Altura definida pelo cliente em 01/10/2026.	0,60 m

Único ponto de consumo: cooktop do gourmet, secadora e trocador da piscina são elétricos e a churrasqueira é a carvão (Tomadas R05 e definições de 30/09). Trajeto da tubulação, diâmetros, regulador e registros: projeto de gás (NBR 15526), por profissional habilitado.

Compatibilização

QUADRO 1A

Condensadoras	C1 e C2 (Gree G-Max multisplit 48.000 BTU/h) acima do abrigo. Altura de instalação e suporte a definir; localização ainda A CONFIRMAR no caderno de ar condicionado.
Tomadas C	Pontos de força das condensadoras a 1,50 m, entre C1 e C2 (Tomadas R05, item 10).
Janelas	As janelas do WC 01 e do WC 02 ficam atrás das condensadoras.
Fogão	Tomada de acendimento a 0,30 e tomada da coifa a 2,065 no mesmo eixo do ponto de gás (Tomadas R05, itens 13.1 e 13.7).

Verificar antes de executar

QUADRO 1B

- Afastamentos e ventilação do abrigo de GLP em relação a fontes de ignição (condensadoras e tomadas C), aberturas (janelas dos WCs), ralos e caixas, conforme NBR 13523, NBR 15526 e IT 28 do Corpo de Bombeiros de SP.
- Acesso para troca dos botijões e circulação livre no corredor externo.
- Afastamento entre o ponto de gás do fogão e a tomada de acendimento logo abaixo, no mesmo eixo.

Legenda

QUADRO 2

	Ponto de gás (GLP)		Código do ponto
	Abrigo de GLP		Ampliação
	Botijão P13 (esquemático)		Cota em metros
	Condensadora (projeção)		Alvenaria
	Tomada da condensadora		Janela / vidro

Altura do piso acabado ao eixo do ponto. Cores: amarelo = gás (NBR 6493).

Observações técnicas

QUADRO 3

- Escopo**
Localização do abrigo de GLP e do ponto de consumo. Não é projeto de gás: rede interna, diâmetros, trajeto, regulador, registros, teste de estanqueidade e ventilação seguem o projeto de gás do responsável técnico.
- Abrigo**
Dois botijões P13 sob as condensadoras C1 e C2, na projeção delas. Posição das condensadoras conforme a prancha de Tomadas R05; o caderno de ar condicionado ainda indica localização a confirmar.
- Fogão**
Ponto de gás a 0,60 do piso acabado, no eixo de 1,36 da parede da janela. Conexão do fogão conforme o fabricante.
- Alturas e cotas**
Alturas do piso acabado ao eixo. Cotas em metros, a partir da face da parede indicada. Conferir as medidas no local.
- Normas**
NBR 15526 (redes de distribuição interna de gases combustíveis), NBR 13523 (central de GLP) e IT 28 do Corpo de Bombeiros do Estado de São Paulo.



CARIMBO

PROJETO
Residência Ivan e Ana Neris
Nova Odessa - SP

RESPONSÁVEIS TÉCNICAS
Lidiane Barbosa · CAU A290220-6
Isadora Ferrari · CAU A269382-8

PLANTA
Pontos de gás (GLP)

ESCALA
1:100 e 1:25 · folha A2

0 — 2 m (1:25)

Conferir as medidas no local

DATA
01/10/2026

PRANCHA

01/01

REVISÃO

R01